


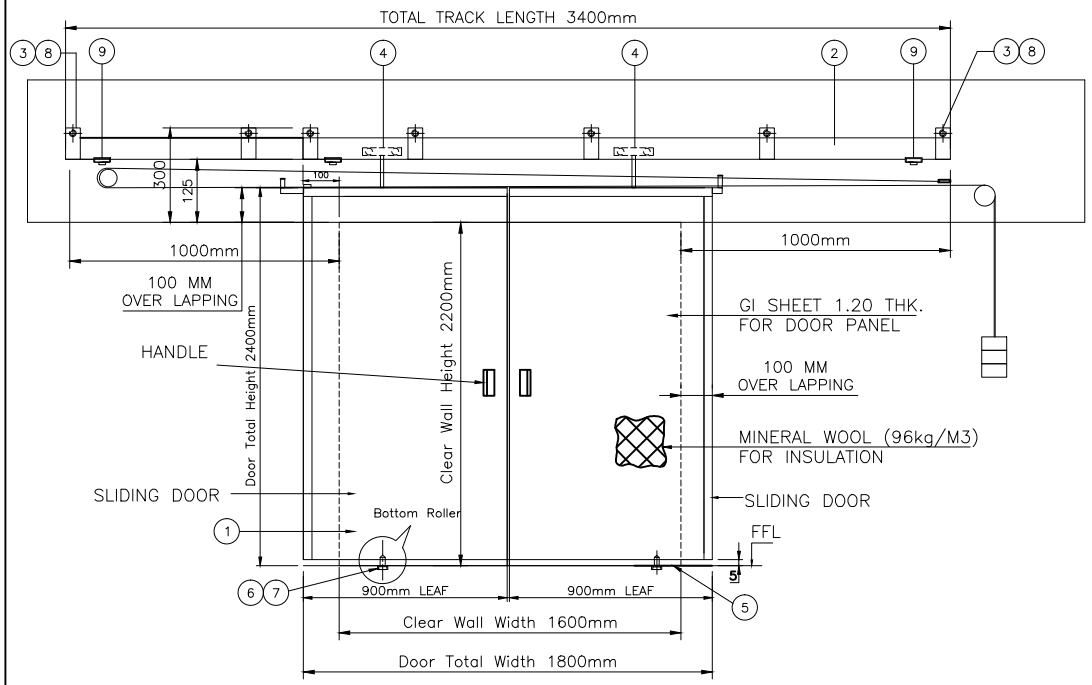


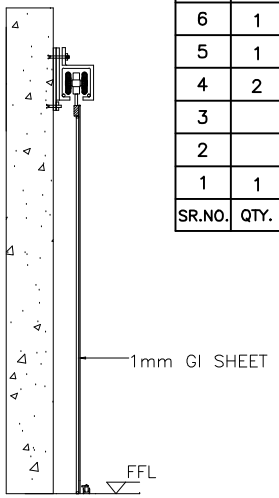


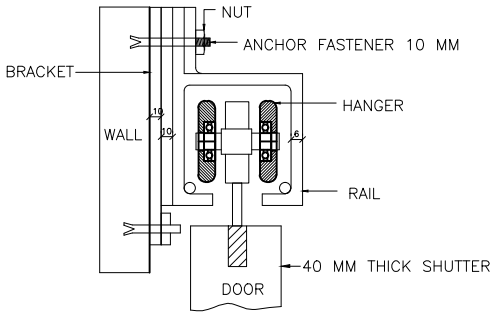

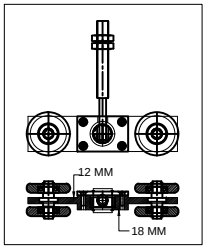


DETAIL AT 'B'

SR.NO.	QTY.	DESCRIPTION
9	1	STOPPER (FOR HANGER ASSLY.)
8	1	COVER (FOR TRACK BKT.)
7	1	BOTTOM ROLLER MTG. FLAT (BOTTOM ROLLER BKT.)
6	1	BOTTOM ROLLER ASSLY.
5	1	'Z' SECTION
4	2	HANGER ROLLER ASSLY./PANEL
3		TRACK BRACKET
2		SLIDING TRACK
1	1	SLIDING DOOR & FRAME / BACK SUPPORT SQ. TUBE

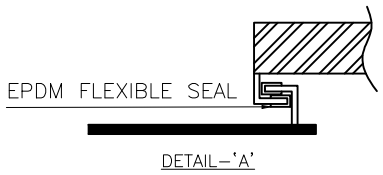

DETAIL–'A'

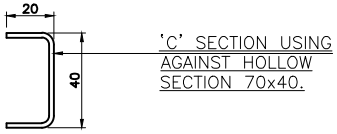

'C' SECTION USING AGAINST HOLLOW SECTION 70x40.

DETAIL–C PROFILE FOR FRAME

DOOR DIMENSION		
CLEAR WIDTH	CLEAR HEIGHT	
1600mm	2200mm	01NOS

Panel Make : - Radient Safe Door Make

NOTE : DOOR OVERLAPING 100mm AT RH & LH AND TOP SIDE
ALL DIMENSIONS ARE IN MM.
CLIENT SHOULD CONFIRM DOOR OPENING DIRECTION.

TOLERANCE:- ± 10mm

This drawing & designing is the property of NIHVA TECHNOLOGIES. Not to be sold or copied to any other concern.

TITLE: AUTOMATIC SLIDING DOOR				NIHVA TECHNOLOGIES PVT. LTD. PUNE
	NAME	SIGN	DATE	NIHVA TECHNOLOGIES PVT. LTD. Website:- www.nihva.com Tel : 020 66304033 Email:- info@nihva.com
DRAWN	SURAJ		21/11/18	CLIENT -
CHECK	P.A		20/11/18	PROJECT -
APPROVAL	R.D		20/11/18	SITE -
If any queries contact : design@nihva.com				DWG. NO. : NIHVA/18-19/0181/R02 REV-02
ALL DIMENSION ARE IN mm				SCALE: NTS WT: SHEET: 01 OF 01