



PRODUCED BY AN AUTODESK EDUCATIONAL PRODUCT

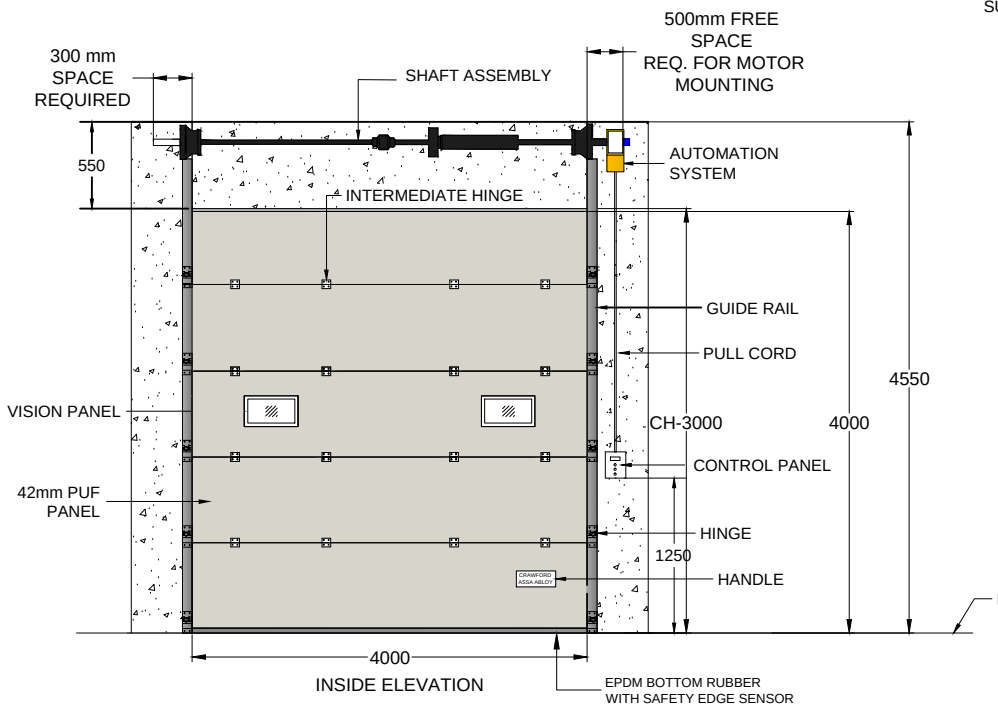

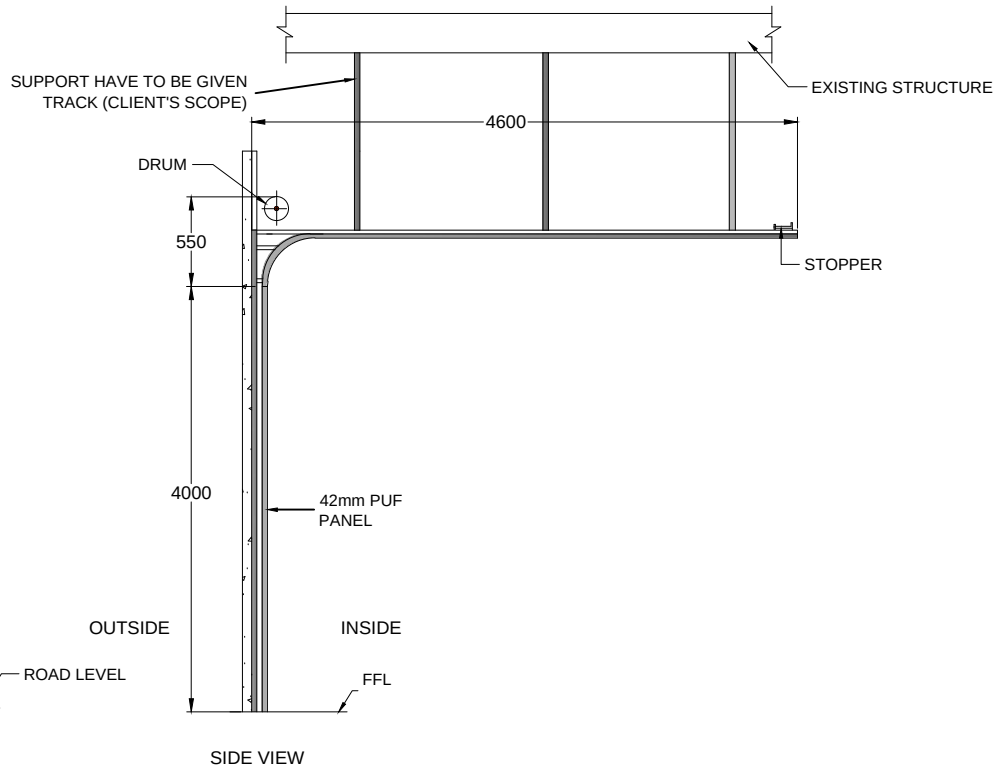

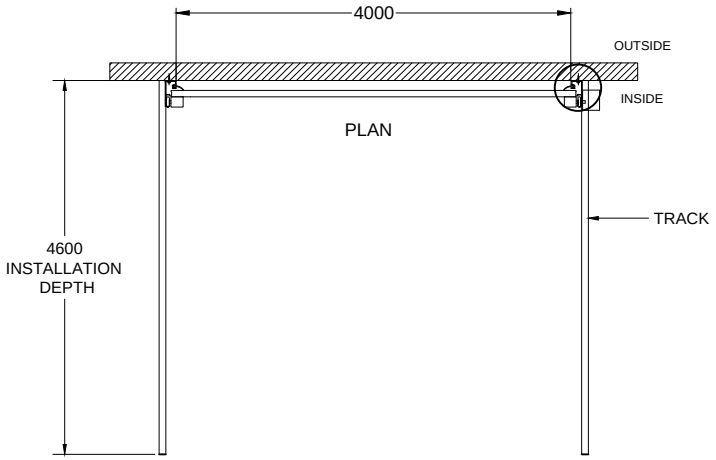

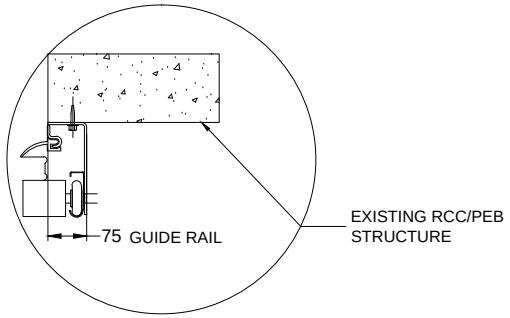

TRACK DETAILS

SR NO	CLEAR WIDTH	CLEAR HEIGHT	QTY
01	4000mm	4000mm	2

TOLERANCE: ±10mm

This drawing & design is the property of NIHVA TECHNOLOGIES. Not to be sold or copied to any other concern.

TITLE: SECTIONAL DOOR (VL)

NIHVA TECHNOLOGIES PVT. LTD.
NIHVA TECHNOLOGIES PVT. LTD. PUNE
Tel : 020 66304033
Email:- info@nihva.com
Website:- www.nihva.com

	NAME	SIGN	DATE
DRAWN	AKASH		04/09/18
CHECK	VIKRANT		04/09/18
APPROVAL	R.D		04/09/18

CLIENT -PROJECTSPOOL ENGG. SERVICE PVT. LTD.

PROJECT -

SITE -

If any queries contact : design@nihva.com

DWG. NO. : NIHVA/18-19/0122 REV: 0

ALL DIMENSION ARE IN mm

SCALE: NTS WT: SHEET: 01 OF 01

PRODUCED BY AN AUTODESK EDUCATIONAL PRODUCT