



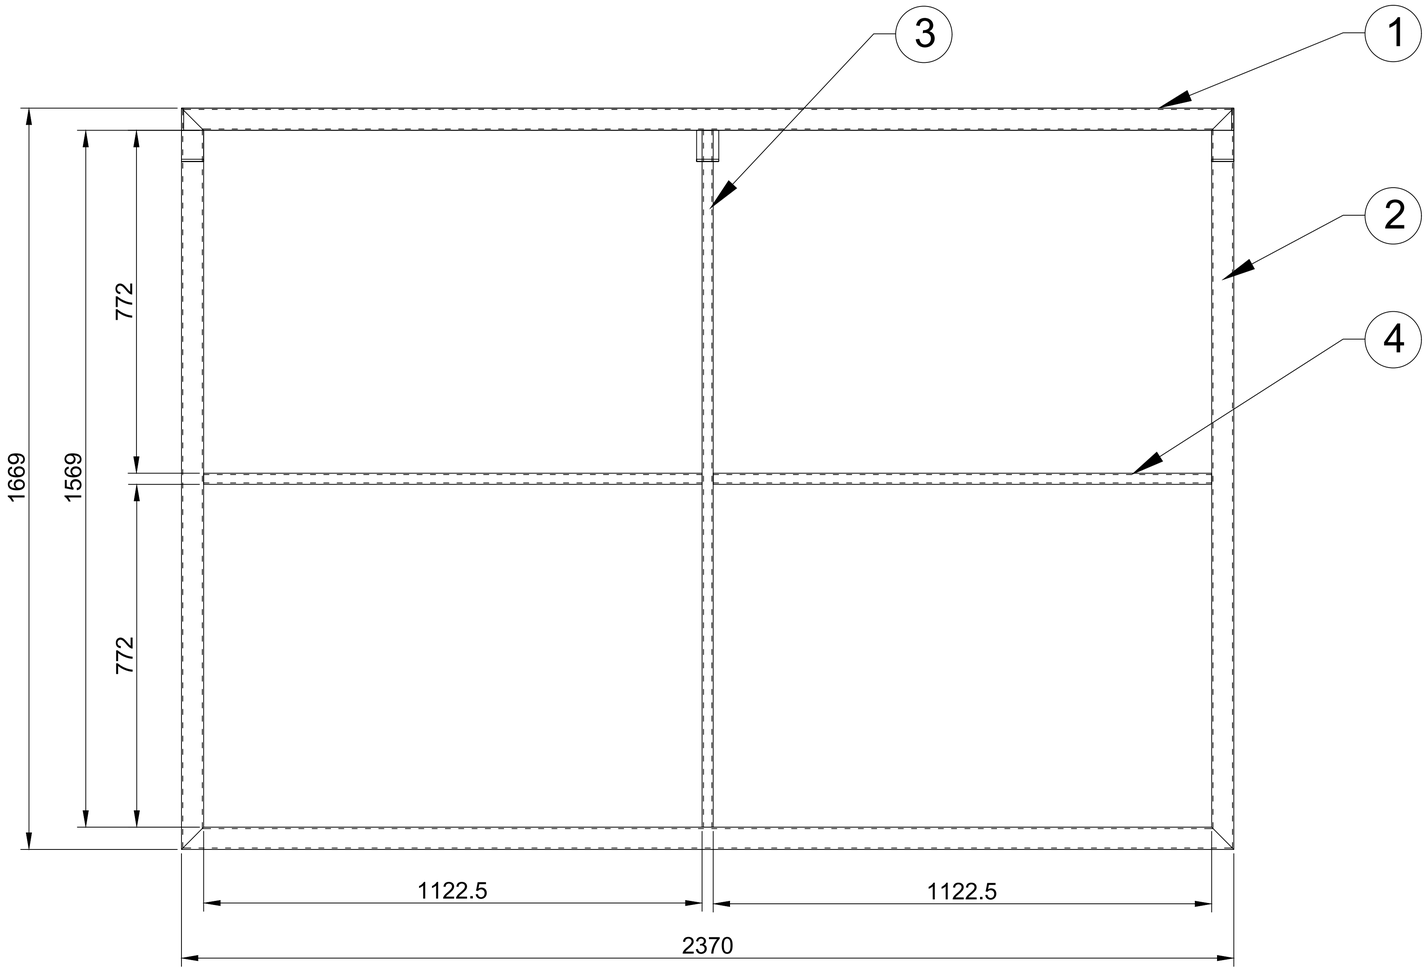

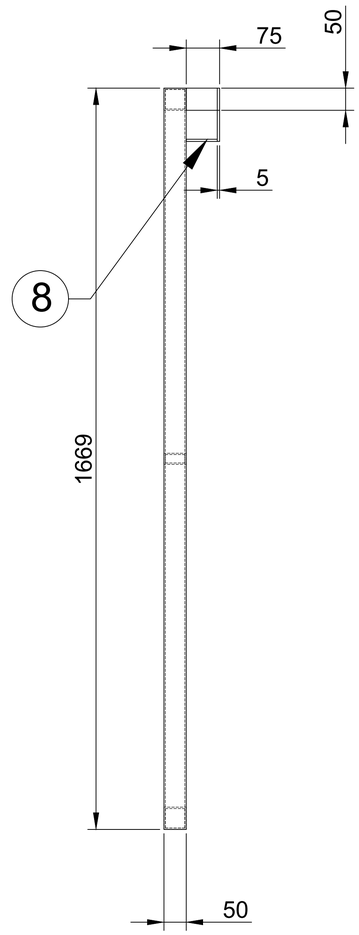

BOM FOR 1 LEAF				
SL NO.	DESCRIPTION	SPECIFICATION	QTY	WEIGHT
1	MS SQ. TUBE	50X50X3X2370L	2NOS	20.41
2	MS SQ. TUBE	50X50X3X1669L	2NOS	14.37
3	MS REC. TUBE	50X25X3X1569L	1NO	4.91
4	MS SQ. TUBE	50X25X3X1122.5L	2 NOS	7.02
5	M.S. FLAT	50 X 5 X 2370 L	1 NO	4.65
6	M.S. FLAT	50 X 5 X 70 L	8 NOS	1.08
	TOTAL			52.4400

Note:-

1.All Dimension are in MM

2.Kindly Mentain the given Dimensions

Rev No.	Revision	Date	Revised By

This drawing & design is the property of NIHVA TECHNOLOGIES. Not to be sold or copied to any other concern.

TITLE:- 2ND & 3RD LEAF

	NAME	DATE	SIGN
DRAWN	NIRMALA	15/04/2023	
CHECK	A.K.	15/04/2023	
APPRD.	V.T.	15/04/2023	

If any queries contact : design1@nihva.com

ALL DIMENSION ARE IN mm

NIHVA TECHNOLOGIES PVT. LTD.
NIHVA TECHNOLOGIES PVT. LTD. PUNE
Tel : 020 66304033
Email:- info@nihva.com
Website:- www.nihva.com

CLIENT - Cloos India Welding Technology Pvt. Ltd

LOCATION -

PRODUCT - TELESCOPIC SLIDING GATE | QTY- 8

DWG NO:- NIHVA/23-24/MFG /0121 | REV-00

SCALE: NTS | SCALE:-- 1:1 | SHEET: 01 OF 01