

RETRACTABLE ROOF

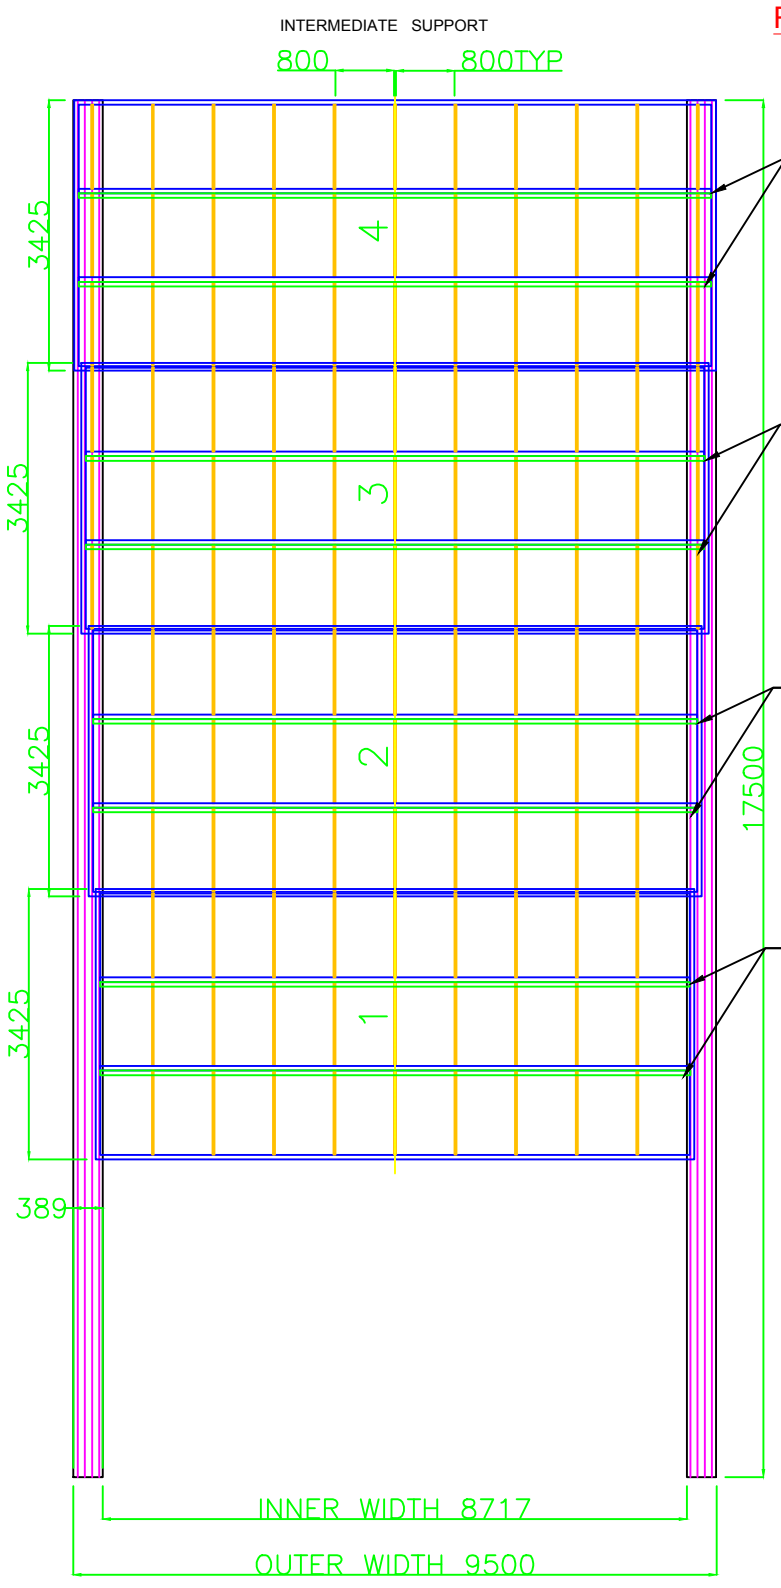

ENCLOSED PLAN

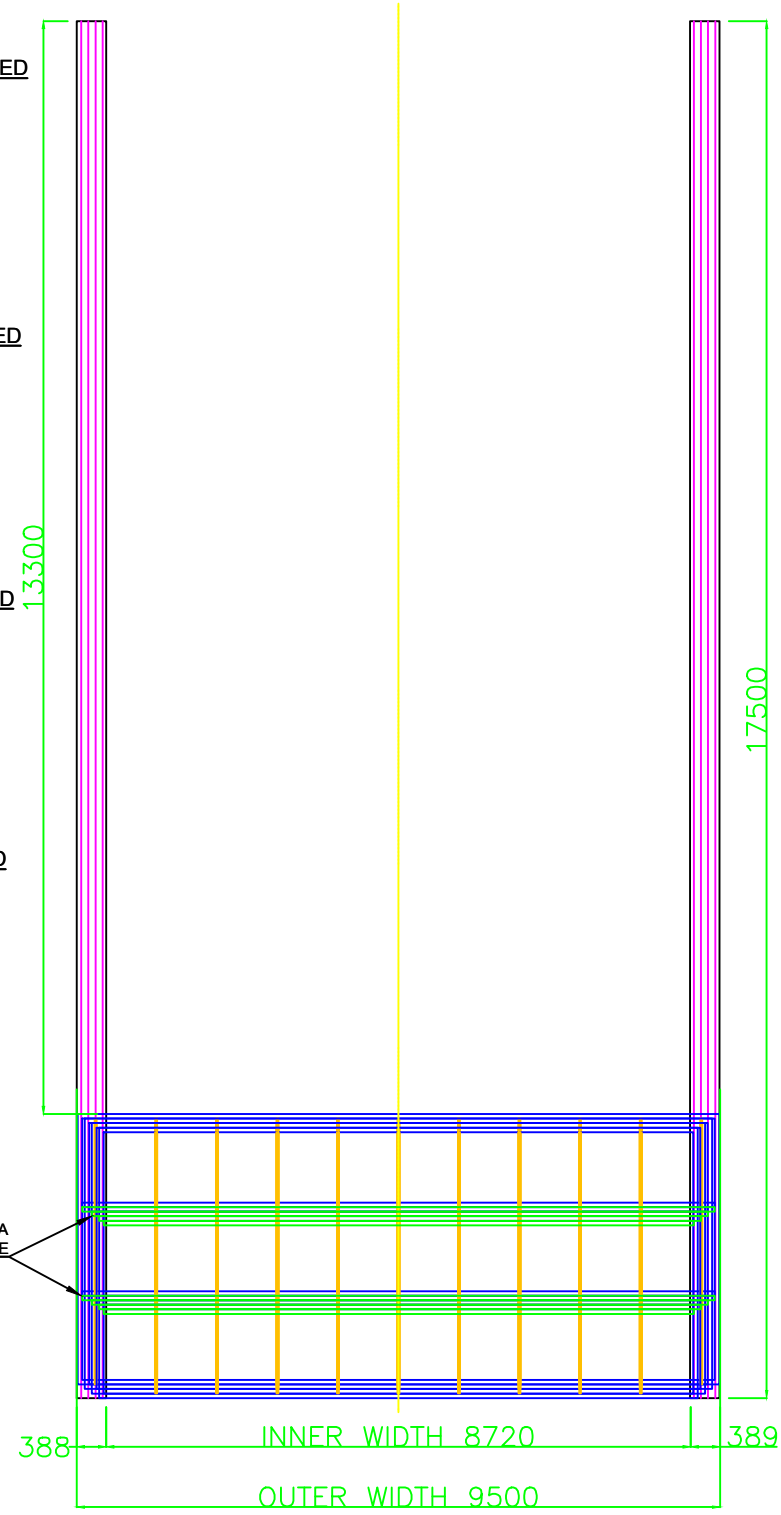

STACKED PLAN

REV.	DESCRIPTION.	REVISED BY	SIGN	DATE
002	REVISED GA DRAWING PER SINGLE SIDE OUT OF CLEAR OPENING	MAHESH S.		23.03.23
001	REVISED GA DRAWING PER BI-PARTING WITHIN CLEAR OPENING	MAHESH S.		23.03.23
000	RELEASED GA DWG FOR APPROVAL	GAURAV J.		23.03.23

This drawing & design is the property of NIHVA TECHNOLOGIES. Not to be sold or copied to any other concern.

TITLE: ROOF LAYOUT	NAME	SIGN	DATE	
DRAWN	MAHESH S.		23.03.23	CLIENT - MR. PRANAV
CHECK	MAHESH S.		23.03.23	LOCATION - NOIDA_IN
APPRD.	VIJAY T.		23.03.23	PRODUCT - RETRACTABLE ROOF
If any queries contact : projectsautomation@nihva.com				NIHVA\22-23\02XX — REV- 0
ALL DIMENSION ARE IN mm				SCALE: NTS — SHEET: 01 OF 01