


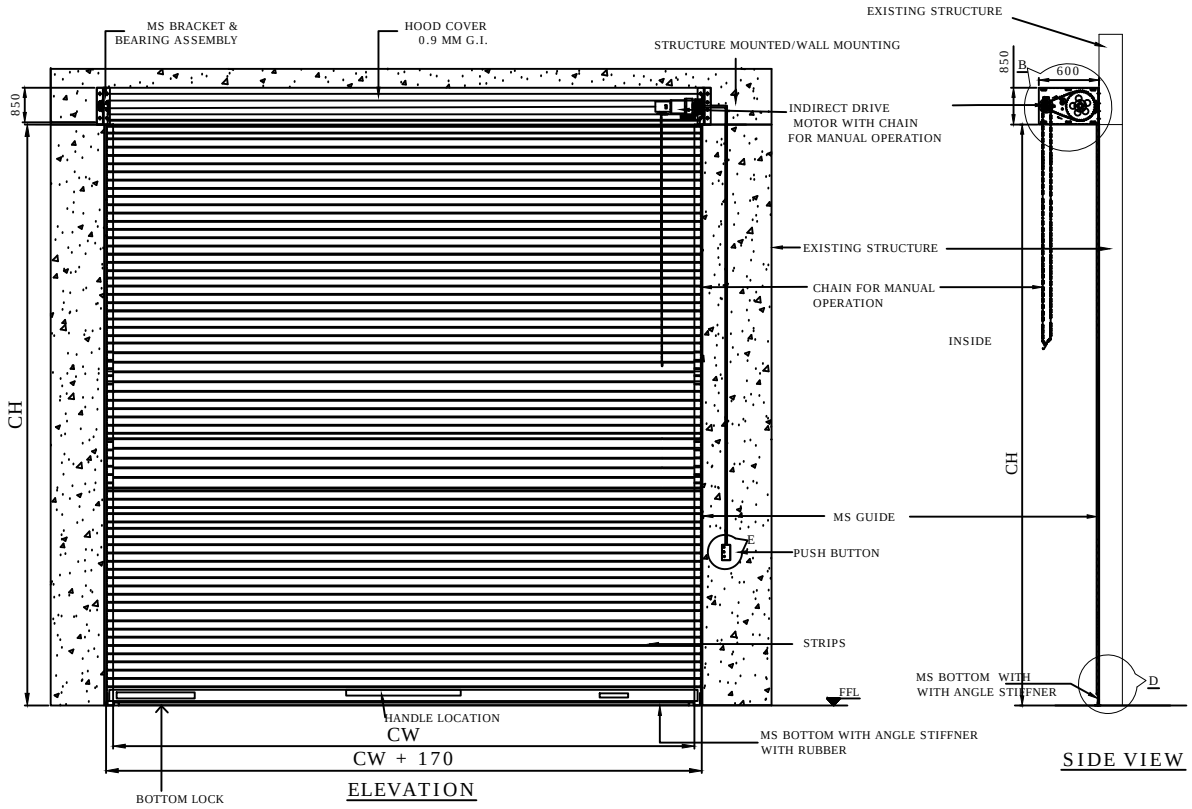


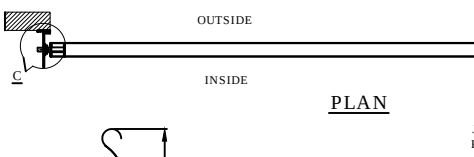


PLAN

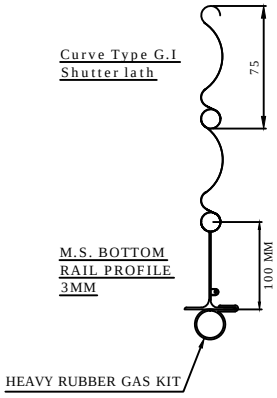

DETAILS : D

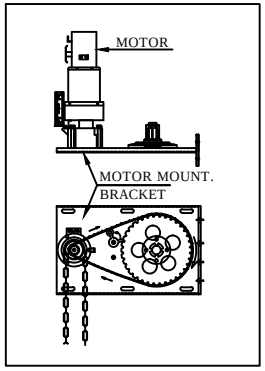


DETAILS : A & B

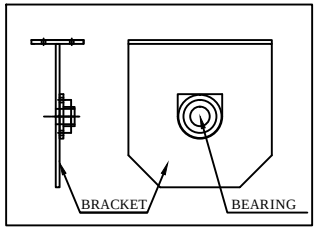

DETAILS : C

NOTE:
(1) IF REQUIRED M.S.TECHNICAL STRUCTURE & FITTING IN CLIENT SCOPE.
(2) ALL CIVIL WORK IN CLIENT SCOPE.
(3) SHUTTER WILL BE ONLY INSTALLED AFTER STRUCTURE READY AS PER DRAWING PROVIDED IF REQUIRED .
(4) PLEASE REFER FOLLOWING TABLE & MENTION YOUR REQUIREMNT IN TABLE.

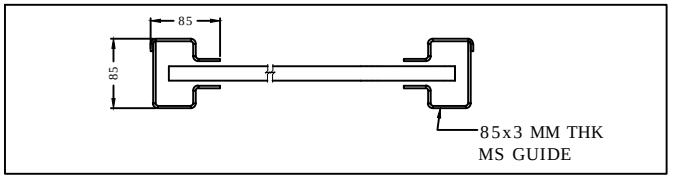

SR NO	PARAMETER	DESCRIPTION	CUSTOMER REMARK
1	SHUTTER MOUNTING	ON STRUCTURE / ON CONCRETE	
2	SURFACE FINISH	RAL CODE FOR POWDER COATING	

3400	3950	2	
CLEAR WIDTH (CW)	CLEAR HEIGHT (CH)	QUANTITY	RAL COLOR POWDER COATED

This drawing & design is the property of NIHVA TECHNOLOGIES. Not to be sold or copied to any other concern.

TITLE: MOTORIZED ROLLING SHUTTER

	NAME	SIGN	DATE
DRAWN	S.M.S.		9.11.2020
CHECK	K.P.		9.11.2020
APPRD.			

NIHVA TECHNOLOGIES PVT. LTD.
NIHVA TECHNOLOGIES PVT. LTD. PUNE
Tel : 020 66304033
Email:- info@nihva.com
Website:- www.nihva.com

CLIENT - SEZ BIOTECH SERVICES PVT LTD

PROJECT - SEZ BIOTECH SERVICES PVT LTD

SITE LOCATION - PUNE

If any queries contact : projectsupport@nihva.com

DWG. NO. : NIHVA/20-21/0082 REV- R00

ALL DIMENSION ARE IN mm | SCALE: NTS | WT: | SHEET: