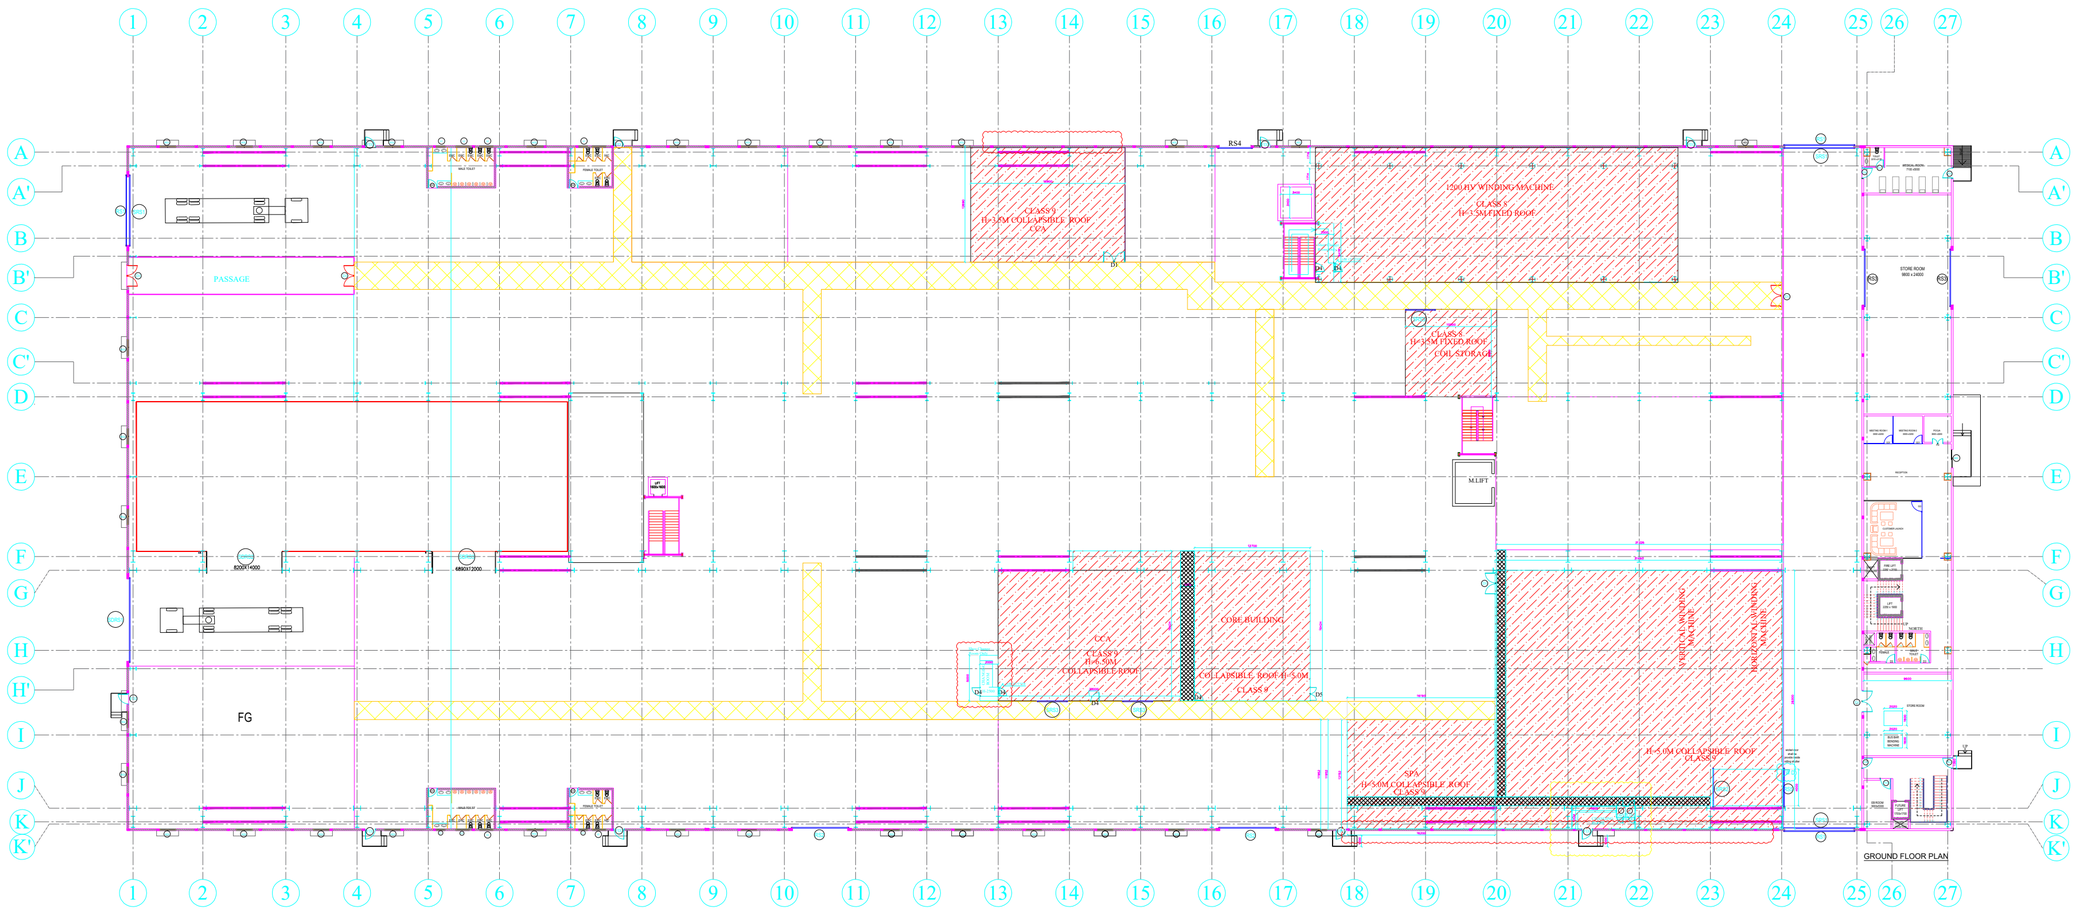


GROUND FLOOR
DOORS & WINDOW SCHEDULE:

S.No.	Doors	Size	Material	No.s
1	MD	2000x2400	Automatic Sliding Glass door	1
2	GD1	1500x2400	Glass door	2
3	GD2	1000x2400	Glass door	4
4	D1	2400x2400	Solid Double Flush door With Vison Panel	06
5	D2	900x2400	Toilet door	01
6	D3	1000x2400	Toilet door	06
7	D4	1000x2100	Solid Double Flush door With Vison Panel	08
8	D5	1500x2100	Solid Double Flush door With Vison Panel	01
9	D6	750x2100	Solid Double Flush door With Vison Panel	01
9	FD1	1000x2400	Fire rated steel Single door	02
10	FD2	1200x2400	Fire rated steel Single door	13
11	WD	900x2400	Wicket door	01

S.No.	Window	Size	Material	No.s
1	WD1	1800x1500	Aluminium Sliding window	31

S.No.	Ventilators	Size	Material	No.s
1	V1	1000x600	Aluminium Ventilator	2
2	V2	1500x600	Aluminium Ventilator	11

S.No.	Rolling shutter	Size	Material	No.s
1	SDRS1	9000x10000	Sliding Metallic rolling shutter	01
2	SDRS2	8200x14000	Sliding rolling shutter	01
3	SDRS3	6890x12000	Sliding rolling shutter	01
4	RS1	7500x8000	Metallic rolling shutter	03
5	RS2	6000x6500	Metallic rolling shutter	02
6	RS3	6000x3500	Metallic rolling shutter	02
7	RS4	3500x6500	Metallic rolling shutter	01
8	RS5	4000x5000	Metallic rolling shutter	01
9	SRS1	7500x8000	Speed rolling shutter	03
10	SRS2	4000x5000	Speed rolling shutter	01
11	SRS3	3000x3000	Speed rolling shutter	03

LEGEND

CLEAN ROOM

200MM THK. BLOCK WALL

100MM THK. BLOCK WALL

PCC

GLASS PARTITION

PLY PARTITION

PARAPET WALL

FACTORY GROUND FLOOR PLAN