
DRAWING

REV DESCRIPTION	DATE	REV NO
	28-08-2025	REV 00
1.		

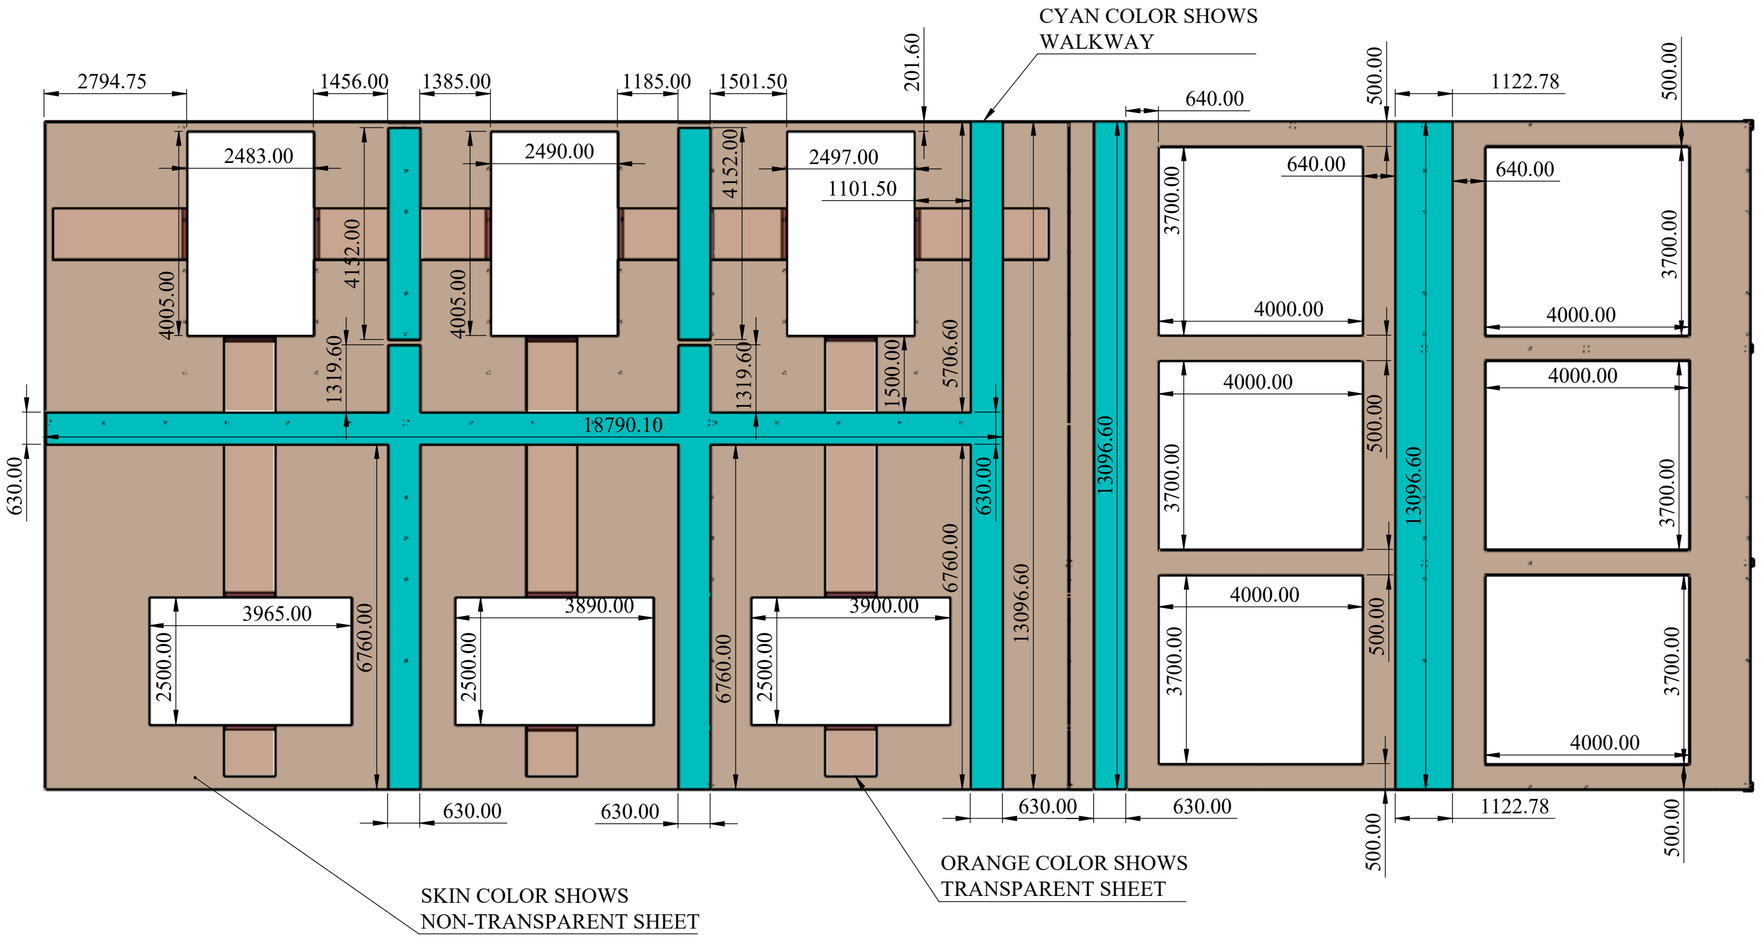

NOTE :

SPECIAL INSTRUCTION'S :

TITLE - ROOF AUTOMATION

DWG NO - NTPL-244-PM-001-00-00-00

NIHVA TECHNOLOGIES PVT.LTD.PUNE
Website - www.nihva.com

	NAME	SIGNATURE	DATE
DRAWN	V.W.		28-08-2025
CHK'D	S.P.		04-09-2025
APPV'D	V.T.		05-09-2025

PRODUCT - RETRACTABLE ROOF

PROJECT NO - NTPL-244-PM | REVISION - 00

SITE LOCATION - GUJARAT | WEIGHT -

MATRIAL - | QTY - 1

If any queries contact - Design@nihva.com

PROJECTION METHOD:


SCALE :

ALL DIMENSION ARE IN mm | A2


DRAWING


ITEM NO.	PART NUMBER	DESCRIPTION	QTY.
1	HWM UNIT WALKWAY-1 W 630X L 13096 MM LONG	MS SQ TUBE SIZE- 30X30X2.6MM THK	4
2	CHEQUERED_MS PLATE_W630 X L1306 MM LONG	MS CHEQURED PLATE SIZE- W 630 X L 1306 X 3 MM THK	4

REV DESCRIPTION	DATE	REV NO
	28-08-2025	REV 00
1.		

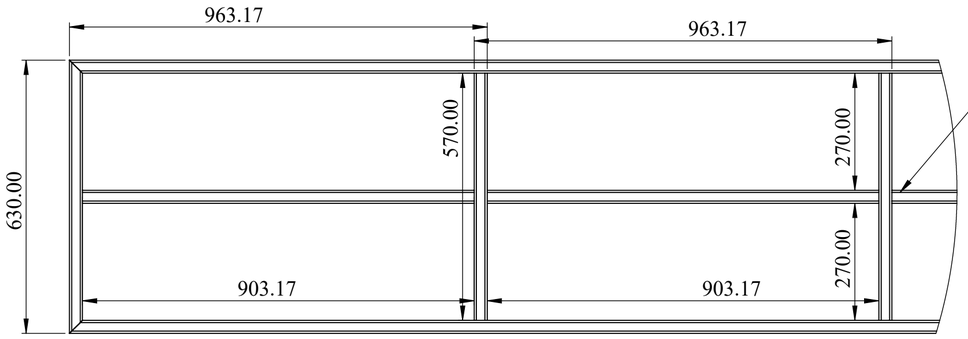

DETAIL A
SCALE 1 : 10

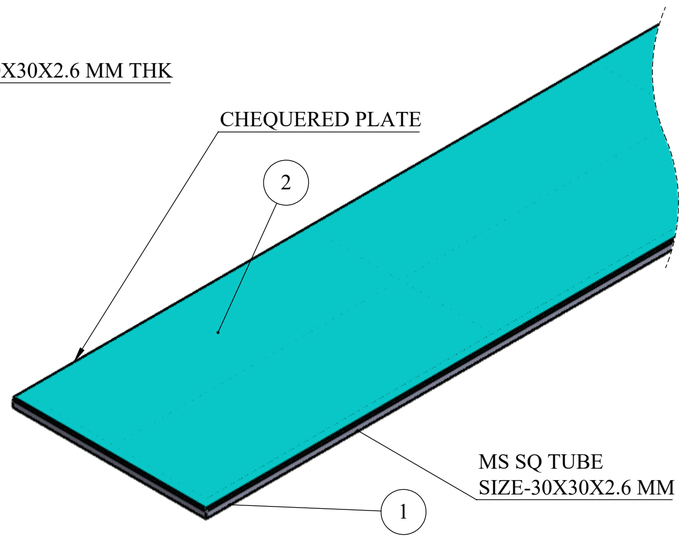

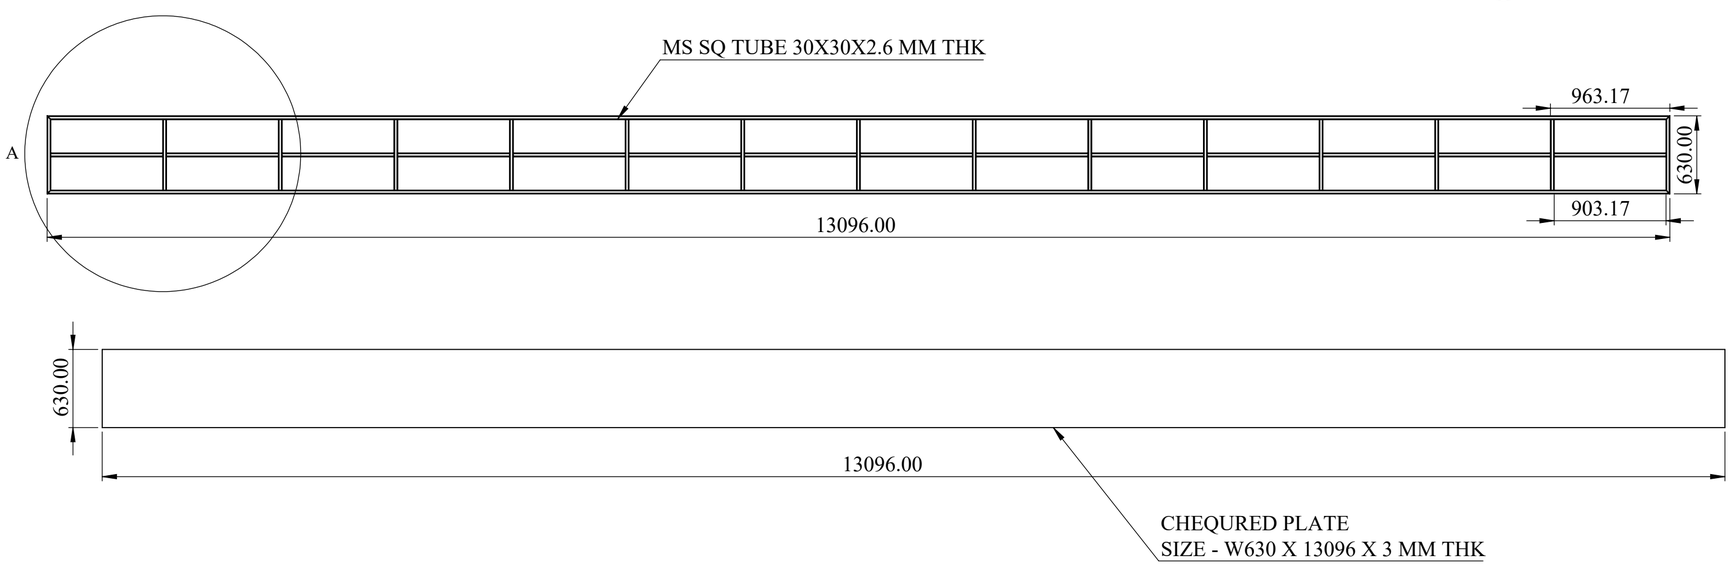

NOTE :

NAME: WALKWAY'S
SIZE : 630x13096 MM LONG
MTL : MS
QTY : 04 NOS


SPECIAL INSTRUCTION'S :

TITLE - ROOF AUTOMATION			
DWG NO - NTPL-244-PM-001-00-00-00			
NIHVA Technologies Pvt. Ltd.	NIHVA TECHNOLOGIES PVT.LTD.PUNE Website - www.nihva.com		
	NAME	SIGNATURE	DATE
DRAWN	V.W.		28-08-2025
CHK'D	S.P.		04-09-2025
APPV'D	V.T.		05-09-2025
PRODUCT - RETRACTABLE ROOF			
PROJECT NO - NTPL-244-PM	REVISION - 00		
SITE LOCATION - GUJARAT	WEIGHT -		
MATRIAL -	QTY - 1		
If any queries contact - Design@nihva.com			
ALL DIMENSION ARE IN mm	A2	PROJECTION METHOD:	SCALE :
			SHEET 2 OF 4


DRAWING

REV DESCRIPTION	DATE	REV NO
	28-08-2025	REV 00
1.		

ITEM NO.	PART NUMBER	DESCRIPTION	QTY.
1	HWM UNIT WALKWAY-2_W 1122 X L 13096 MM LONG	MS SQ TUBE 30X30X2.6 MM THK	1
2	CHEQUERED_MS PLATE_W1122 X L13096 X 3 MM THK-13096 MM LONG	MS CHEQUERED PLATE W1122XL13096X3 MM THK	1

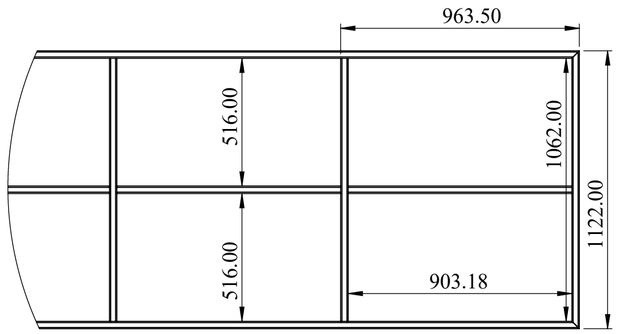

DETAIL B
SCALE 2 : 35

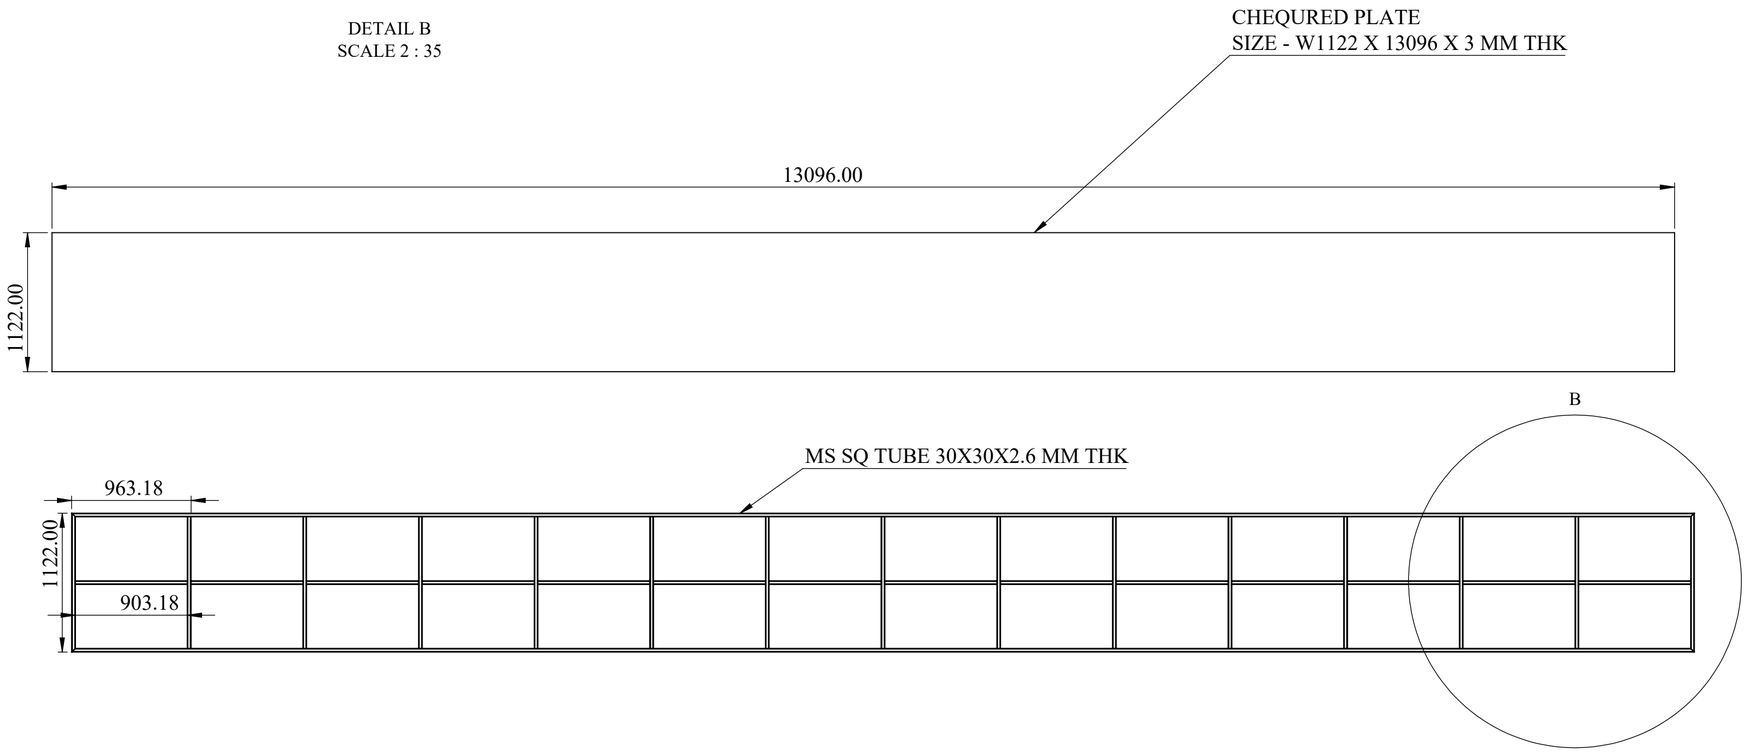

NOTE :

NAME: WALKWAY'S
SIZE : 1122 x13096 MM LONG
MTL : MS
QTY : 01 NOS

SPECIAL INSTRUCTION'S :

TITLE - ROOF AUTOMATION

DWG NO - NTPL-244-PM-001-00-00-00

NIHVA Technologies Pvt. Ltd.

NIHVA TECHNOLOGIES PVT.LTD.PUNE
Website - www.nihva.com

	NAME	SIGNATURE	DATE
DRAWN	V.W.		28-08-2025
CHK'D	S.P.		04-09-2025
APPV'D	V.T.		05-09-2025


PRODUCT - RETRACTABLE ROOF
PROJECT NO - NTPL-244-PM
REVISION - 00
SITE LOCATION - GUJARAT
WEIGHT -
MATRIAL -
QTY - 1
PROJECTION METHOD:
SCALE :
SHEET 3 OF 4

If any queries contact - Design@nihva.com
ALL DIMENSION ARE IN mm
A2


DRAWING


ITEM NO.	PART NUMBER	DESCRIPTION	QTY.
1	HWM UNIT WALKWAY-3 W 630X L 18790 MM LONG	MS SQ TUBE 30X30X2.6 MM THK	1
2	CHEQUERED_MS PLATE_W630 X L18790 X 3MM THK	MS CHEQURED PLATE - W630 X L 18790 X 3 MM THK	1

REV DESCRIPTION	DATE	REV NO
	28-08-2025	REV 00
1.		

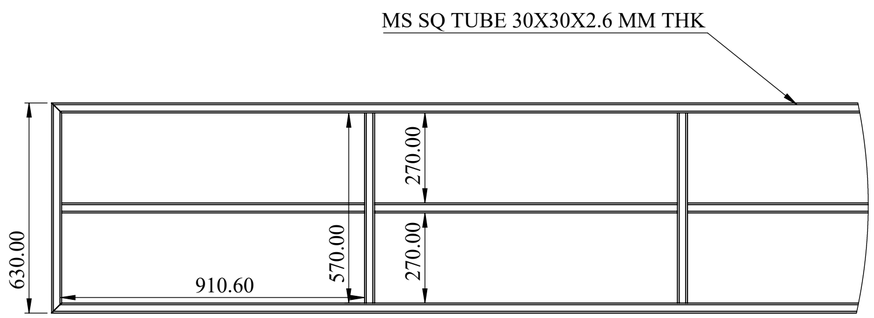

DETAIL C
SCALE 1 : 13

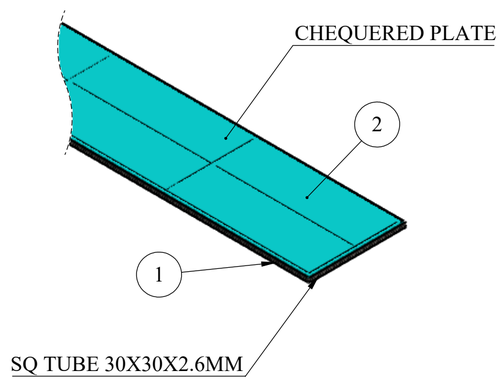

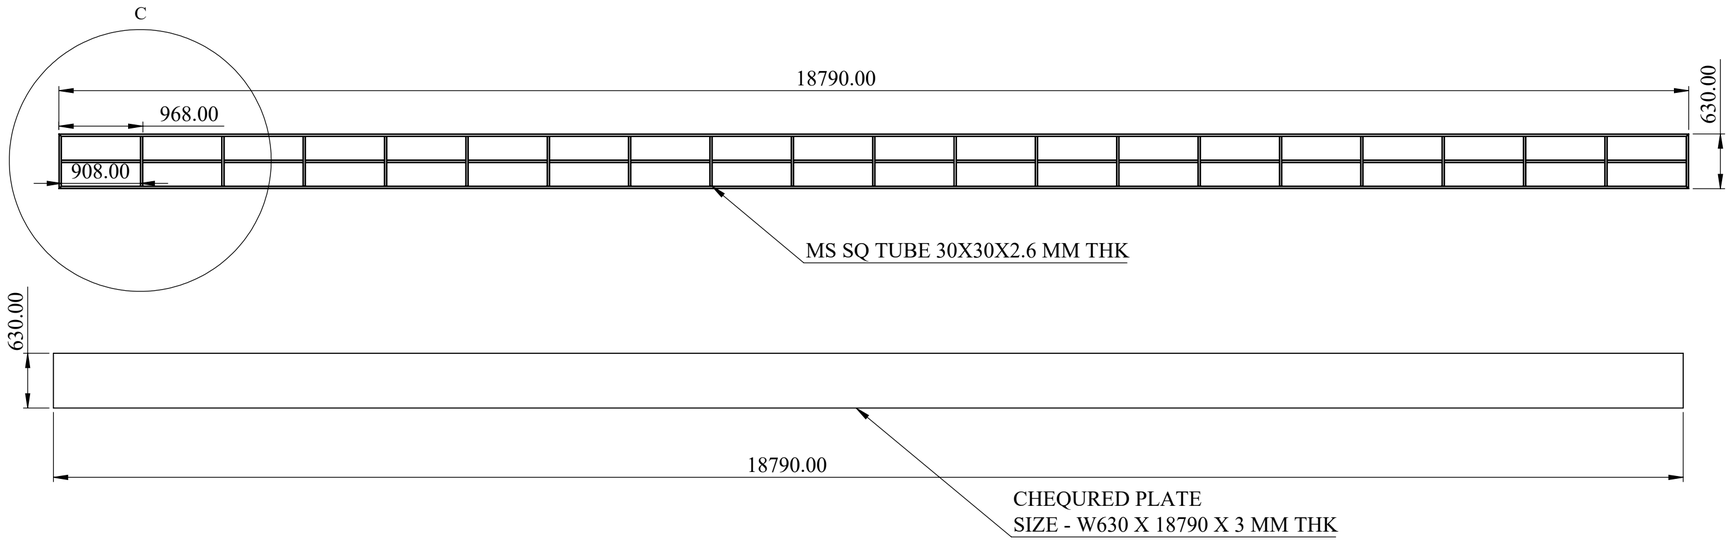

NOTE :

NAME: WALKWAY'S
SIZE : 630 x18790 MM LONG
MTL : MS
QTY : 01 NOS

SPECIAL INSTRUCTION'S :

TITLE - ROOF AUTOMATION

DWG NO - NTPL-244-PM-001-00-00-00

NIHVA TECHNOLOGIES PVT.LTD.PUNE
Website - www.nihva.com

	NAME	SIGNATURE	DATE
DRAWN	V.W.		28-08-2025
CHK'D	S.P.		04-09-2025
APPV'D	V.T.		05-09-2025

PRODUCT - RETRACTABLE ROOF
PROJECT NO - NTPL-244-PM
REVISION - 00
SITE LOCATION - GUJARAT
WEIGHT -
MATRIAL -
QTY - 1
If any queries contact - Design@nihva.com
PROJECTION METHOD:
SCALE :
ALL DIMENSION ARE IN mm
A2
SHEET 4 OF 4