


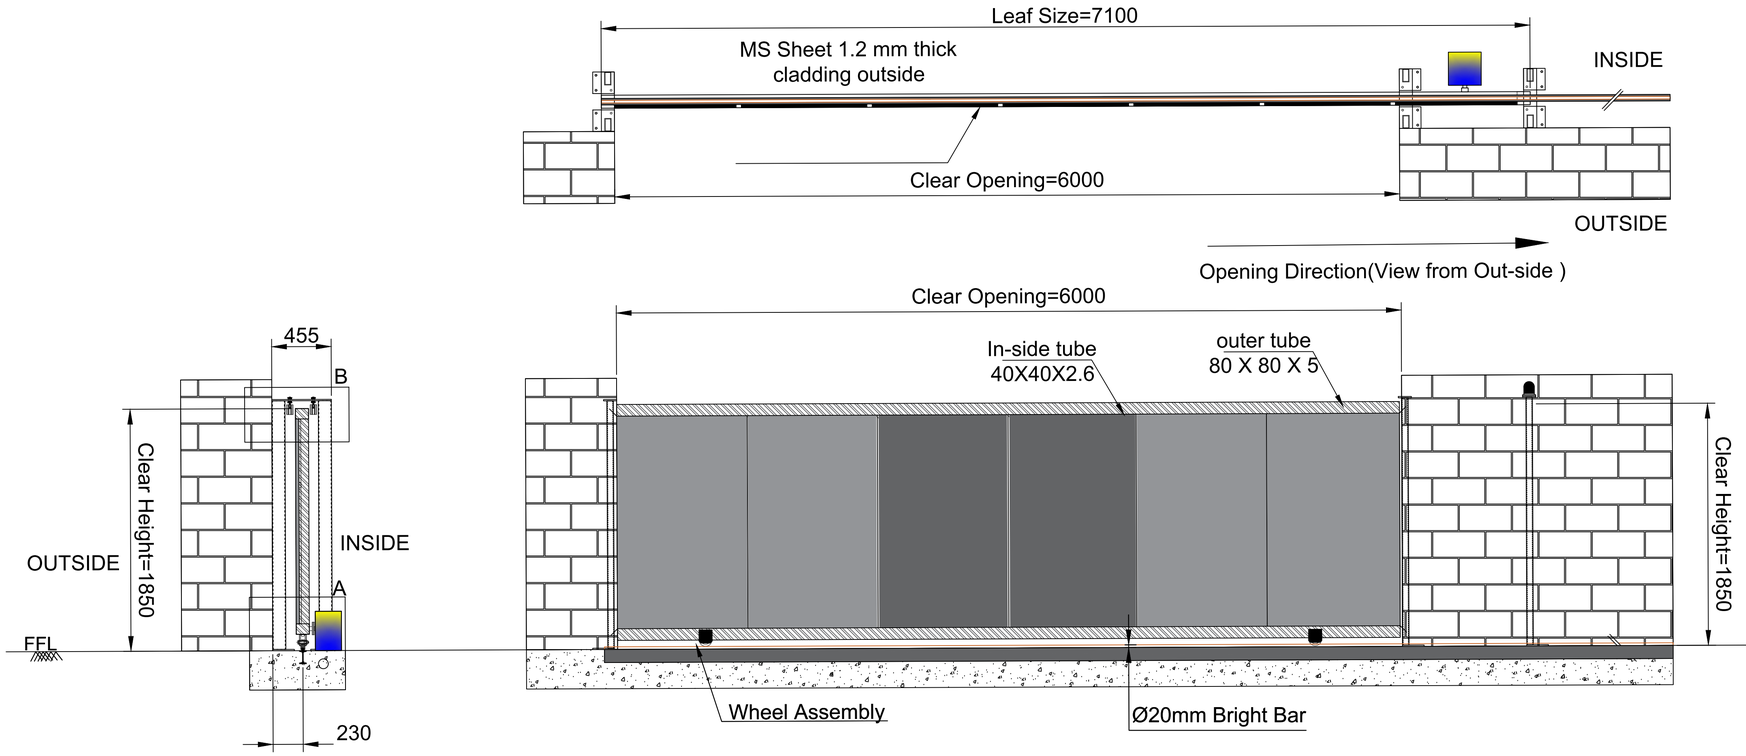


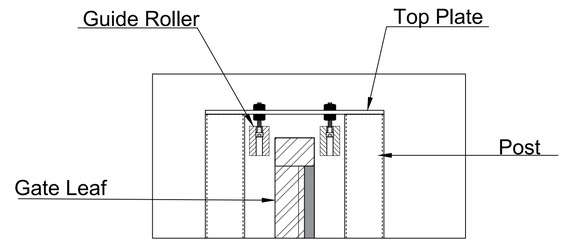


Detail:B

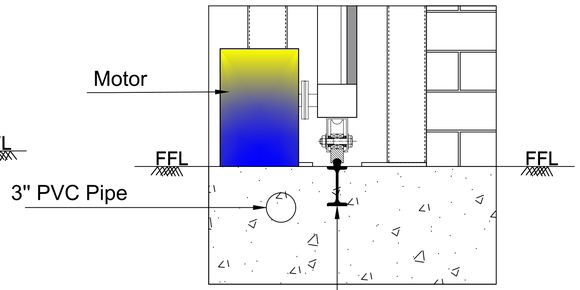

Detail:A

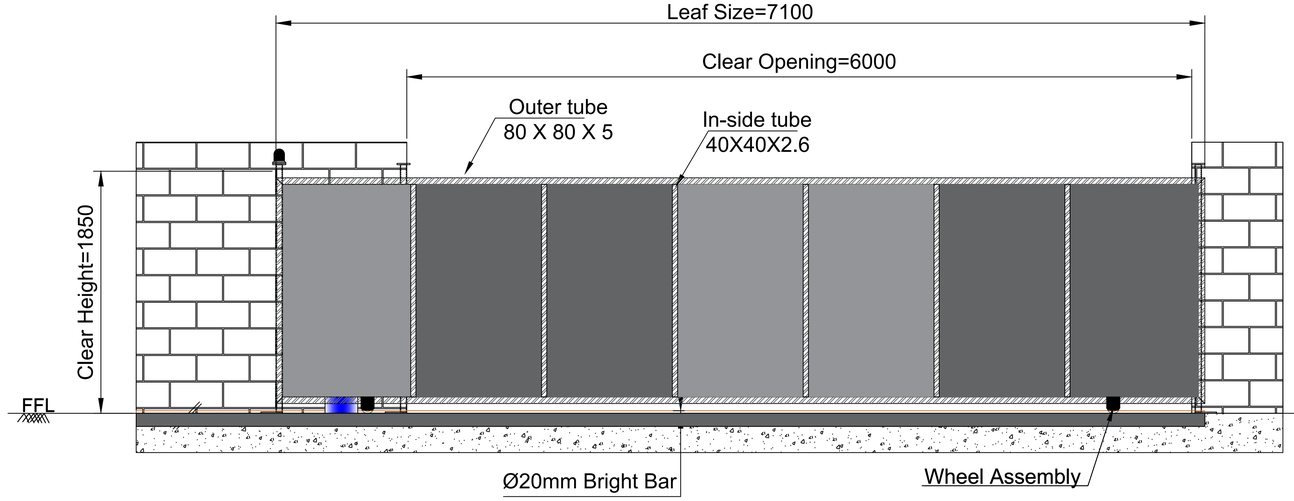

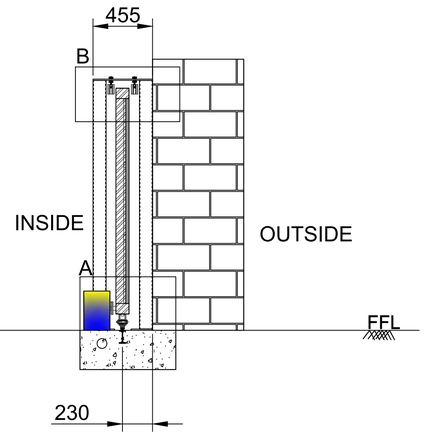

Note:-

1.All Dimension are in MM.
2.Required all civil work is in Client Scope.
3.Installation and Fabrication tolerance will be ±20mm
4.Required Parking will be 7300
5. Coating : Approved RAL 9002

Opening Direction(View from inside)

Rev No.	Revision	Date	Revised By
3	Revision Done As Per Client need - panels on gate 7 nos instead of 6 nos.	30/07/2022	Mahesh S.
2	Revision Done As Per Client need - panels on gate 6 nos instead of 7 nos.	28/07/2022	Mahesh S.
1	Revision Done As Per Client Requirements	23/07/2022	Sujata

This drawing & design is the property of NIHVA TECHNOLOGIES. Not to be sold or copied to any other concern.

TITLE:-MOTORISED SLIDING GATE

NIHVA TECHNOLOGIES PVT. LTD.
NIHVA TECHNOLOGIES PVT. PUNE
Tel : 020 66304033
Email:- info@nihva.com
Website:- www.nihva.com

	NAME	DATE	SIGN
DRAWN	MAHESH S.	18-07-2022	
CHECK	MAHESH S.	18-07-2022	
APPRD.	A.KURHADE	18-07-2022	

If any queries contact : design@nihva.com

ALL DIMENSION ARE IN mm

CLIENT - S.S.GHORPADE CONSTRUCTIONS PVT. LTD.

LOCATION -

PRODUCT - MOTORISED SLIDING GATE

DWG NO:- NIHVA/22-23/CLT/0081 REV- 0

SCALE: NTS SCALE:-- 1:1 SHEET: 01 OF 01