


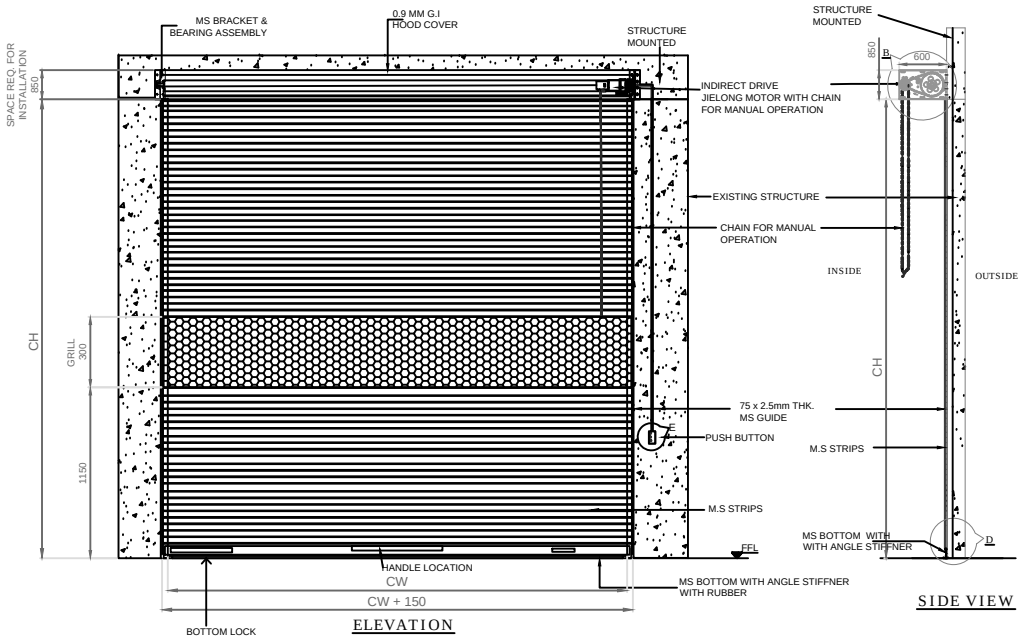


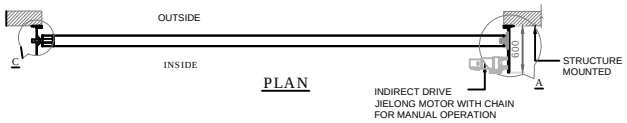



PLAN

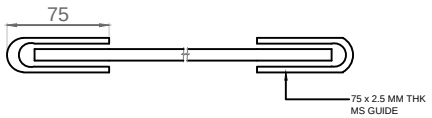

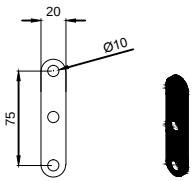


5 m m THK. LINK

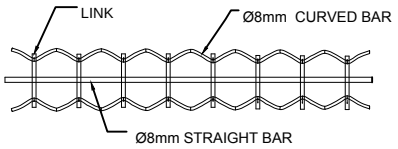


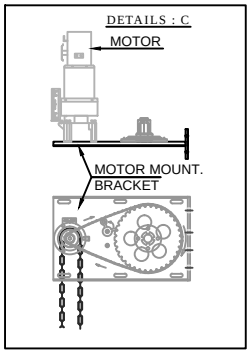

DETAILS : A & B

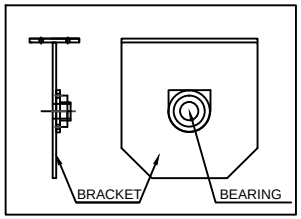

DETAILS : C

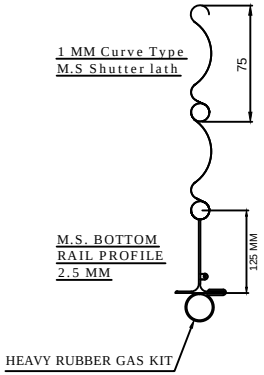

DETAILS : D

2500	2000	2
CLEAR WIDTH (CW)	CLEAR HEIGHT (CH)	QUANTITY

NOTE:
1. REQUIRED TECHNICAL M.S STRUCTURE FOR SHUTTER IN CLIENT SCOPE.
2. POWDER COATING.

This drawing & design is the property of NIHVA TECHNOLOGIES. Not to be sold or copied to any other concern.

TITLE	MOTORIZED ROLLING SHUTTER			NIHVA TECHNOLOGIES PVT. LTD.
	NAME	SIGN	DATE	
DRAWN	P.A		20.07.2020	CLIENT -
CHECK	G.J		20.07.2020	PROJECT -
APPRD.				SITE LOCATION -
If any queries contact : design@nihva.com				DWG. NO. : NIHVA/20-21/VDR/0043 REV- R00
ALL DIMENSION ARE IN mm				SCALE: NTS WT: SHEET:

NIHVA TECHNOLOGIES PVT. LTD. PUNE
Tel : 020 66304033
Email:- info@nihva.com
Website:- www.nihva.com