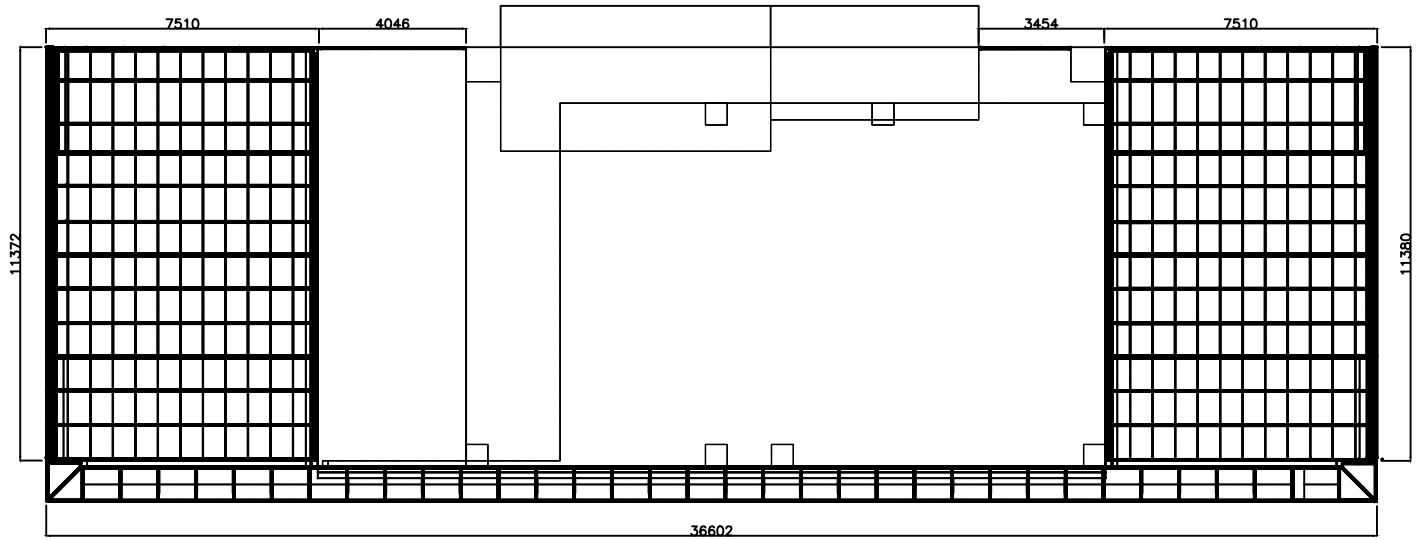

ENCLOSED PLAN

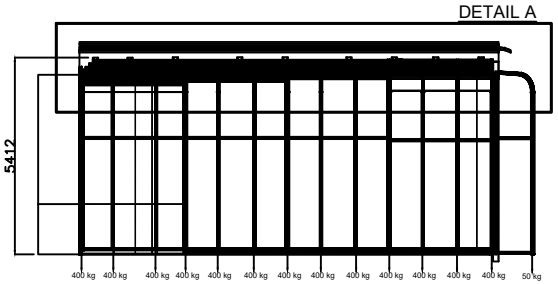

SIDE VIEW

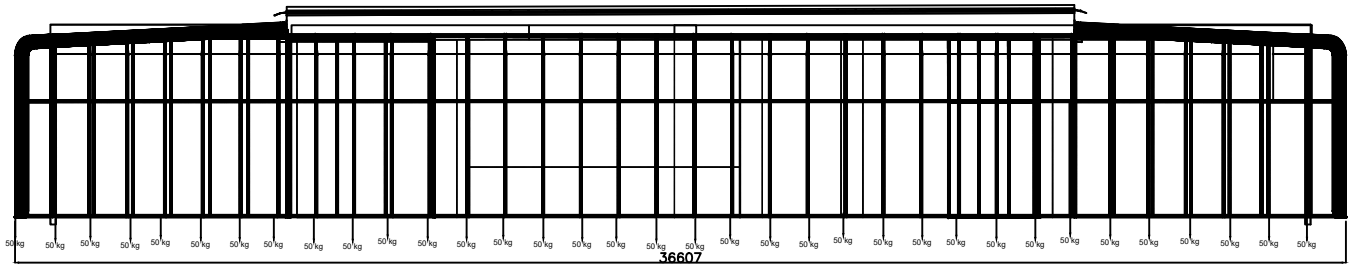

FRONT VIEW

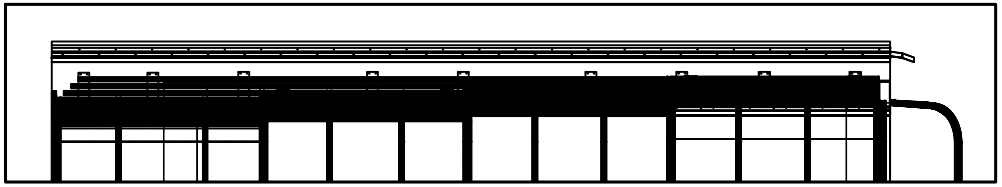

DETAIL A
ENLARGED VIEW
FIXING DETAILS

PITCH - 1000 MM

TITLE:- FRAME ASSEMBLY			
	NAME	DATE	SIGN
DRAWN	KISHAN	11/08/22	
CHECK	G. JAIN	11/08/22	
APPRD.	V. TARAK	11/08/22	

NIHVA TECHNOLOGIES PVT. LTD.

NIHVA TECHNOLOGIES PVT. LTD. PUNE
Tel : 020 66304033
Email:- info@nihva.com
Website:- www.nihva.com

CLIENT - 24K KRAFT BREWZZ		
LOCATION - PAVILION MALL		
PRODUCT: RETRACTABLE ROOF		
If any queries contact : design@nihva.com	DWG NO:-NIHVA/22-23/MFG/0048	REV- 0
ALL DIMENSION ARE IN mm	SCALE: NTS SCALE:-- 1:1	SHEET: 01 OF 01