


230 V & 50 Hz
Single phase supply
Required near left side
of Operator.

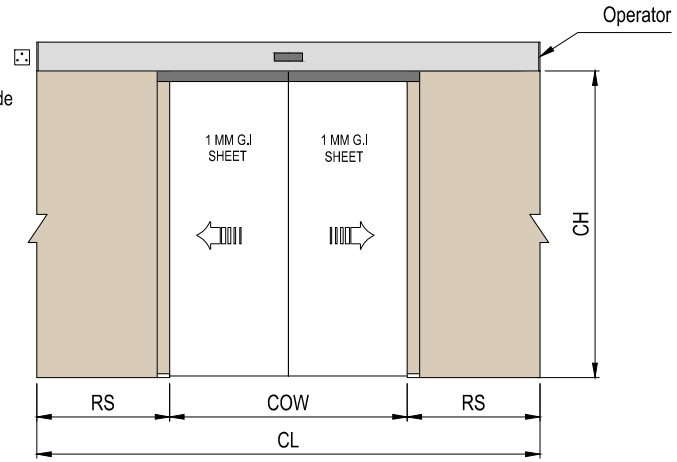


Inside Elevation

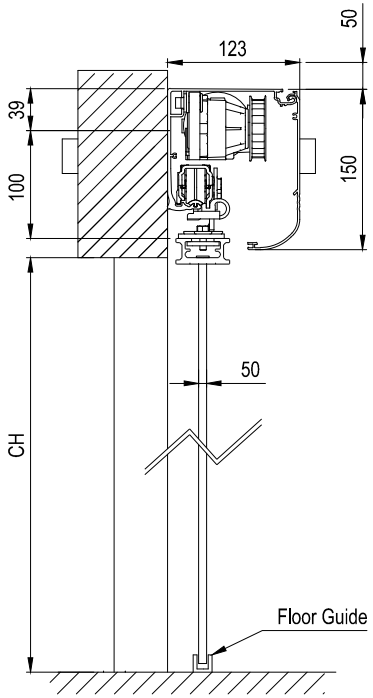

Fixing Plan

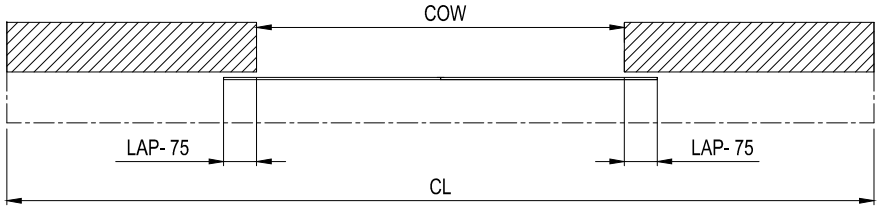

Closed Condition

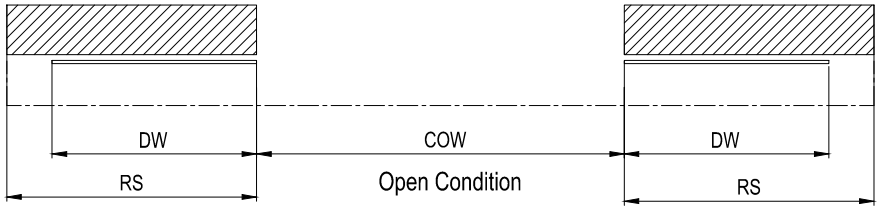

Open Condition

Plan

1	1200	2400	2750	1275	775	1
Sr. No.	(COW) CLEAR OPEN WIDTH	(CH) CLEAR HEIGHT	(CL) CLEAR LENGTH	(DW) DOOR WIDTH	(RS) REQ. SPACE	QTY

This drawing & designing is the property of NIHVA TECHNOLOGIES. Not to be sold or copied to any other concern.

TITLE: AUTOMATIC METAL SLIDING DOOR SL 500-ACCESS CONTROL

NIHVA TECHNOLOGIES PVT. LTD. PUNE
Tel : 020 66304033
Email:- info@nihva.com
Website:- www.nihva.com

	NAME	SIGN	DATE
DRAWN	PRADEEP		21.08.2018
CHECK	VIKRANT		21.08.2018
APPROVAL	R.D		21.08.2018
REV.	00		

CLIENT - DEVI CONSTRUCTION
PROJECT -
SITE - PUNE
DWG. NO. : NIHVA/18-19/0106
If any queries contact : design@nihva.com
SCALE: NTS | WT: | SHEET: 01 OF 01
ALL DIMENSION ARE IN mm