


PRODUCED BY AN AUTODESK EDUCATIONAL PRODUCT

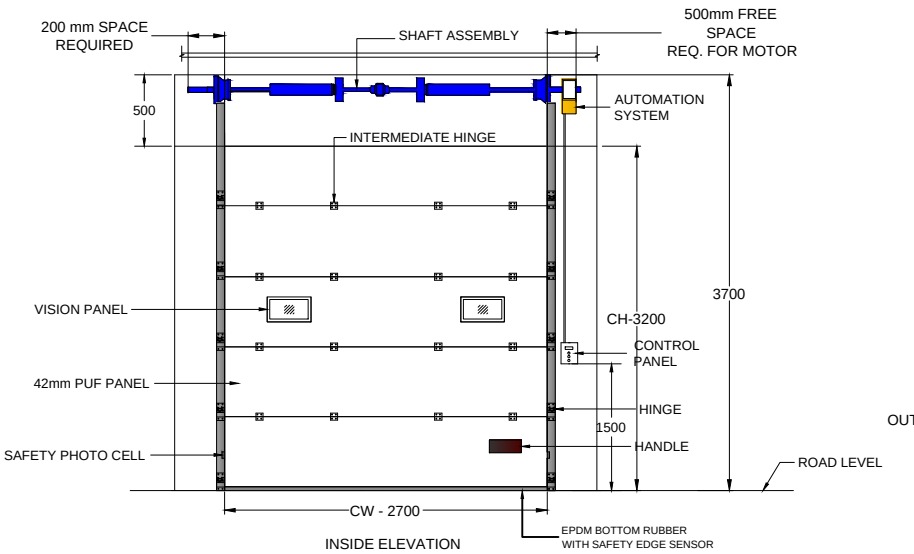


INSIDE ELEVATION

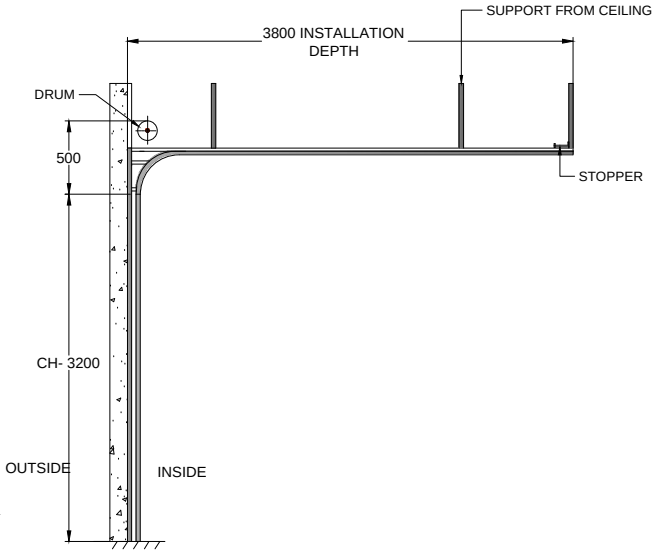

SIDE VIEW

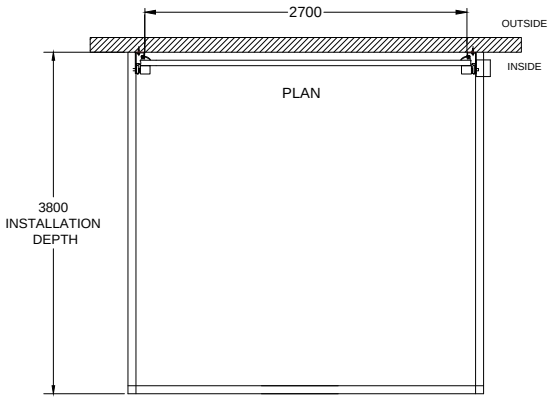

PLAN

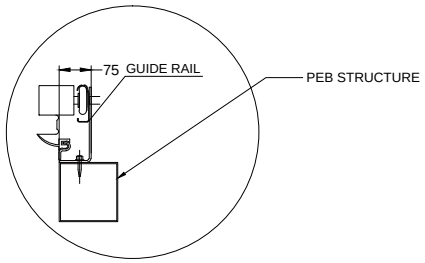

TRACK DETAILS

DIMENSION :

CLEAR WIDTH	CLEAR HEIGHT	QUANTITY
2700 mm	3200 mm	2

TECHNICAL DATA :

COMPONENTS	MATERIALS	SPECIFICATIONS
DOOR PANELS	GI & PUF	42mm CFC- FREE POLYURETHANE WITH 0.5mm THK, GI PRECOATED PANELS.
DOOR HINGE	———	HEAVY DUTY HINGES FOR INTERLOCKING OF PANELS
SHAFT ASSEMBLY	STD.	TORSIONAL SPRING WITH SHAFT & BEARING PLATES
FINISH		WHITE RAL 9002

ACCESSORIES-

IMPORTANT NOTES:

1.SINGLE PHASE POWER SUPPLY REQUIRED AT DOOR LOCATION.
2.ALL CIVIL WORK SHALL BE CLIENT'S SCOPE.

NIHVA TECHNOLOGIES PVT. LTD. PUNE
Email:- info@nihva.com
Website:- www.nihva.com

TITLE:

SECTIONAL DOOR SL (MOTORIZED)

CLIENT'S APPROVAL :

CLIENT - FERRERO INDIA PVT. LTD.

PROJECT -

SITE LOCATION - BARAMATI

DWG. NO. : NIHVA/17-18/0291 | REV- 0

SCALE: NTS | WT: | SHEET:1 OF 1

DRAWN BY: OMKAR | DATE: 22-11-2017

CHECK BY: SHEKHAR | DATE: 22-11-2017

APPROVED BY : SHEKHAR | DATE: 22-11-2017

If any queries contact : projects@nihva.com

NOTE: ALL DIMENSIONS ARE IN mm

PRODUCED BY AN AUTODESK EDUCATIONAL PRODUCT
PRODUCED BY AN AUTODESK EDUCATIONAL PRODUCT
PRODUCED BY AN AUTODESK EDUCATIONAL PRODUCT