
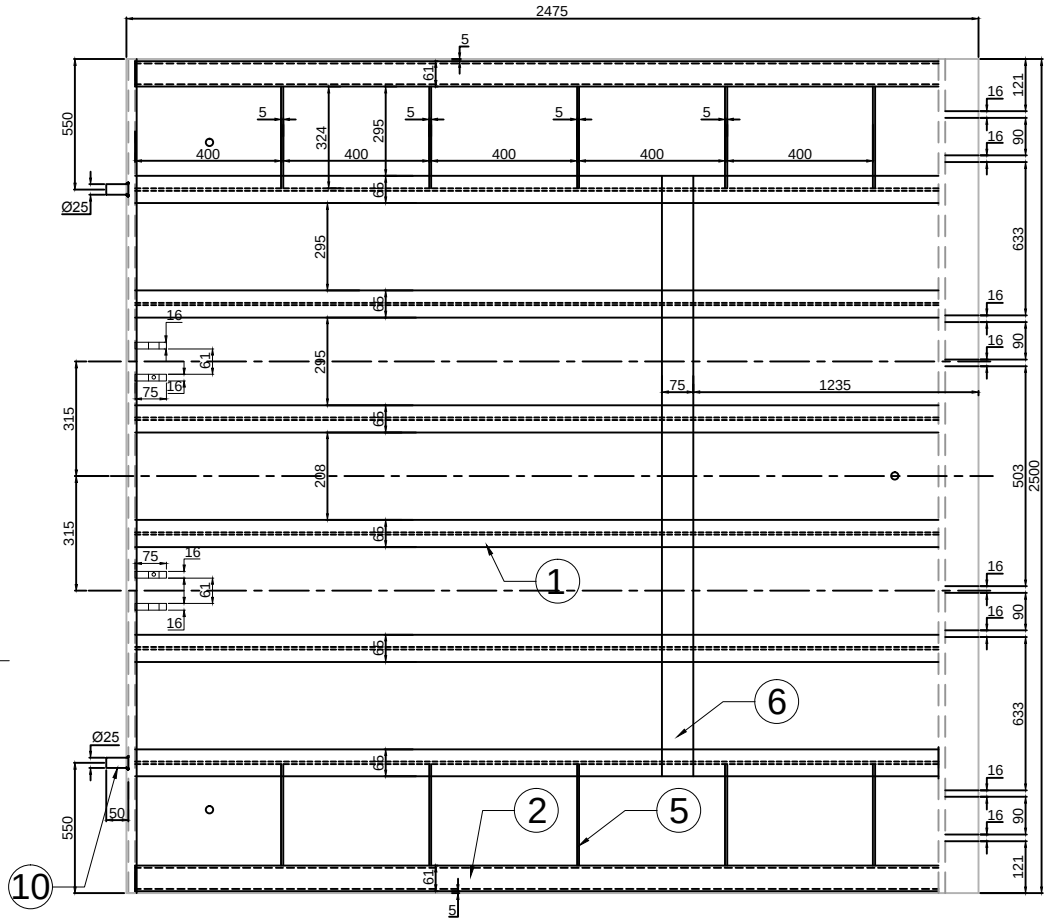


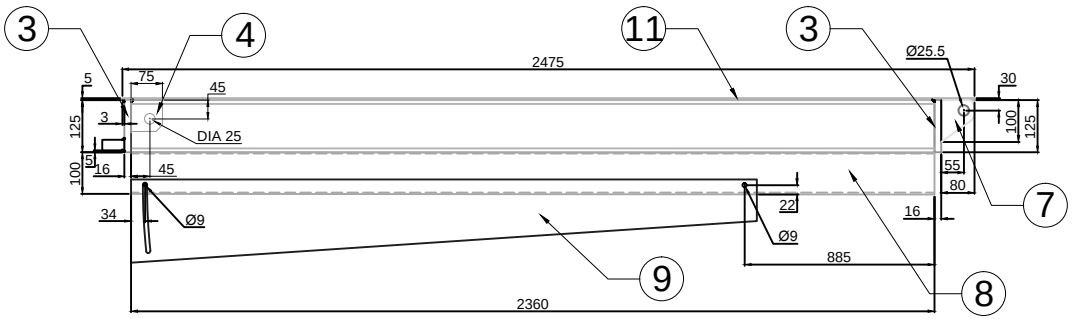

NOTE:~ MTL : MS

PART NO.	PART NAME	DESCRIPTION	QTY
1.	ISMB	125 X 65 X 2360L	6 NOS
2.	R.TUBE	122 X 61 X 4.8THK X 2360L	2 NOS
3.	FLAT	125 X 16 X 2500L	2 NOS
4.	FLAT	75 X 16 X 75L	4 NOS
5.	FLAT	125 X 6 X 324L	10 NOS
6.	FLAT	75 X 6 X 1775L	1 NO
7.	FLAT	100 X 16 X 80L	10 NOS
8.	BEND	100 X 3THK X 2360L	2 NOS
9.	SIDE COVER	200 X 3THK X 1500L	2 NOS
10.	LIP STOPER	Ø25 X 53L	4 NOS
11.	CHEQ.SHEET	2500 X 5 THK X 2475L	1 NO
12.	EYE BOLT	M16 X STD WITH NUT	3 NOS

This drawing & design is the property of NIHVA TECHNOLOGIES. Not to be sold or copied to any other concern.

TITLE

DECK ASSLY

	NAME	SIGN	DATE
DRAWN	PRADEEP		23.04.2018
CHECK	PRADEEP		23.04.2018
APPRD.	PRADEEP		23.04.2018

If any queries contact : design@nihva.com

ALL DIMENSION ARE IN mm

NIHVA TECHNOLOGIES PVT. LTD.

NIHVA TECHNOLOGIES PVT. LTD. PUNE
Tel : 020 66304033
Email:- info@nihva.com
Website:- www.nihva.com

CLIENT -

PROJECT - DLMP1004

SITE LOCATION -

DWG. NO. : NIHVA/18-19/DLMP1004_006

SCALE: NTS | WT: | REV- 00