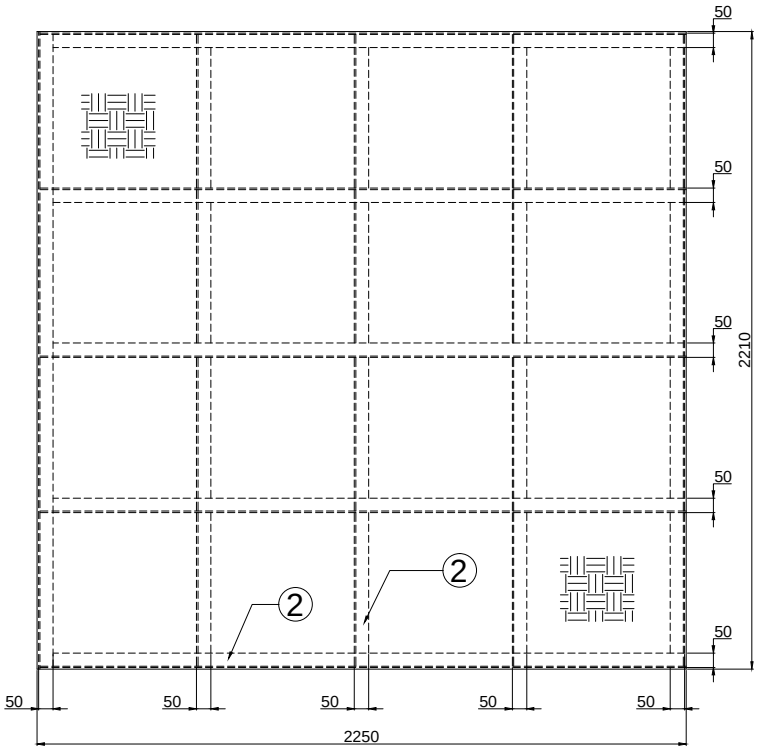

ELEVATION

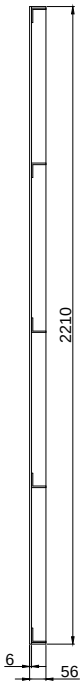

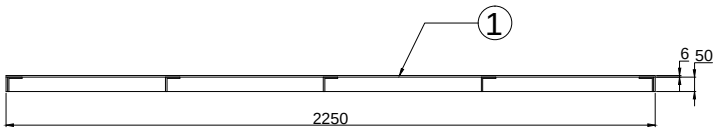

PLAN

SR NO	DESCRIPTION
1.	CHEQ. SHEET 6 MM THK
2.	ISA 50 X 50 X 5 MM THK

SIZE:

WIDTH	LENGTH	HEIGHT	QUANTITY
2210 mm	2250 mm	56 mm	07 NOS.

NIHVA TECHNOLOGIES PVT. LTD.

NIHVA TECHNOLOGY
PVT. LTD. PUNE
Email:- info@nihva.com
Website:- www.nihva.com

TITLE:

DOCK PIT ENCLOSER

CLIENT'S APPROVAL :

CLIENT - IKEA

PROJECT - IKEA

SITE LOCATION - CHAKAN PHASE III

DWG. NO. : NIHVA/18-19/0056

SCALE: NTS	WT: 300 kgs	SHEET:1 OF 1
DRAWN BY: PA		DATE: 14.06.2018
CHECK BY: SS		DATE: 14.06.2018

If any queries contact : design@nihva.com

NOTE: ALL DIMENSION ARE IN mm

THIS DRAWING & DESIGNING IS THE PROPERTY OF NIHVA TECHNOLOGIES. NOT BE SOLD OR COPY TO ANY OTHER CONCERN.