
DWG.NO: SALT_1729_STR_01_R0

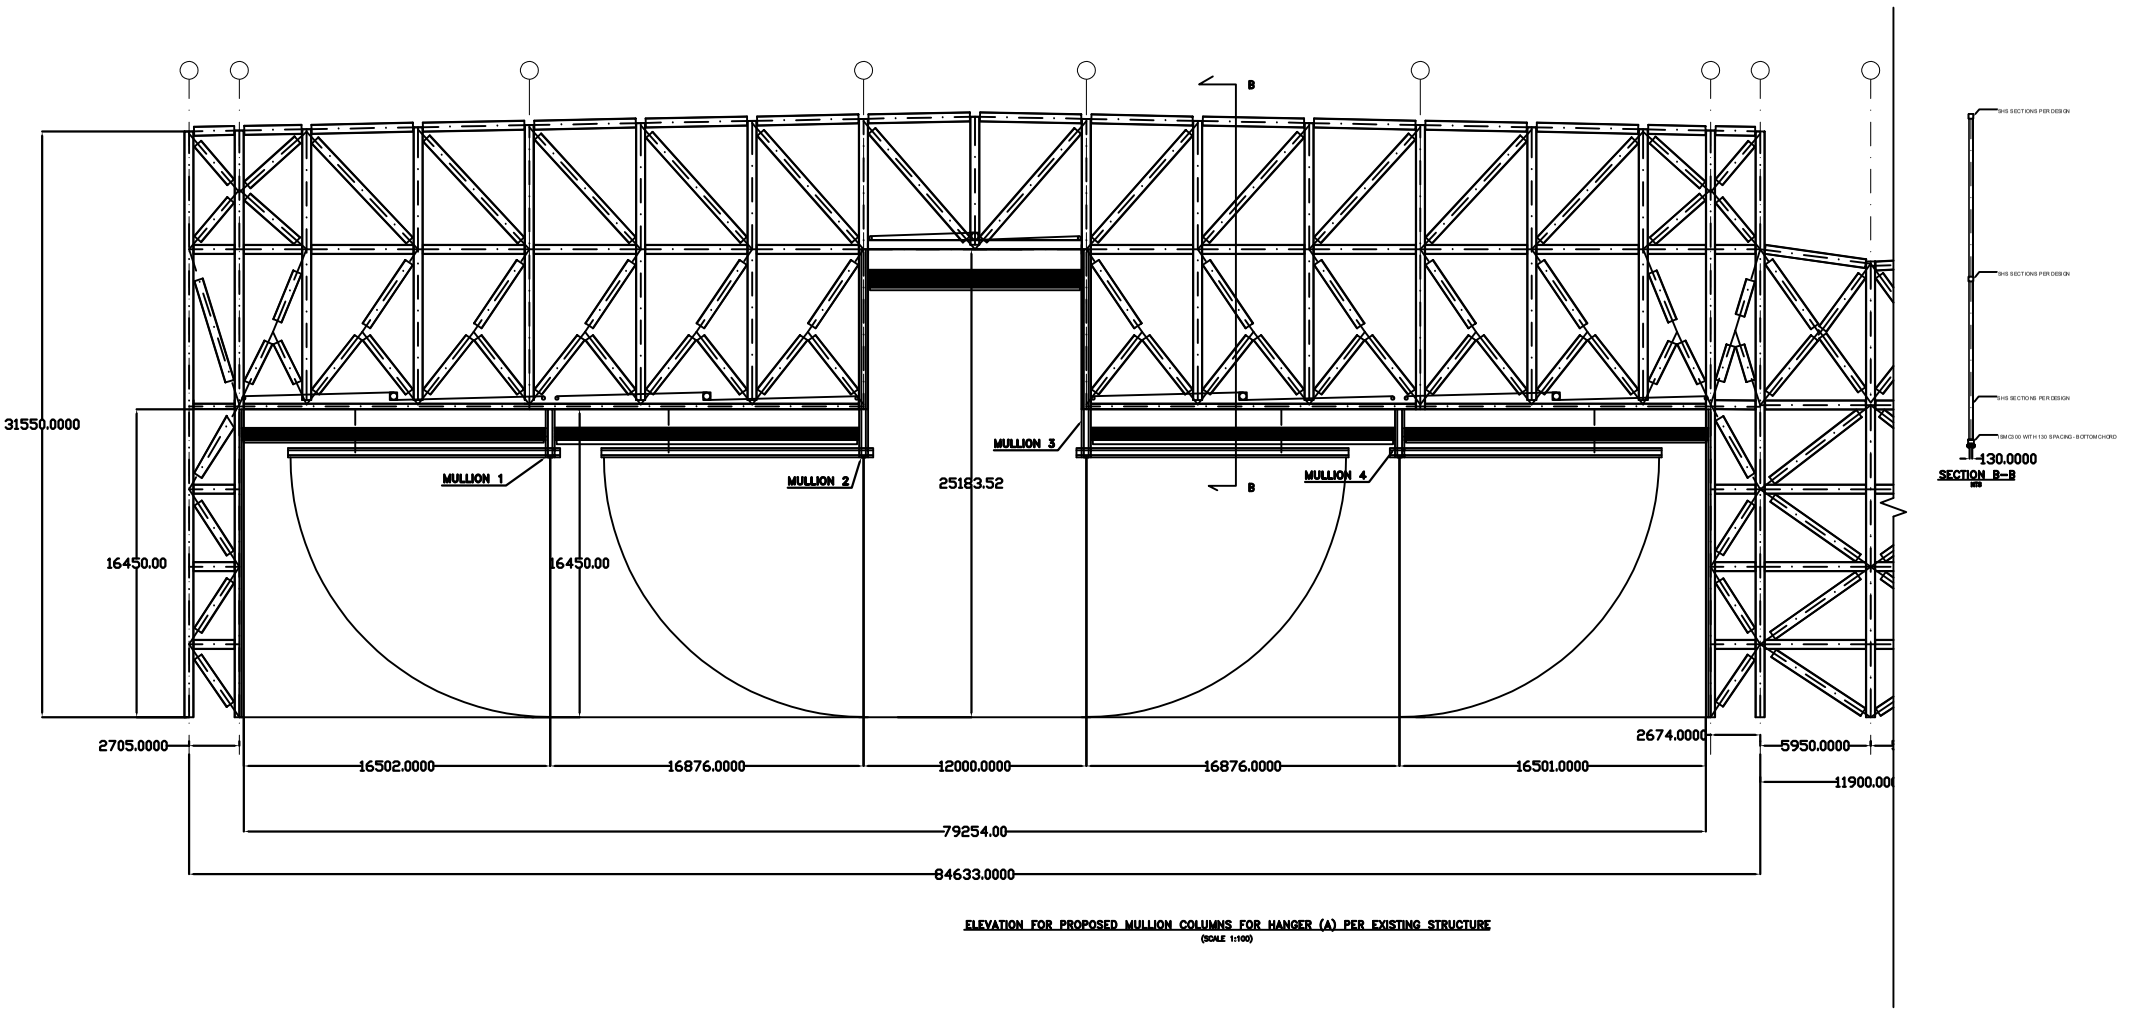

ELEVATION FOR PROPOSED MULLION COLUMNS FOR HANGER (A) PER EXISTING STRUCTURE
(SCALE 1:100)

REV.NO.	DESCRIPTION.	REV.DATE	DRAWN.	CHKD.	APPD.
1					

DWG.TITLE :- DRAWING FOR DOOR LOCATION HANGER (A)

PROJECT	
CLIENT	Hydrabad International Airport

SALT DESIGN SERVICES
4-PUSHKAR NIRZAR, SBI COLONY,
NEAR ICICI BANK, KOTHRUD, PUNE-411038.

DRAWN :RB	CHECKED : HAB	SCALE: 1:100
APPROVED : HAB	JOB CODE. : 1729	DATE: 17.09.2022
DWG.NO: SALT_1729_STR_01_R0	(SH-1OF2)	REV. - R0 SIZE. - A0

A1 [841 x 594]