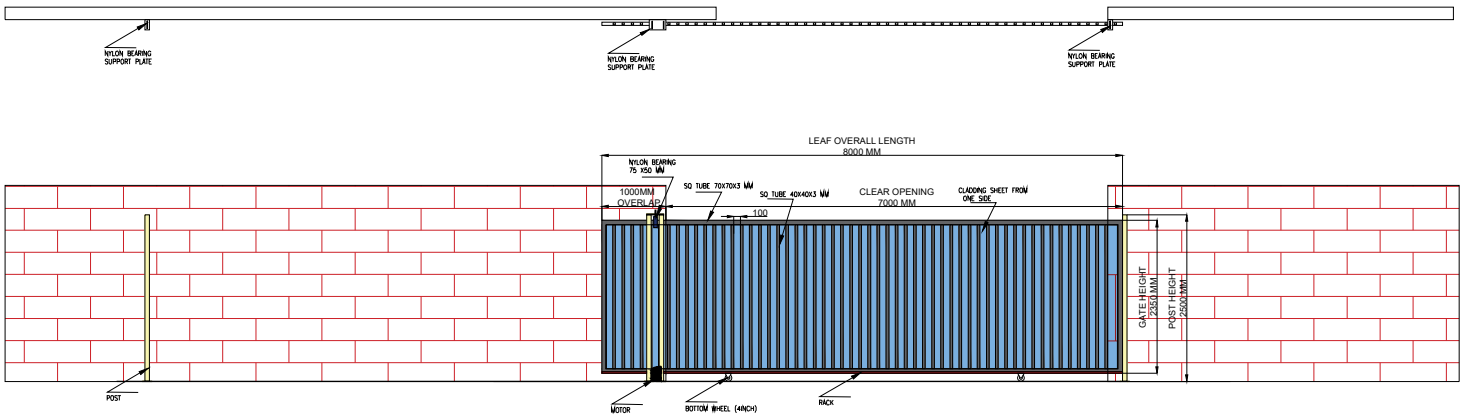


TECHNICAL SPECIFICATION:-

SR.	SPECIFICATION	DETAILS
1.	DOOR TYPE	MOTORIZED SINGLE LEAF SLIDING LEAF
2.	MOUNTING LOCATION AREA	INSIDE AREA
3.	OUTER FRAME & POST	SQ TUBE 70X70X3 MM
4.	INNEAR TUBE	SQ TUBE 40X40X3 MM
5.	BOTTOM RAIL ON GROUND	DIA 20 MM EN 8 BRIGHT BAR & ISMB -100X50 MM
6.	BOTTOM WHEEL	HEAVY DUTY WHEEL 4 INCH
7.	GUIDE ROLLER	NYLON ROLLERS-75X 50 MM
8.	COLOUR	
9.	OPERATING SWITCH	PUSH BUTTON FROM INSIDE

GATE SIZES :-

SR.	CLEAR OPENING	CLEAR HEIGHT	QTY.
01	7000 mm	2350 mm	01

This drawing & design is the property of NIHVA TECHNOLOGIES. Not to be sold or copied to any other concern.

TITLE

SLIDING GATES

	NAME	SIGN	DATE
DRAWN	B.S		15.04.2026
CHECK	V.T		15.04.2026
APPRD.	V.T		15.04.2026

If any queries contact : design2@nihva.com

ALL DIMENSION ARE IN mm

NIHVA TECHNOLOGIES PVT. LTD.
NIHVA TECHNOLOGIES PVT. LTD. PUNE
Tel : 020 66304033
Email:- info@nihva.com
Website:- www.nihva.com

CLIENT - CG POWER

PRODUCT - SLIDING GATES

FORMAT NO - NIHVA-DD-F-03

DWG. NO. : NIHVA/26-27 | REV- R00

SCALE: NTS | WT: | SHEET: