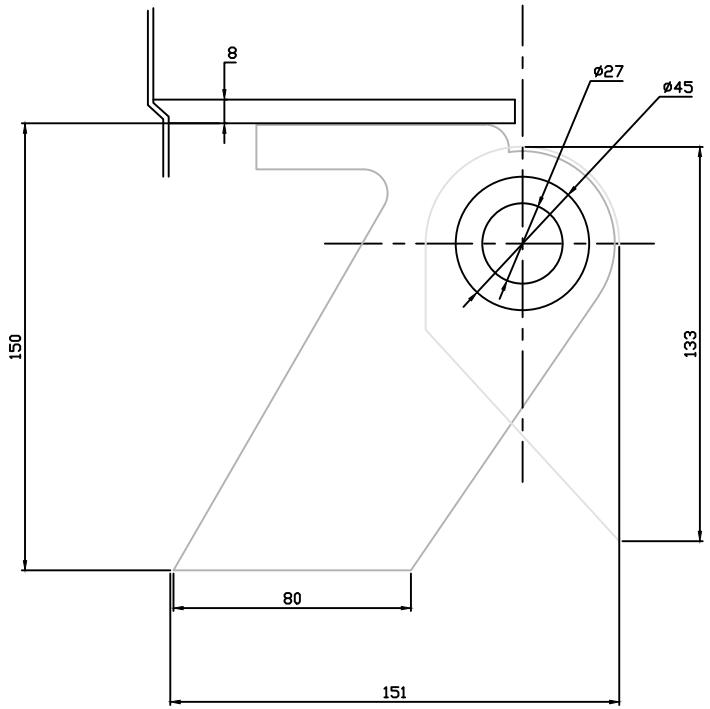

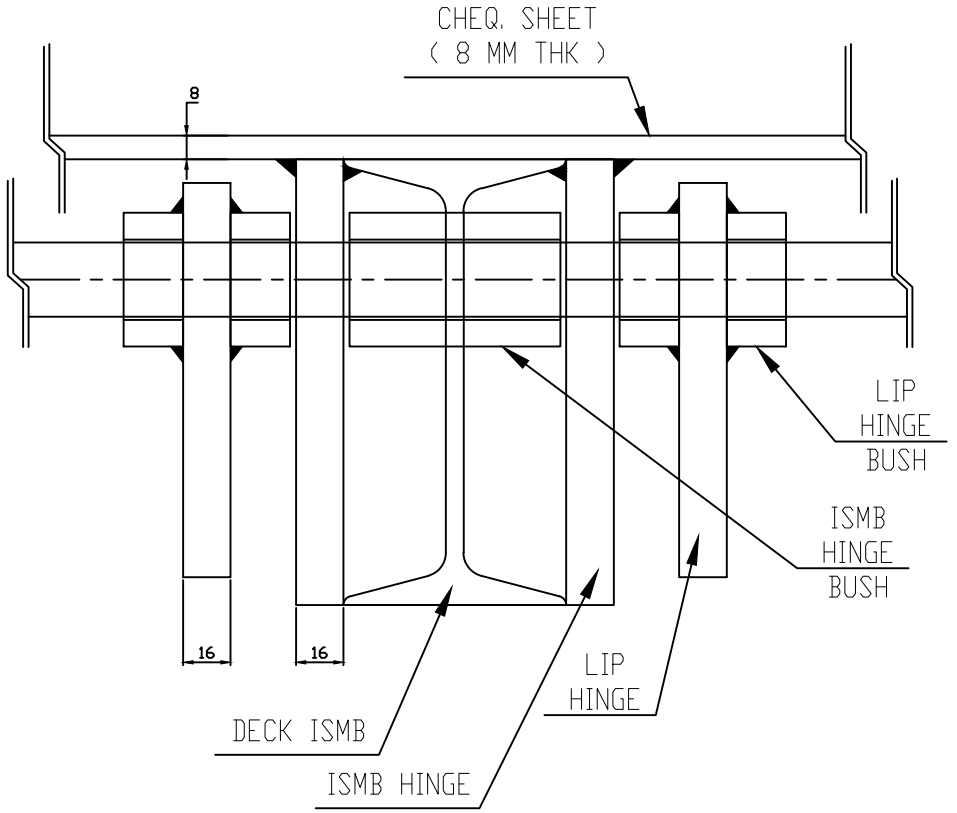

This drawing & design is the property of NIHVA TECHNOLOGIES. Not to be sold or copied to any other concern.

TITLE: NEW LIP ASSLY			NIHVA TECHNOLOGIES PVT. LTD.	NIHVA TECHNOLOGIES PVT. LTD, PUNE Tel : 020 66304033 Email:- info@nihva.com Website:- www.nihva.com
NAME	SIGN	DATE		
DRAWN P.A		30.06.2018	CLIENT -	
CHECK R.D		30.06.2018	PROJECT -	
APPRD. R.D		30.06.2018	SITE LOCATION -	
If any queries contact : design@nihva.com			DWG. NO. : NIHVA/18-19/052	
ALL DIMENSION ARE IN mm			SCALE:NTS	WT: REV- 00