

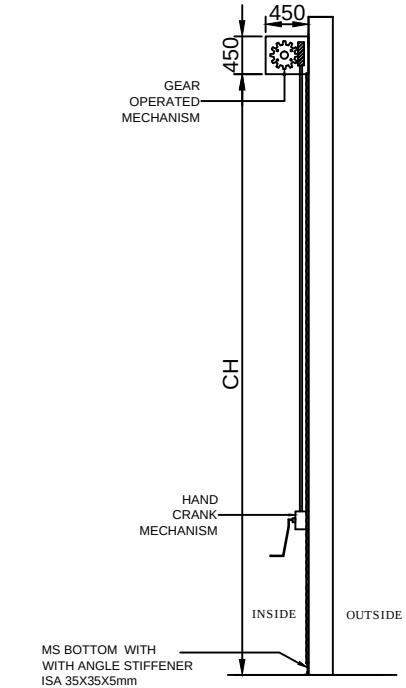




SIDE VIEW

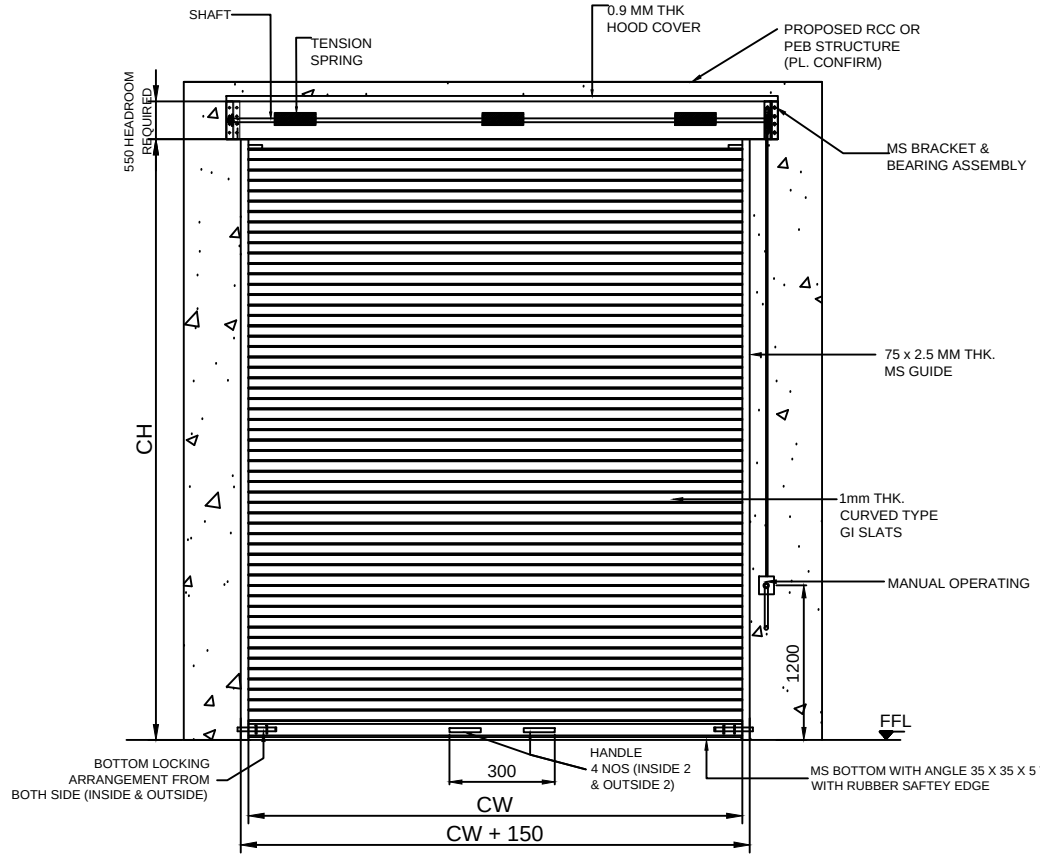



INSIDE ELEVATION

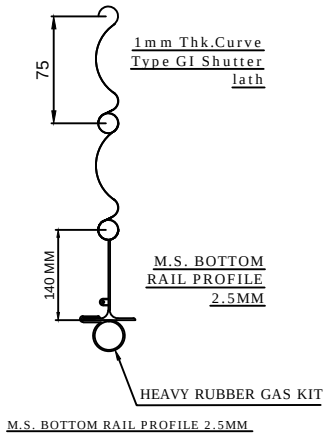


M.S. BOTTOM RAIL PROFILE 2.5MM

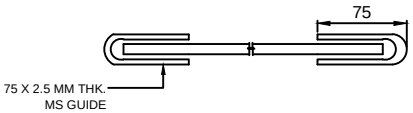

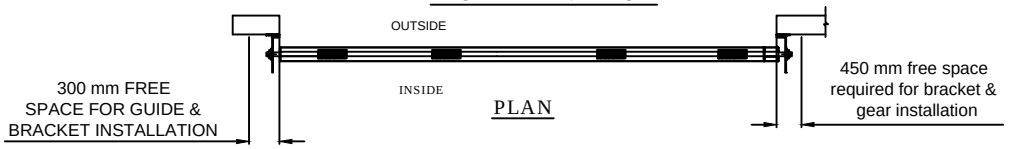
PLAN

TOLERANCE - ±5mm

| REV. NO | DATE | DRAWN | REMARK |
|---|---|---|---|
| R01 | 24.12.19 | P.A | 2. BOTTOM LOCK PROVISION<br>1. HANDLE ADDED. |

This drawing & design is the property of NIHVA TECHNOLOGIES. Not to be sold or copied to any other concern.

TITLE: GEAR OPERATED ROLLING SHUTTER With Right side gearbox

| | NAME | SIGN | DATE |
|---|---|---|---|
| DRAWN | P.A | | 07.12.2019 |
| CHECK | G.J | | 07.12.2019 |
| APPRD. | | | |

If any queries contact : design@nihva.com

ALL DIMENSION ARE IN mm

NIHVA TECHNOLOGIES PVT. LTD.
Website:- www.nihva.com

NIHVA TECHNOLOGIES PVT. LTD. PUNE
Tel : 020 66304033
Email:- info@nihva.com

CLIENT - PROGRESSIVE INFRA PROJECT PVT LTD.

PROJECT - VOSS

SITE LOCATION -

DWG. NO. : NIHVA/19-20/0169/R01 | REV- R01

SCALE: NTS | WT: | SHEET: 01 OF 01

NOTE-
1. ALL CIVIL WORK WILL BE CLIENT'S SCOPE.
2.STRUCTURE REQUIRED FOR SHUTTER IS IN CLIENT'S SCOPE.
3.FINAL FINISH OF SHUTTER WILL BE IN POWDER COATING OF APPROVED COLOR

| S.N. | CLEAR WIDTH (CW) | CLEAR HEIGHT (CH) | QTY |
|---|---|---|---|
| 1 | 3000 | 3300 | 02 |
| 2 | 4000 | 4500 | 01 |