




DETAIL G
SCALE 1 : 10

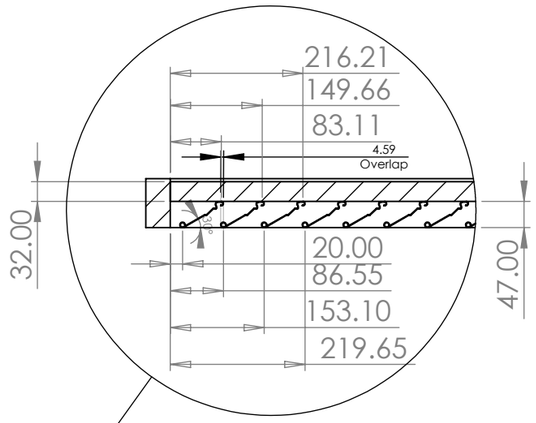



DETAIL H
SCALE 1 : 25

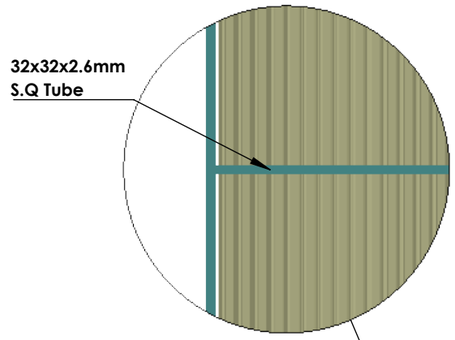

SECTION A-A

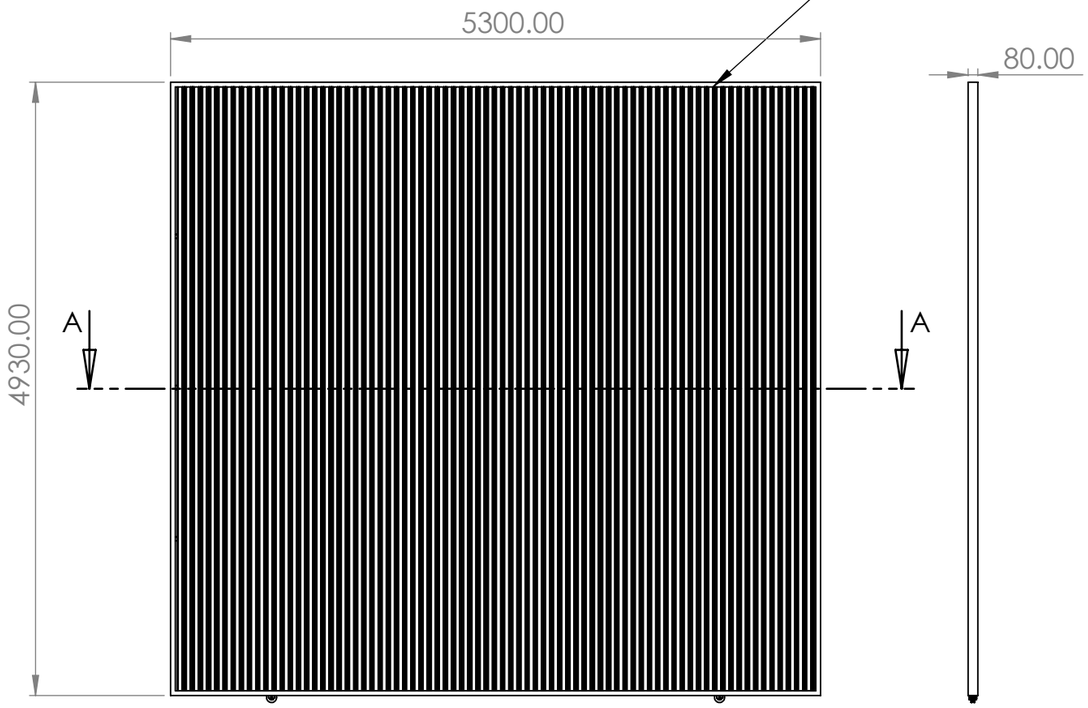

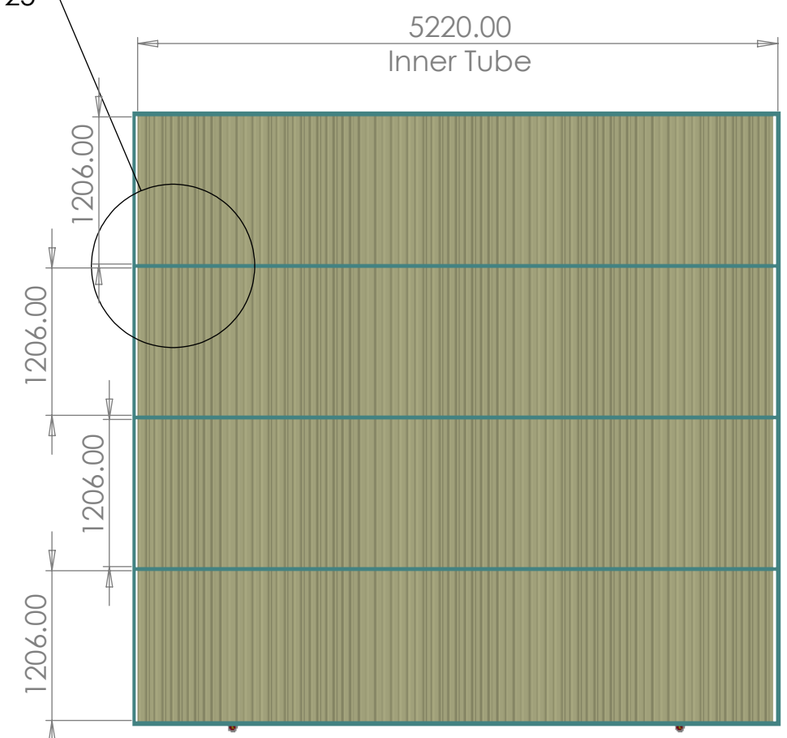

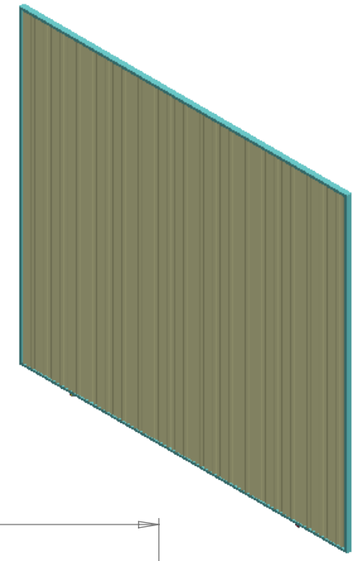

TITLE -	SLIDING LEAF			NIHVA Technologies Pvt. Ltd.	NIHVA TECHNOLOGIES PVT.LTD.PUNE Website - www.nihva.com
	NAME	SIGNATURE	DATE	CLIENT - **PANCHSHIL PRIVILEGE.**	
DRAWN	**S.J**		**28.02.2024**	PRODUCT - **Manual Sliding Gate For DG Substation**	
CHK'D	**A.K**		**28.02.2024**	SITE LOCATION - **Kharadi, Pune**	
APPV'D	**V.T**		**28.02.2024**	QTY - 14	
if any queries contact - supportautomation@nihva.com				DWG NO - NIHVA/22-23/00XX	REVISION -
ALL DIMENSION ARE IN mm			A3	SCALE -	SHEET 1 OF 1