






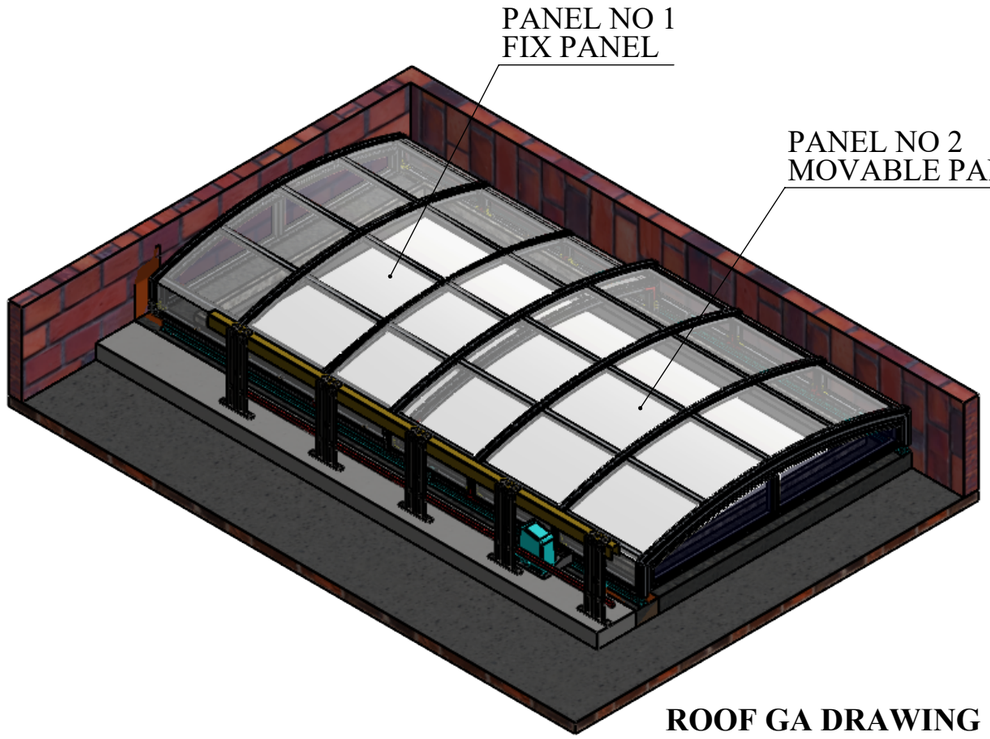

ROOF GA DRAWING

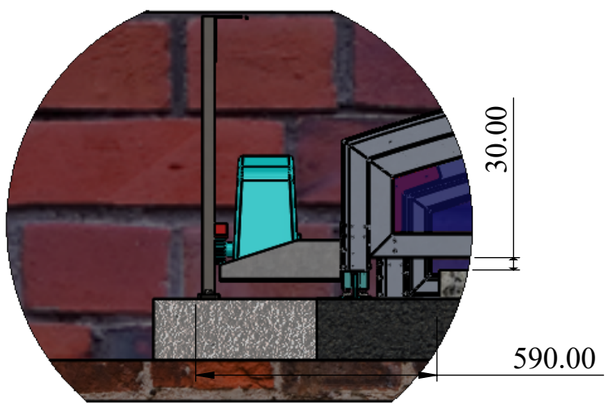


DETAIL A
SCALE 1 : 15

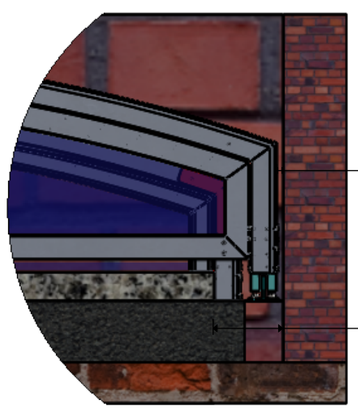



DETAIL B
SCALE 1 : 15

NOTE :
OPENING 2117MM WILL BE AVAILABLE

TITLE - ROOF AUTOMATION				NIHVA TECHNOLOGIES PVT.LTD.PUNE
DWG NO - NTPL-000-PM-001-00-00-00				Website - www.nihva.com
	NAME	SIGNATURE	DATE	PROJECT NO - NTPL-000-PM
DRAWN	V.W		10-06-2025	PRODUCT - RETRACTABLE ROOF
CHK'D	S.W.		10-06-2025	SITE LOCATION - LUCKNOW
APPV'D	V.T.		10-06-2025	
if any queries contact - supportautomation@nihva.com				REVISION - 01 / QTY - 1
ALL DIMENSION ARE IN mm		A3		SCALE / SHEET 1 OF 2

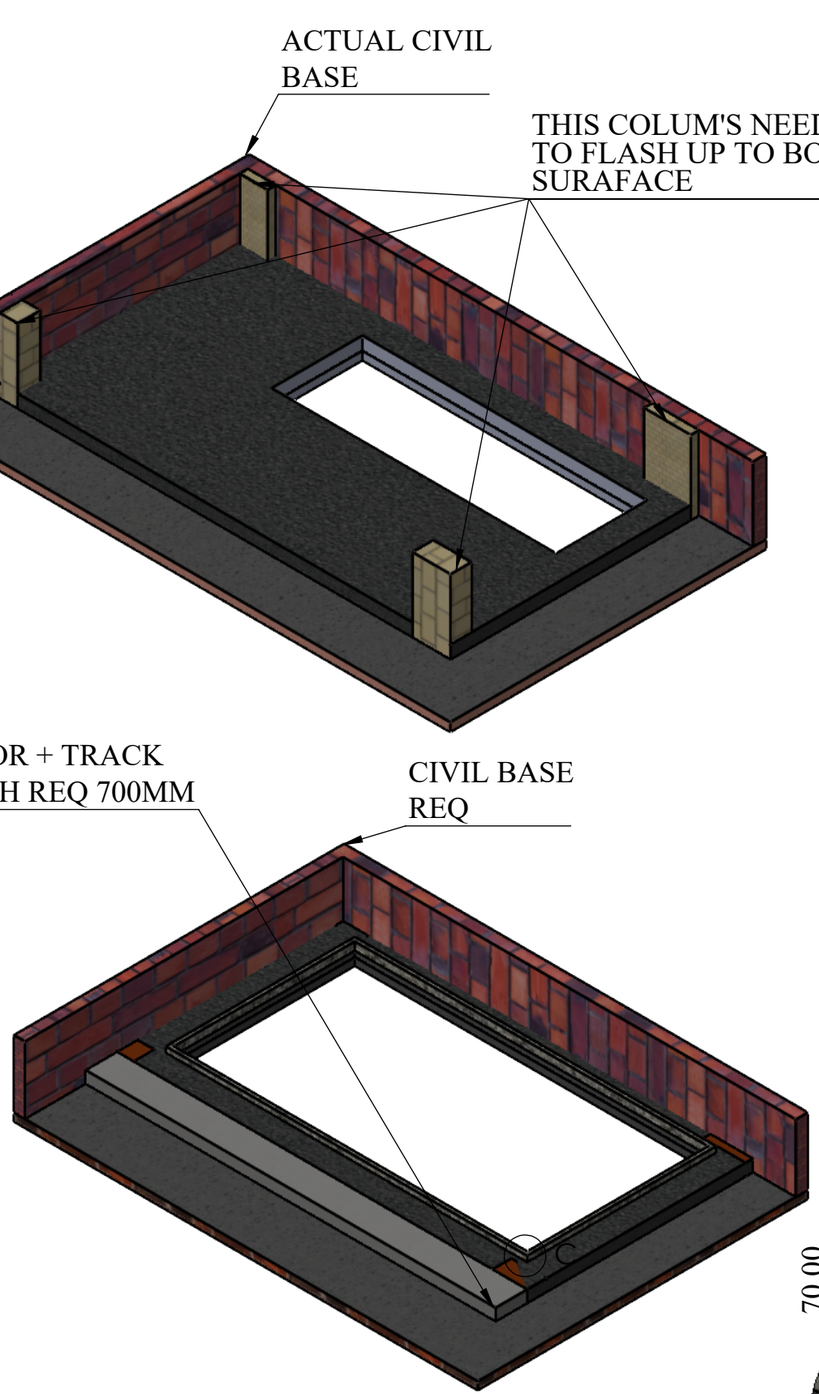

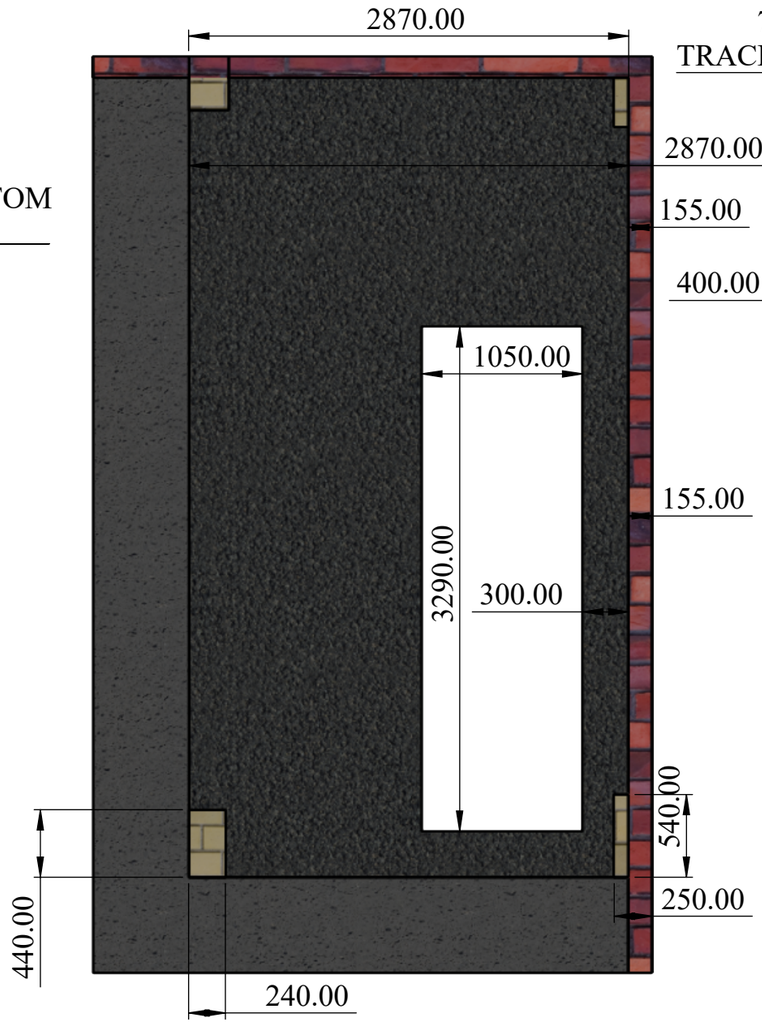

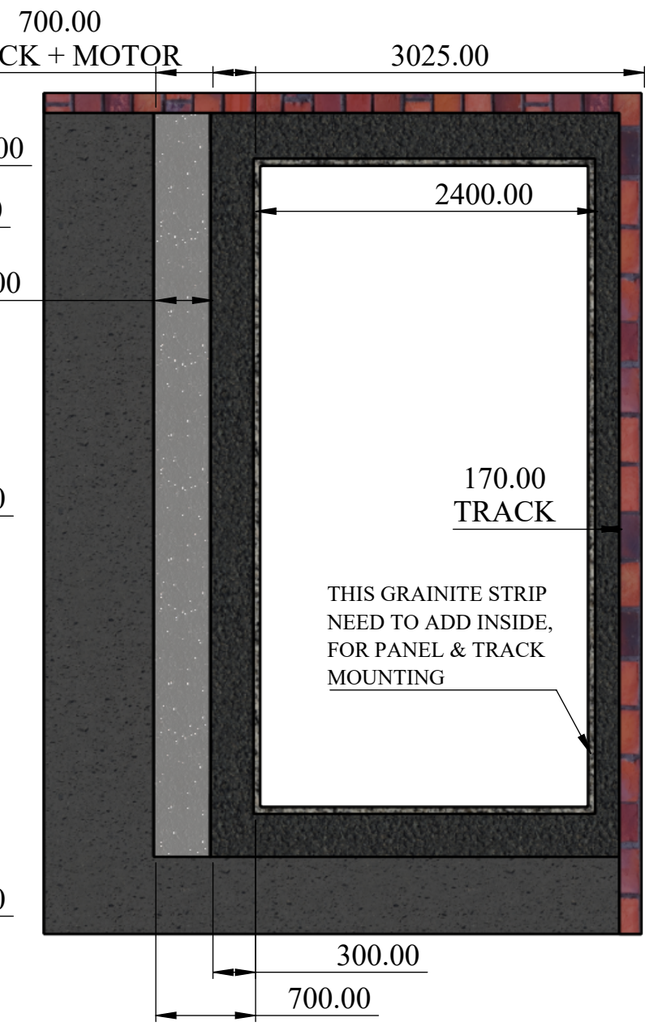




ACTUAL CIVIL
BASE



CIVIL BASE
REQ

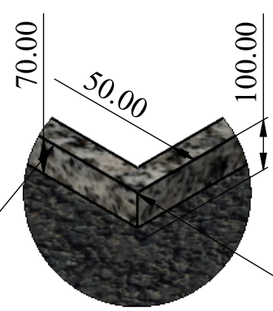

GRANITE STRIP NEED TO
ADD TO RESTRICT WATER FLOW
INSIDE

GRANITE STRIP
100*50MM

DETAIL C
SCALE 1 : 10

CIVIL DRAWING

TITLE - ROOF AUTOMATION				NIHVA TECHNOLOGIES PVT.LTD.PUNE
DWG NO - NTPL-000-PM-001-00-00-00				Website - www.nihva.com
	NAME	SIGNATURE	DATE	PROJECT NO - NTPL-000-PM
DRAWN	V.W		10-06-2025	PRODUCT - RETRACTABLE ROOF
CHK'D	S.W.		10-06-2025	SITE LOCATION - LUCKNOW
APPV'D	V.T.		10-06-2025	
if any queries contact - supportautomation@nihva.com				REVISION - 01 / QTY - 1
ALL DIMENSION ARE IN mm		A3		SCALE / SHEET 2 OF 2