

DRAWING

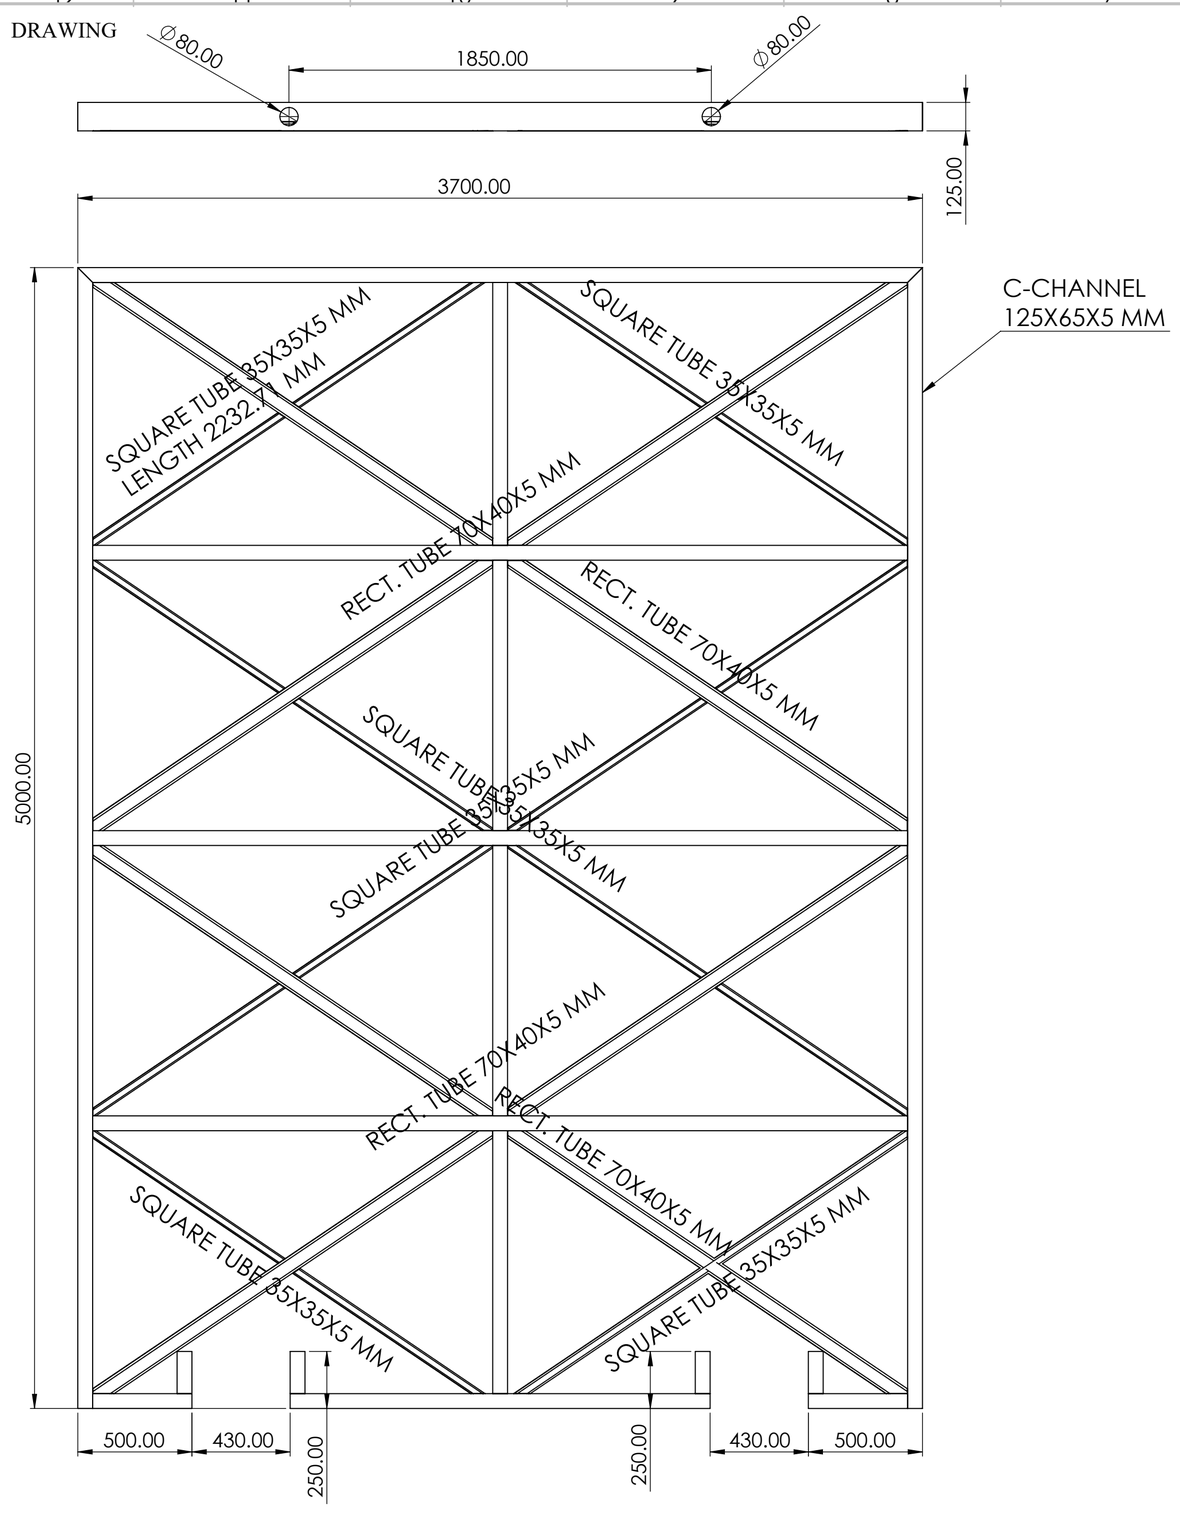

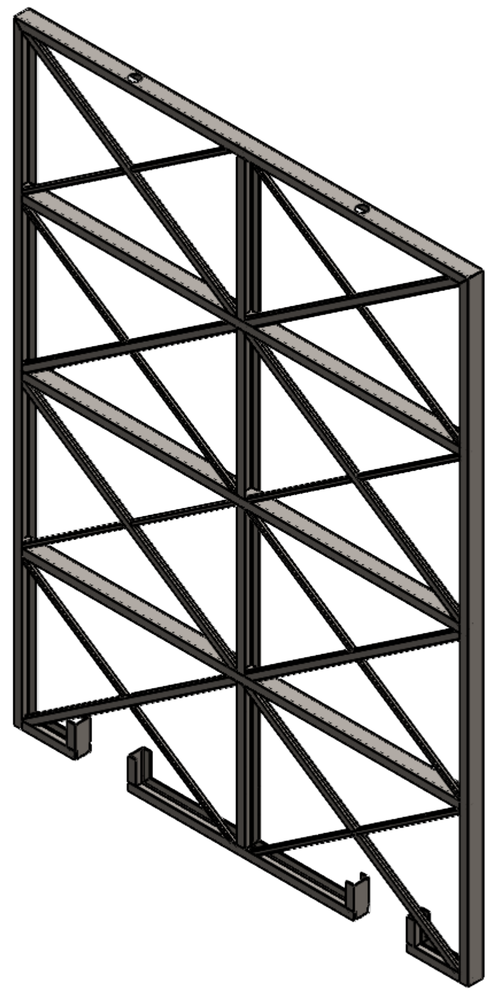

HANGER SLIDING DOOR
ISOMATRIC VIEW

REV DESCRIPTION	DATE	REV NO
	04-07-2025	REV 00
REVISION 01 1)EXTRA INTERMEDIATE SQUARE TUBE (35X35X5 MM) SUPPORT ADDED AS PER CLIENT REQUEST. 2) THIS SQ. TUBE FITTED ON SITE.		

NOTE :

1)SQUARE TUBE 35X35X5 MM THK
LENGTH 2232.71 MM
2)RECTANGULAR TUBE 70X40X5 MM THK
3) ISMC C-CHANNEL125X65X5 MM THK

SPECIAL INSTRUCTION'S :

TITLE - ROOF AUTOMATION


DWG NO - NTPL-000-PM-001-00-00-00


NIHVA TECHNOLOGIES PVT.LTD.PUNE
Website - www.nihva.com

	NAME	SIGNATURE	DATE
DRAWN	V.W.		03-07-2025
CHK'D	S.W.		05-07-2025
APPV'D	V.T.		06-07-2025

PRODUCT - RETRACTABLE ROOF
PROJECT NO - NTPL-000-PM
REVISION - 00
SITE LOCATION -
WEIGHT -
MATRIAL -
QTY - 1
If any queries contact - design.nihva@gmail.com
PROJECTION METHOD:
SCALE :
ALL DIMENSION ARE IN mm
A2
SHEET 1 OF 2

DRAWING

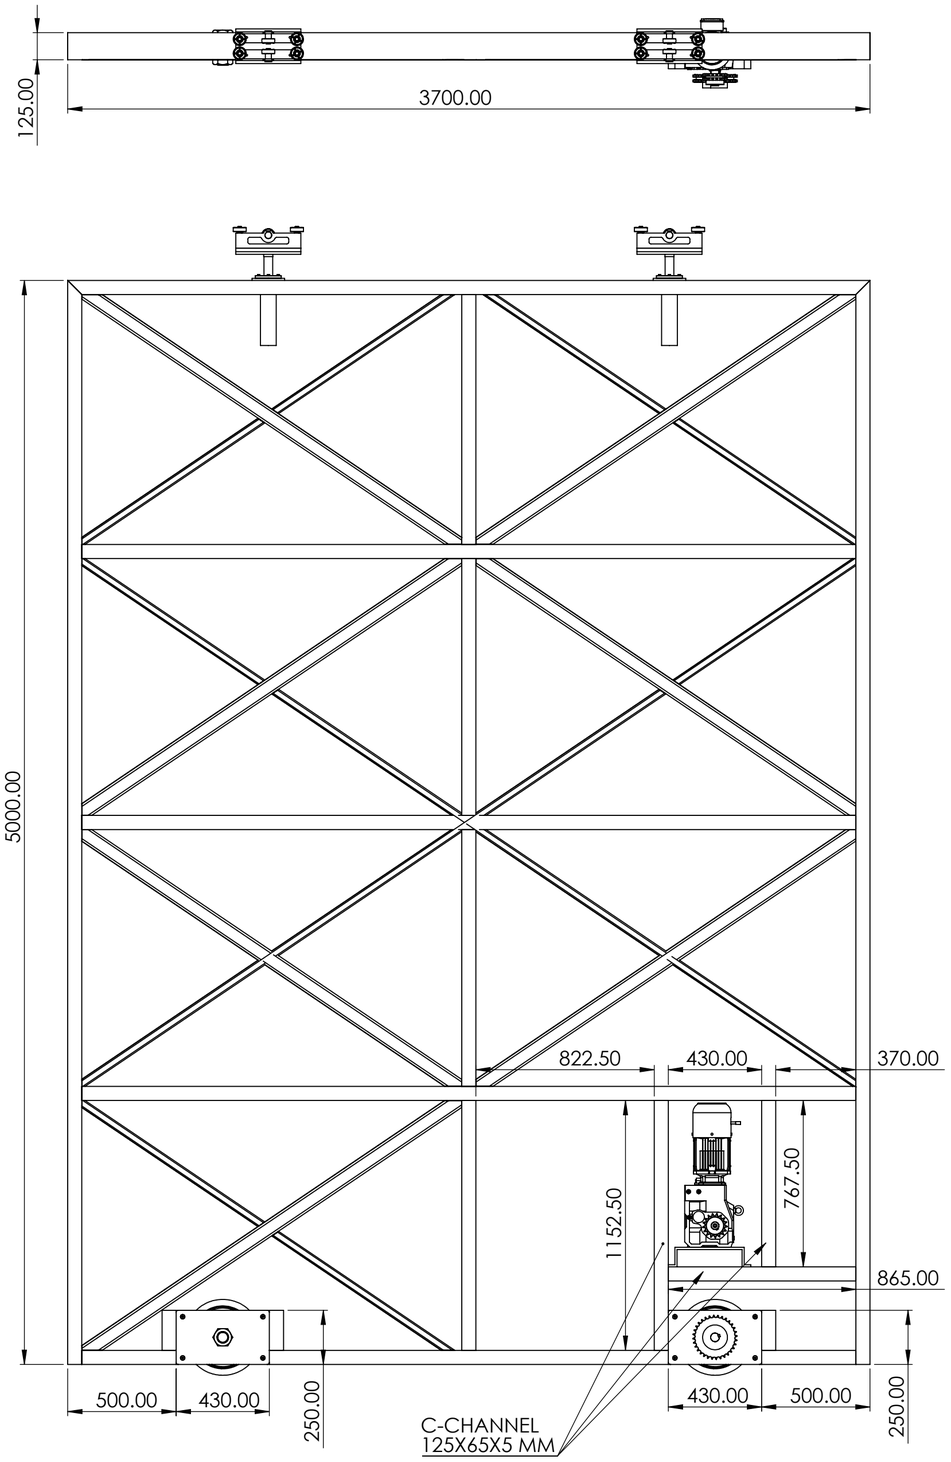

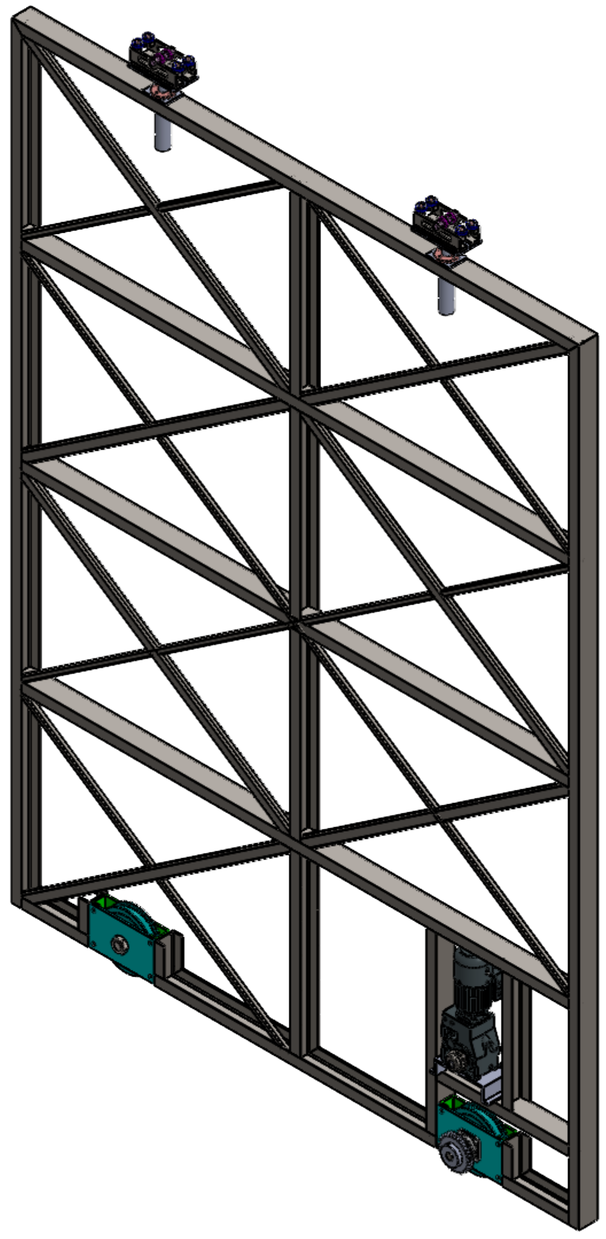

REV DESCRIPTION	DATE	REV NO
	04-07-2025	REV 00
1. Xyz		

NOTE :

SPECIAL INSTRUCTION'S :

TITLE - ROOF AUTOMATION

DWG NO - NTPL-000-PM-001-00-00-00

NIHVA TECHNOLOGIES PVT.LTD.PUNE
Website - www.nihva.com

	NAME	SIGNATURE	DATE
DRAWN	V.W.		03-07-2025
CHK'D	S.W.		05-07-2025
APPV'D	V.T.		06-07-2025

PRODUCT - RETRACTABLE ROOF

PROJECT NO - NTPL-000-PM | REVISION - 00

SITE LOCATION - | WEIGHT -

MATRIAL - | QTY - 1

If any queries contact - design.nihva@gmail.com

PROJECTION METHOD:

SCALE :

ALL DIMENSION ARE IN mm | A2