
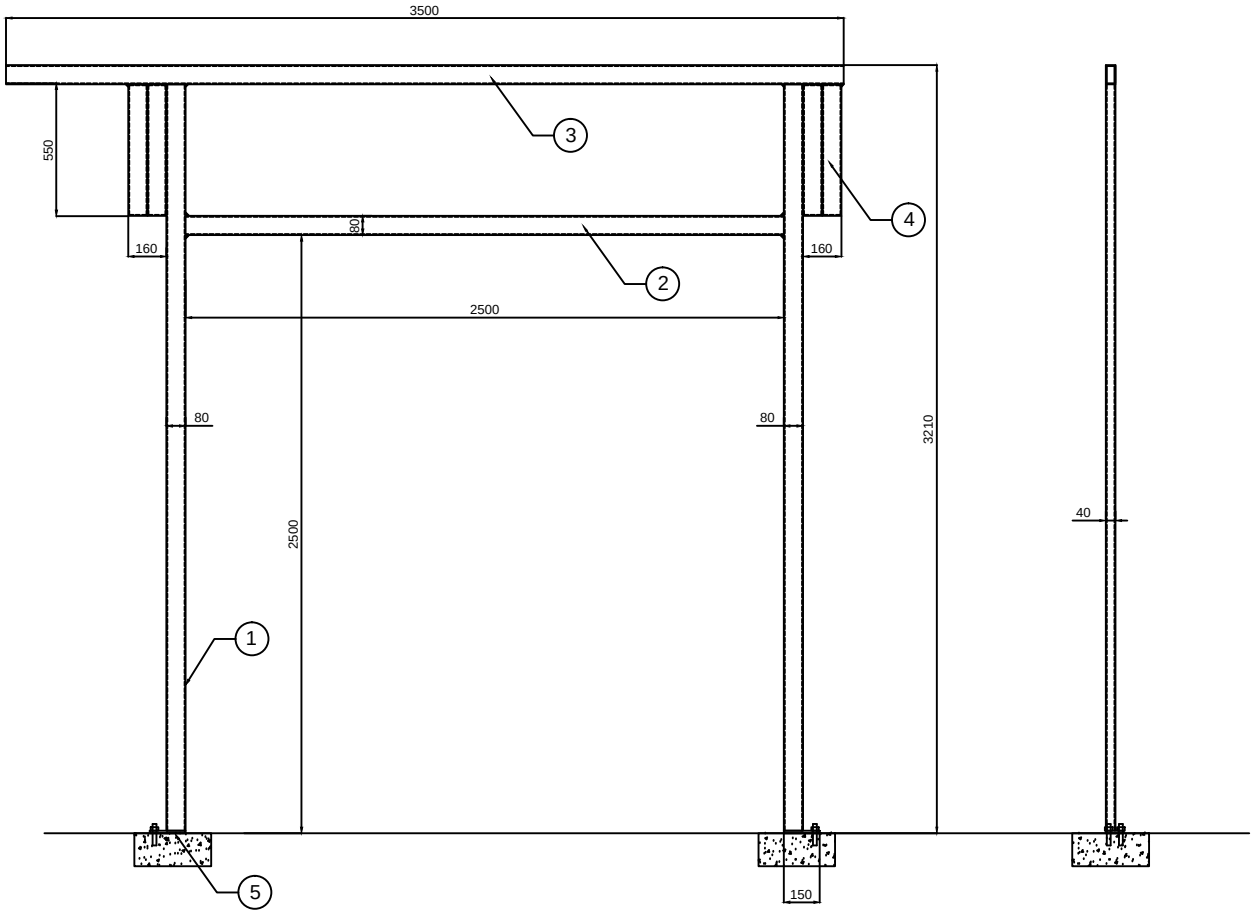


SR NO	DESCRIPTION	SPECIFICATION	QTY
1	R.TUBE	80 X 40 X 4 THK X 3120L	2 NOS
2	R.TUBE	80 X 40 X 4 THK X 2500L	1 NO
3	R.TUBE	80 X 40 X 4 THK X 3500L	1 NO
4	R.TUBE	80 X 40 X 4 THK X 550L CLOSE END	4 NOS
5	FLAT	75 X 10 X 150L	2 NOS
6	ANCHOR BOLT	M12 X 100L	4 NOS
7	R.TUBE	80 X 40 X 4 THK X 200L	2 NOS
8	ISA	50 X 5 X 50L	10 NOS

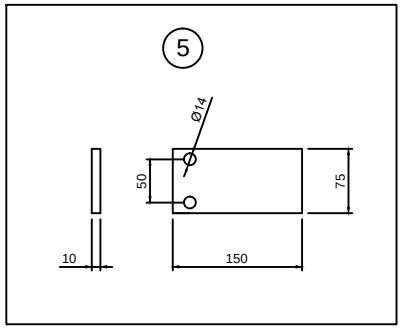

COLOR : RAL 9002
PURE WHITE

TOLERANCE - ±5mm

This drawing & design is the property of NIHVA TECHNOLOGIES. Not to be sold or copied to any other concern.

TITLE
MOTORIZED ROLLING SHUTTER STRUCTURE

	NAME	SIGN	DATE
DRAWN	P.A		19.03.2020
CHECK	G.J		19.03.2020
APPRD.			

If any queries contact : design@nihva.com

ALL DIMENSION ARE IN mm

NIHVA
NIHVA TECHNOLOGIES PVT. LTD.
Website:- www.nihva.com
NIHVA TECHNOLOGIES PVT. LTD. PUNE
Tel : 020 66304033
Email:- info@nihva.com

CLIENT -

PROJECT -

SITE LOCATION -

DWG. NO. : NIHVA/19-20/VDR/375 | REV- R00

SCALE: NTS | WT: | SHEET: 01 OF 01