
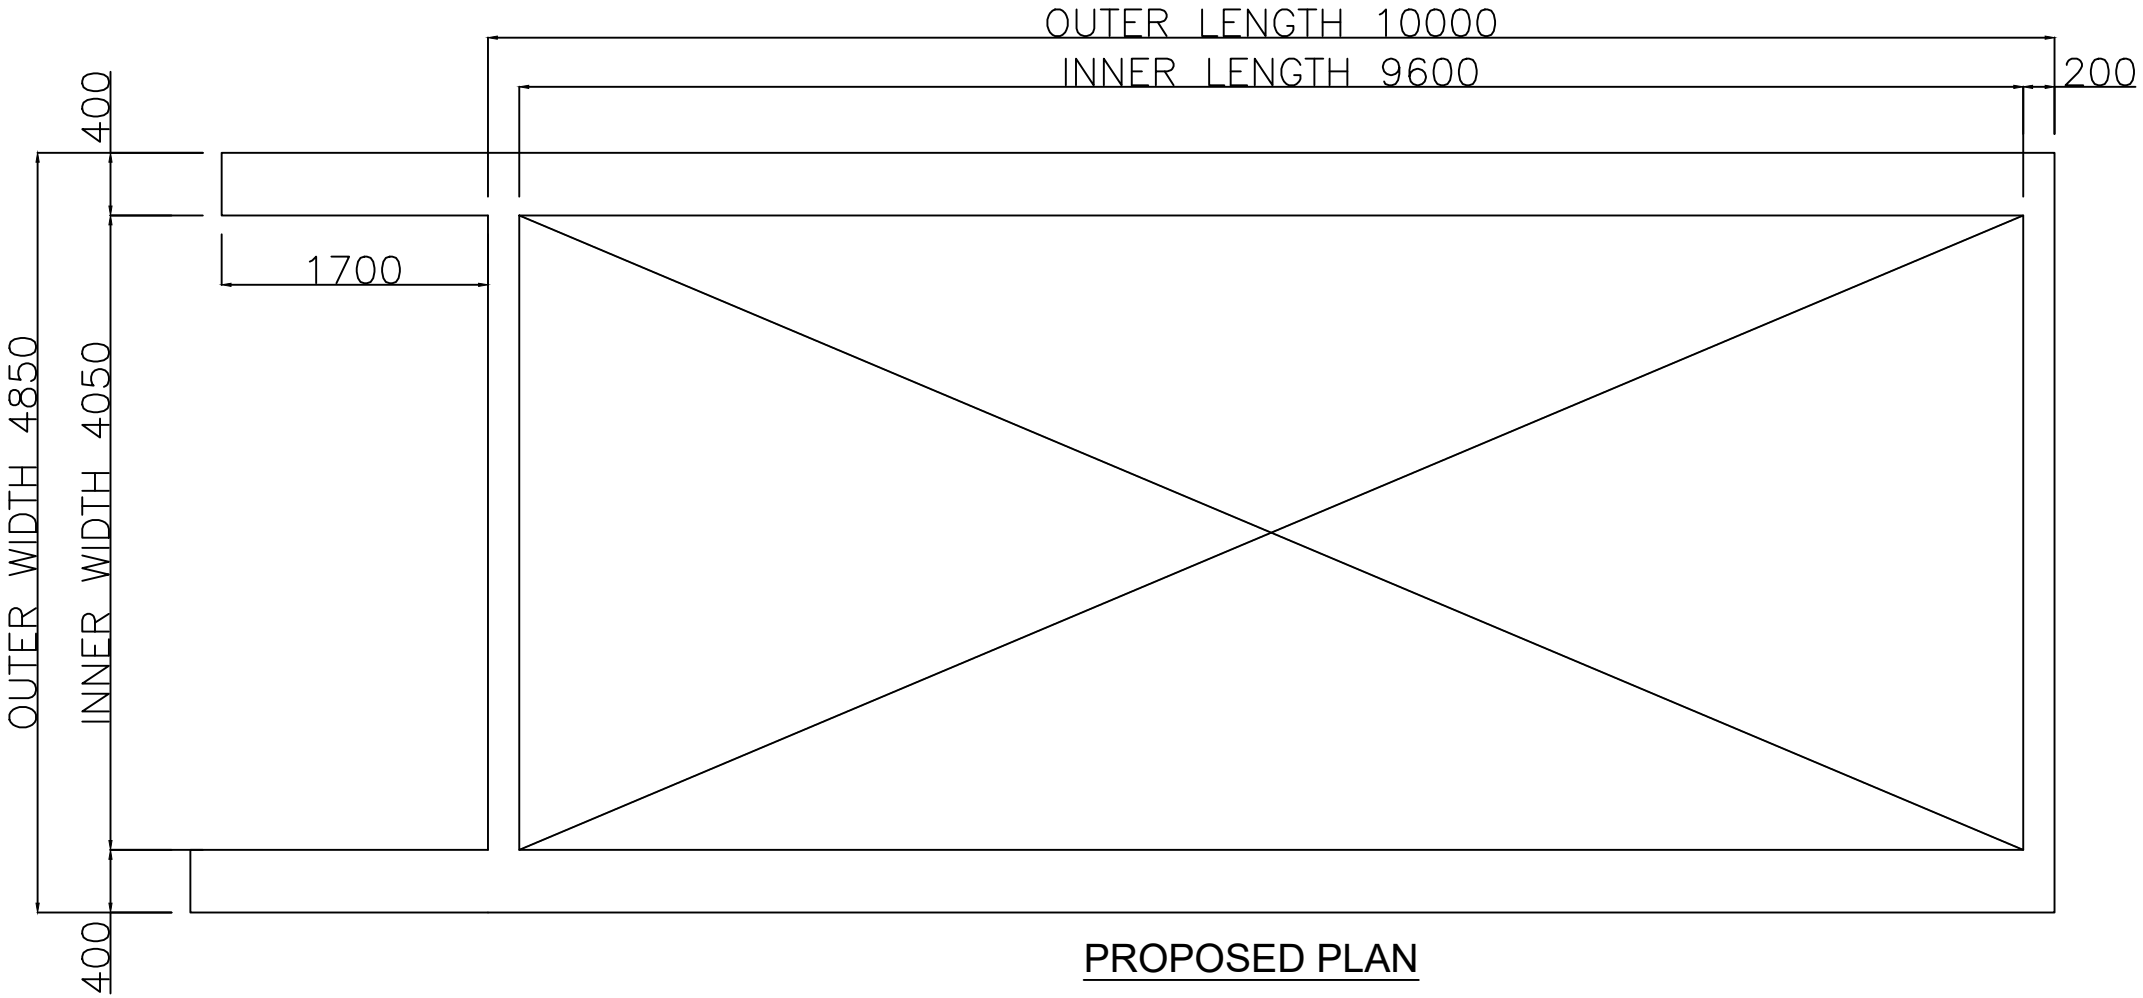


PROPOSED PLAN

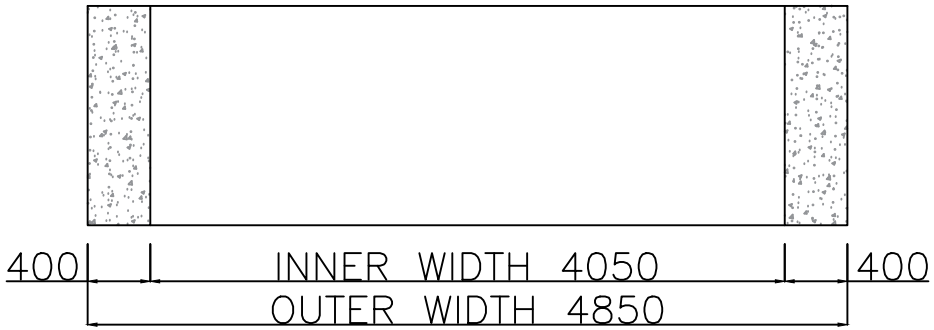

SECTION VIEW

NOTE :-

1. THE STRUCTURE AROUND THE POOL SHOULD BE OF CONCRETE FOR PROPER FASTENING OF POOL COVER.
2. TOP SURFACE SHOULD BE OF GRANITE 20MM FOR SMOOTH FUNCTIONING OF THE SYSTEM.
3. AL PROFILE - POWDER COATED
4. GASKET - EPDM
5. ALL DIMENSION IN MM.