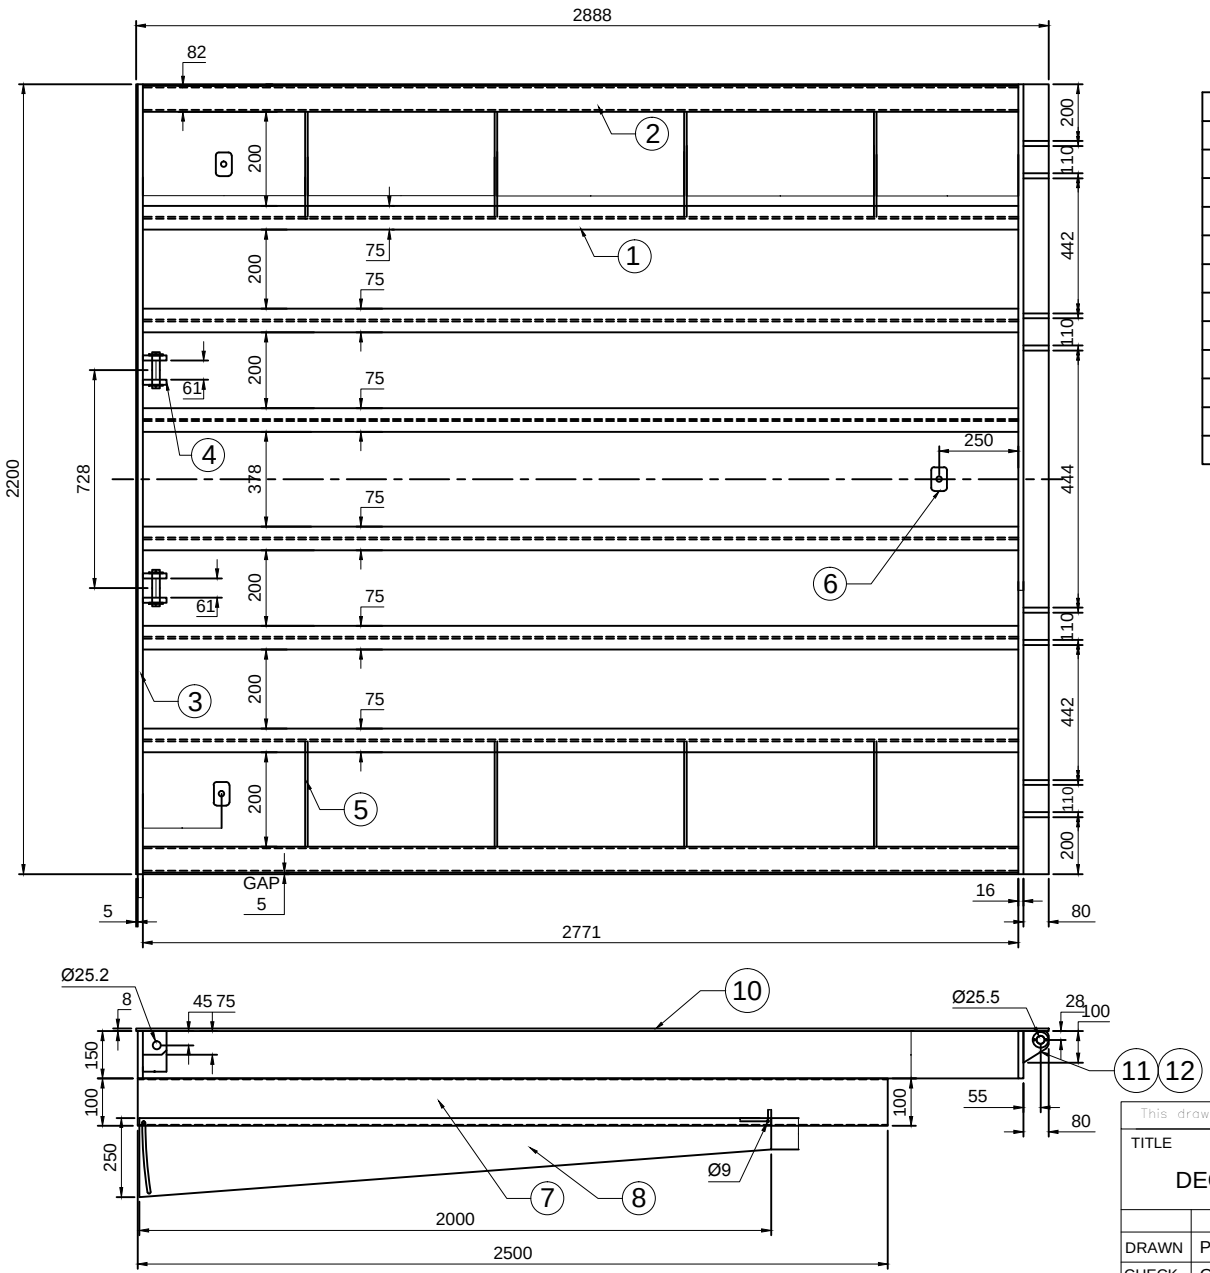


NOTE:~ MTL : MS

PART NO.	PART NAME	DESCRIPTION	QTY
1.	ISMB	150 X 75 X 2770L	6 NOS
2.	R.TUBE	145 X 82 X 4.8THK X 2770L	2 NOS
3.	FLAT	150 X 16 X 2200L	2 NOS
4.	FLAT	75 X 16 X 75L	4 NOS
5.	FLAT	150 X 8 X 234L	8 NOS
6.	FLAT	50 X 16 X 75L (M16 TAPPING)	3 NOS
7.	FLAT	100 X 3THK X 2500L	2 NOS
8.	SIDE COVER	USE STD	2 NOS
9.	LIP STOPER	Ø25 X 53L	4 NOS
10.	CHEQ.SHEET	2200 X 8 THK X 2888L	1 NO
11.	PROFILE	80 X 16 THK X 100L	10 NOS
12.	PROFILE	50 X 5 THK	2 NOS

This drawing & design is the property of NIHVA TECHNOLOGIES. Not to be sold or copied to any other concern.

TITLE

DECK ASSLY

NIHVA TECHNOLOGIES PVT. LTD.

NIHVA TECHNOLOGIES PVT. LTD. PUNE
Tel : 020 66304033
Email:- info@nihva.com
Website:- www.nihva.com

	NAME	SIGN	DATE
DRAWN	P.A		31.12.2019
CHECK	G.J		31.12.2019
APPRD.			

CLIENT -

PROJECT -

SITE LOCATION -

If any queries contact : design@nihva.com

DWG. NO. : NIHVA/19-20/VDR/260

ALL DIMENSION ARE IN mm

SCALE: NTS | WT: | REV- 00