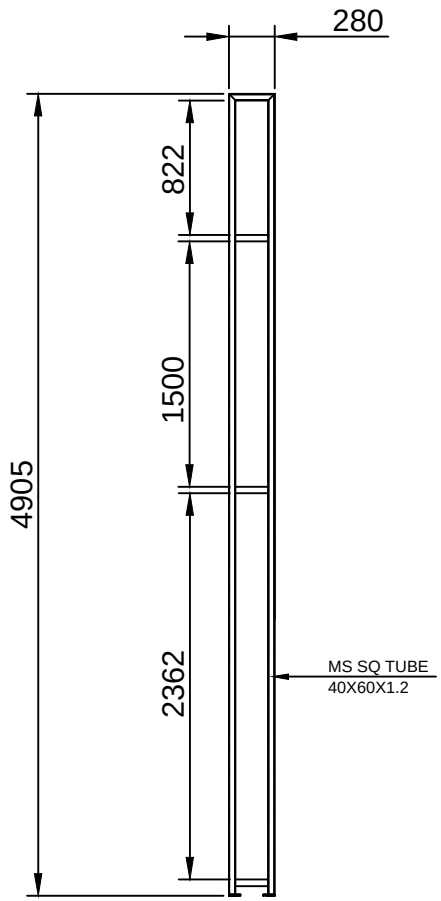

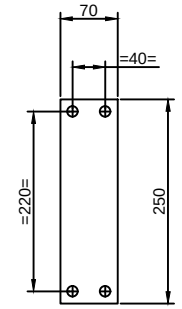

MATERIAL:MS PLATE
THK:10MM
QTY:04 nos

CRM DOOR 13

QTY:02 NOS

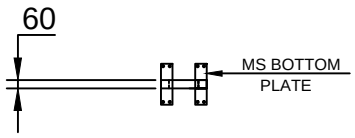

This drawing & design is the property of NIHVA TECHNOLOGIES. Not to be sold or copied to any other concern.

4LEAF-BOTH SIDE CRM DOOR-13			NIHVA TECHNOLOGIES PVT. LTD. PUNE Tel : 020 66304033 Email:- info@nihva.com Website:- www.nihva.com
	NAME	DATE	
DRAWN	KISHAN	16/05/2022	CLIENT - NIHVA TECHNOLOGIES PVT LTD
CHECK	M.SUTAR	16/05/2022	LOCATION -
APPRD.	V.TARAK	16/05/2022	PRODUCT - SLIDING DOOR
If any queries contact : design@nihva.com			DWG NO:-NIHVA/22-23/CLT/
ALL DIMENSION ARE IN mm			SCALE: NTS / SCALE:-- 1:1 / SHEET:

Rev No.	Revision	Date	Revised By