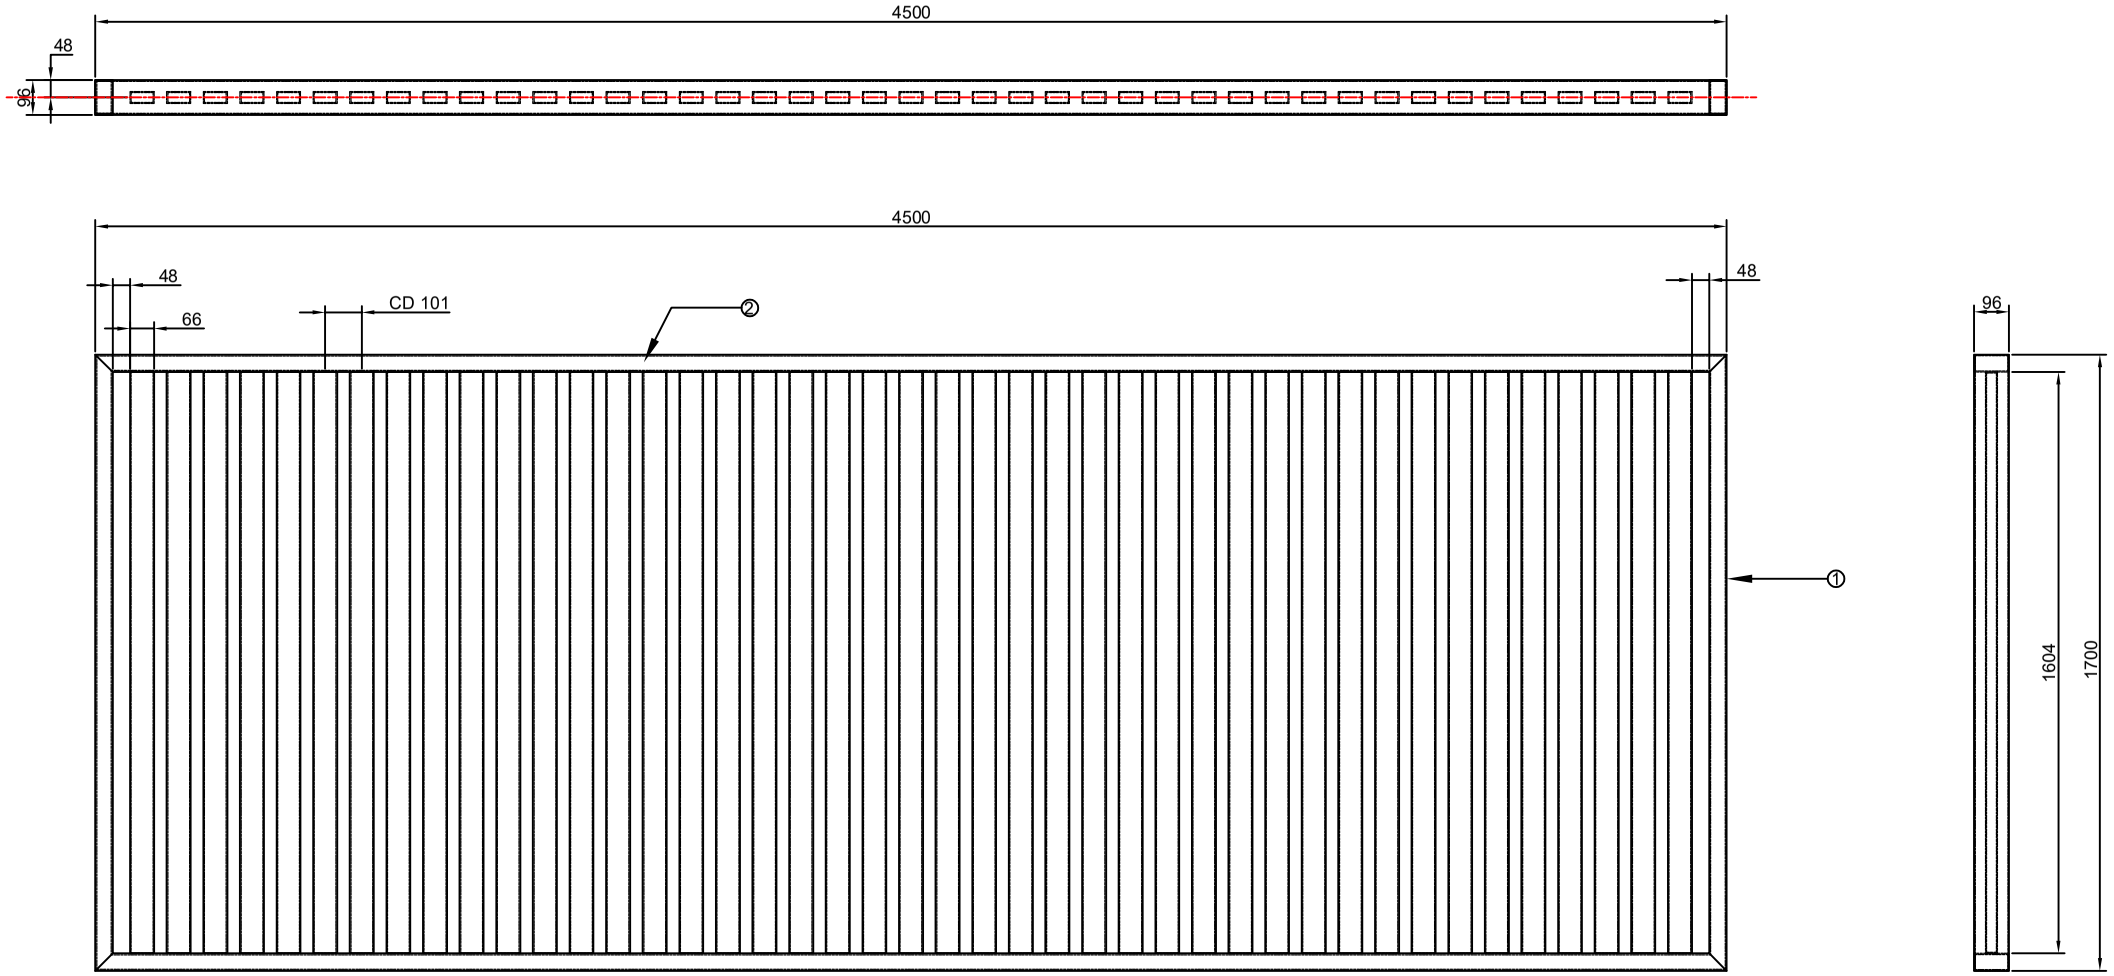


BOM			
SL NO.	DESCRIPTION	SPECIFICATION	QTY
1	MS RECT. TUBE	96X48X4X1700L	2NOS
2	MS RECT. TUBE	96X48X4X4500L	2NOS
3	MS RECT. TUBE	66X33X2.9X1604L	43NOS

Rev No.	Revision	Date	Revised By

This drawing & design is the property of NIHVA TECHNOLOGIES. Not to be sold or copied to any other concern.

TITLE:- TEL.SLIDING GATE

	NAME	DATE	SIGN
DRAWN	SUJATA	07/03/2022	
CHECK	G.PATIL	08/03/2022	
APPRD.	A.K	08/03/2022	

If any queries contact : design@nihva.com

ALL DIMENSION ARE IN mm

NIHVA TECHNOLOGIES PVT. LTD.
NIHVA TECHNOLOGIES PVT. LTD. PUNE
Tel : 020 66304033
Email:- info@nihva.com
Website:- www.nihva.com

CLIENT -

LOCATION -

PRODUCT - TEL.SLIDING GATE | QTY- 04

DWG NO:-NIHVA/21-22/MFG/038 | REV- 0

SCALE: NTS | SCALE:-- 1:1 | SHEET: 01 OF 01