



RAL CODE	COLOR SHADE
7035	LIGHT GRAY
7035	LIGHT GRAY
7001	SILVER GRAY
9010	PURE WHITE
9002	GRAY WHITE
9001	CREAM WHITE

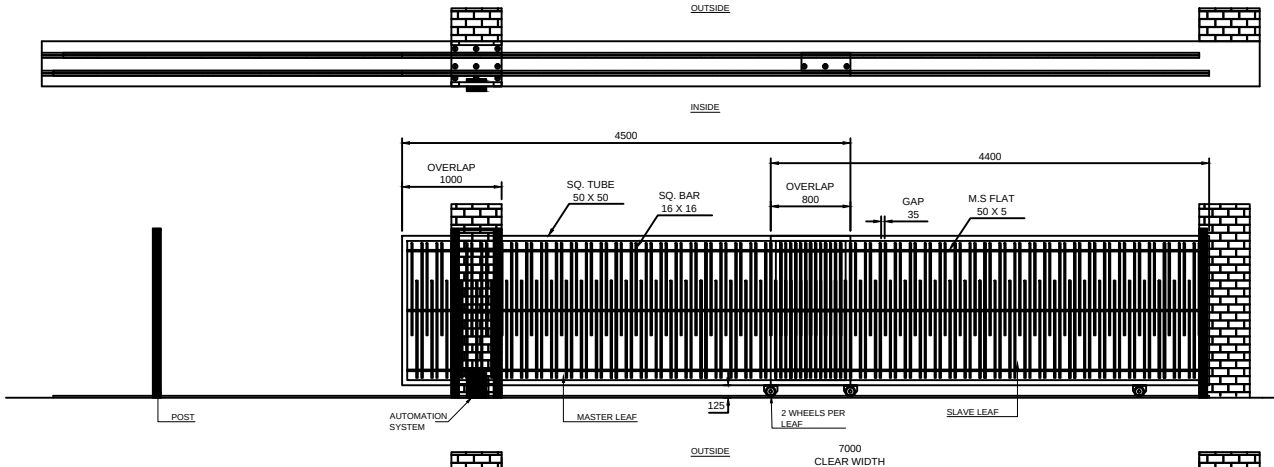

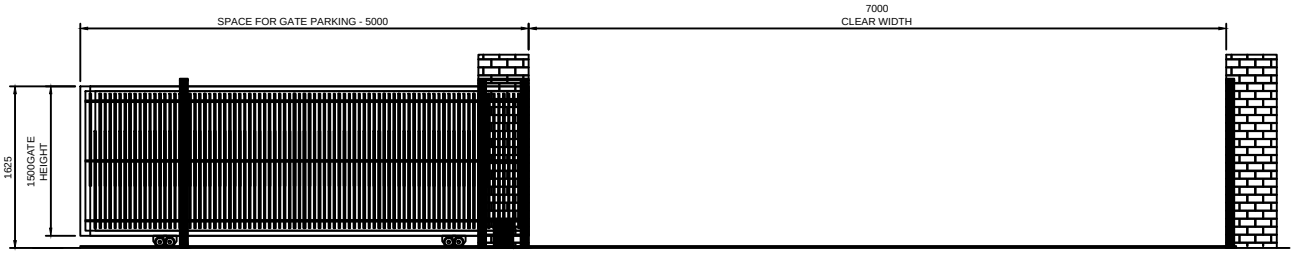

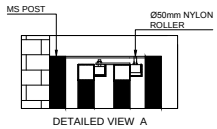

DETAILED VIEW A

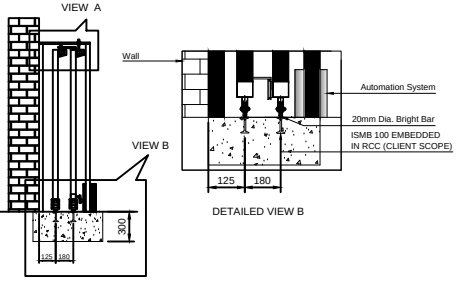

DETAILED VIEW B

R01	26.11.2019	P.A	1. GATE DESIGN CHANGE.
REV NO	REV DATE	DRAWN BY	REMARK

This drawing & designing is the property of NIHVA TECHNOLOGIES. Not to be sold or copied to any other concern.

TITLE: 2 LEAF TELESCOPIC SLIDING GATE 7000X1500mm

NIHVA TECHNOLOGIES PVT. LTD.
NIHVA TECHNOLOGIES PVT. LTD. PUNE
Tel : 020 66304033
Email:- info@nihva.com
Website :- www.nihva.com

	NAME	SIGN	DATE
DRAWN	P.A		26.11.19
CHECKED	G.J		26.11.19
APPROVED			

CLIENT - DEVI GROUP
PROJECT - CONTINENTAL
SITE LOCATION - PUNE
DWG. NO. : NIHVA/19-20/0158/R01 | REV: R01
If any queries contact : projects@nihva.com | SCALE: NTS | WT: | SHEET: 01 OF 01
ALL DIMENSION ARE IN mm