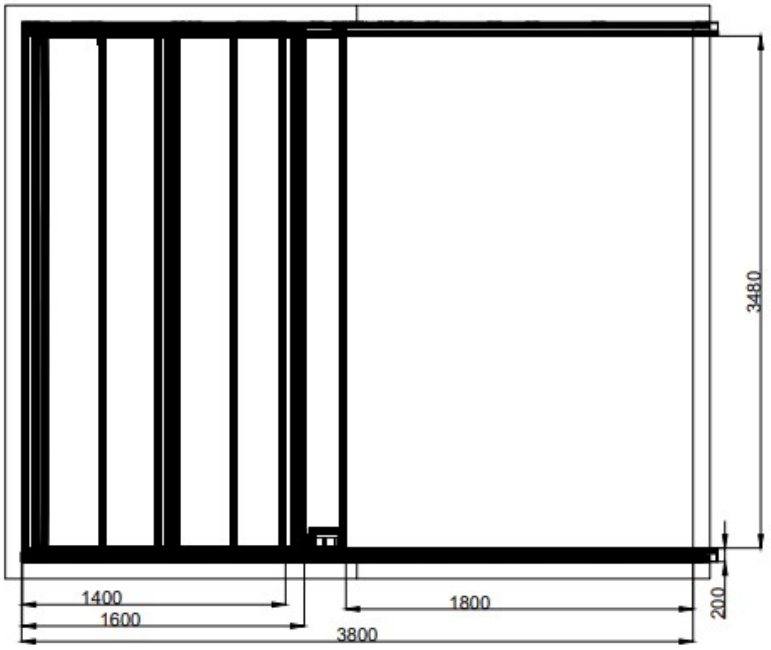
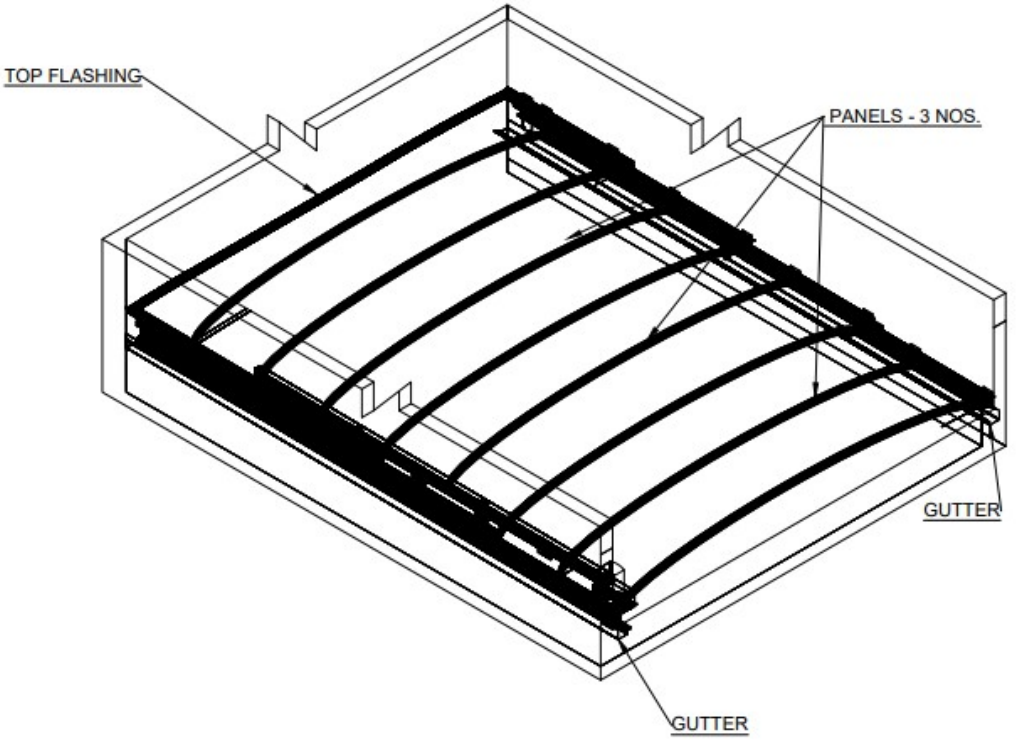
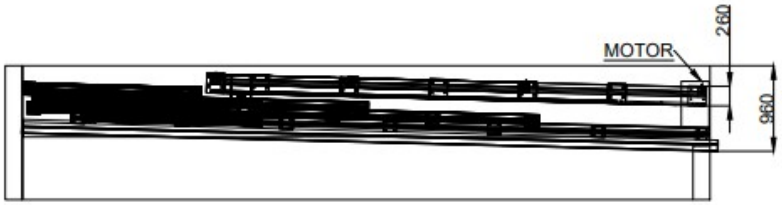
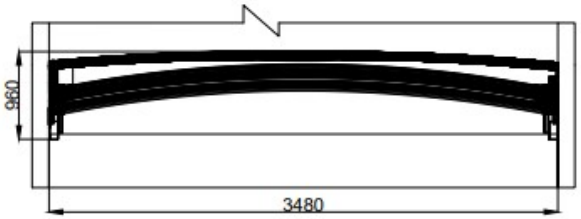



| SR NO. | PROFILE /TRACK | SIZES |
|---|---|---|
| 1 | P - 1 | 60X63XL MM |
| 2 | P - 2 | 50X50XL MM |
| 3 | P - 3 | 105X63XL MM |
| 4 | T - 4 | 105X15XL MM |
| 5 | T - 5 | 135X15XL MM |
| 6 | T - 6 | 100X60XL MM WITH Ø30 BAR |

| REV NO. | DESCRIPTION | Date | Revised By |
|---|---|---|---|
| | | | |

TITLE:- GA DRAWING

NIHVA TECHNOLOGIES PVT. LTD.

NIHVA TECHNOLOGIES PVT. LTD. PUNE
Tel : 020 66304033
Email:- info@nihva.com
Website:- www.nihva.com

| | NAME | DATE | SIGN |
|---|---|---|---|
| DRAWN | MAHESH S. | 26/12/2022 | |
| CHECK | MAHESH S. | 26/12/2022 | |
| APPRD. | VIJAY T. | 26/12/2022 | |

If any queries contact : design@nihva.com

ALL DIMENSION ARE IN mm

CLIENT - NIHVA TECHNOLOGIES PVT.LTD

LOCATION - HYDERABAD

PRODUCT: RETRACTABLE ROOF

DWG NO:-NIHVA/22-23/MFG/0048 | REV- 0

SCALE: NTS | SCALE:-- 1:1 | SHEET: 01 OF 01