
PRODUCED BY AN AUTODESK EDUCATIONAL PRODUCT

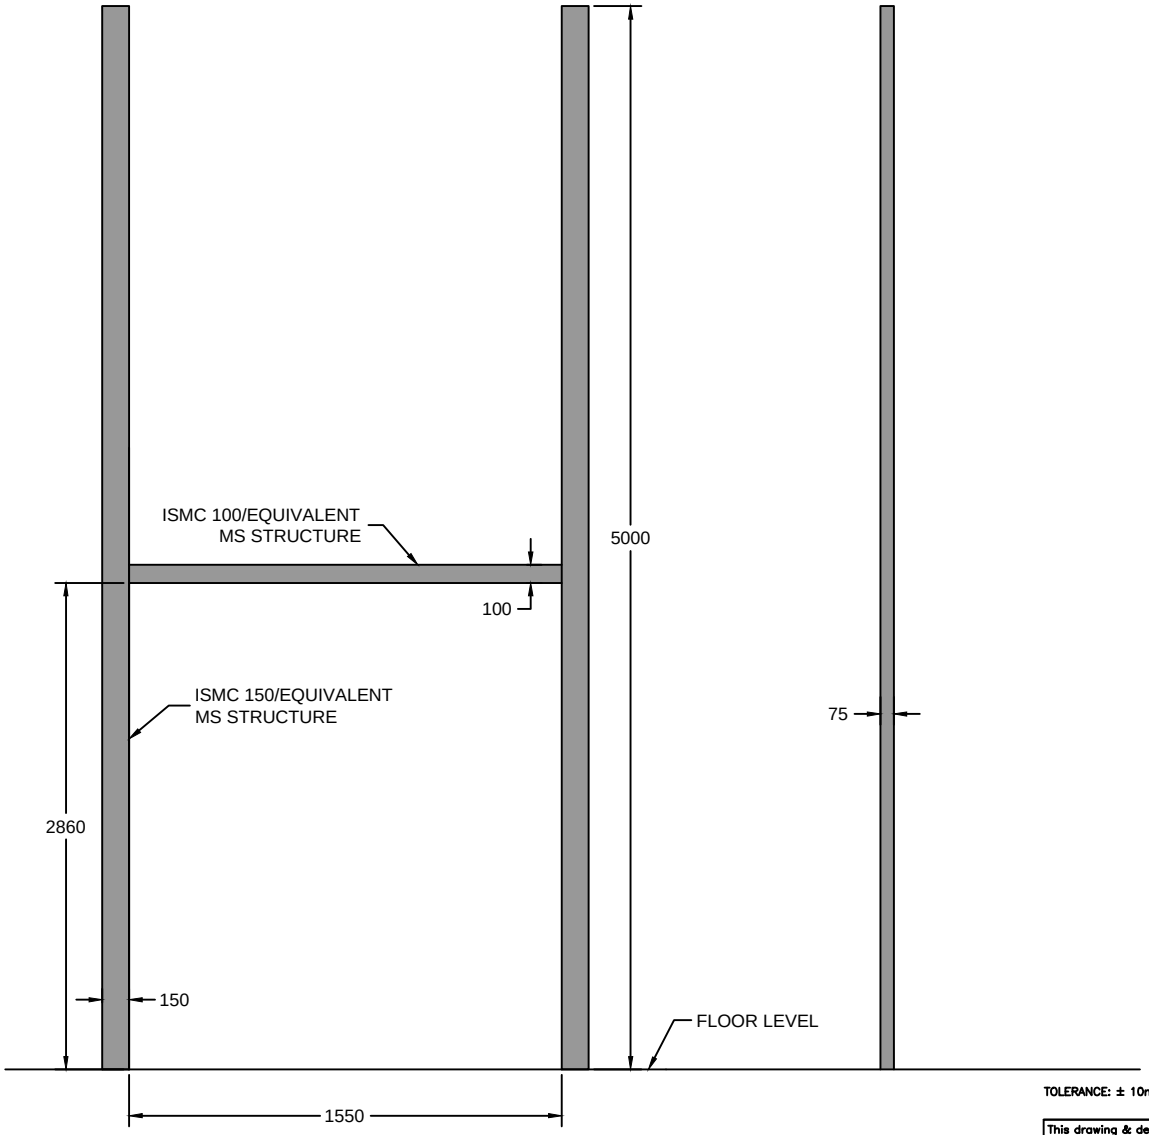

MS STRUCTURE

TOLERANCE: ± 10mm

This drawing & design is the property of NIHVA TECHNOLOGIES. Not to be sold or copied to any other concern.

TITLE			
SECTIONAL DOOR (VERTICAL LIFTING)			
	NAME	SIGN	DATE
DRAWN	P.A		16.03.20
CHECK	G.J		16.03.20
APPROVAL			
If any queries contact : design@nihva.com			
ALL DIMENSION ARE IN mm			

NIHVA TECHNOLOGIES PVT. LTD.
NIHVA TECHNOLOGIES PVT. LTD. PUNE
Tel : 020 66304033
Website:- www.nihva.com Email:- info@nihva.com

CLIENT - CREATIVE CARVE PVT.LTD.			
PROJECT -			
SITE - PUNE			
DWG. NO. : NIHVA/19-20/0242/R01			REV: R01
SCALE: NTS	WT:		SHEET: 01 OF 01

REV NO	DATE	DRAWN	REMARK
R01	11.02.20	P.A	1. CLEAR HEIGHT CHANGE

PRODUCED BY AN AUTODESK EDUCATIONAL PRODUCT

PRODUCED BY AN AUTODESK EDUCATIONAL PRODUCT