


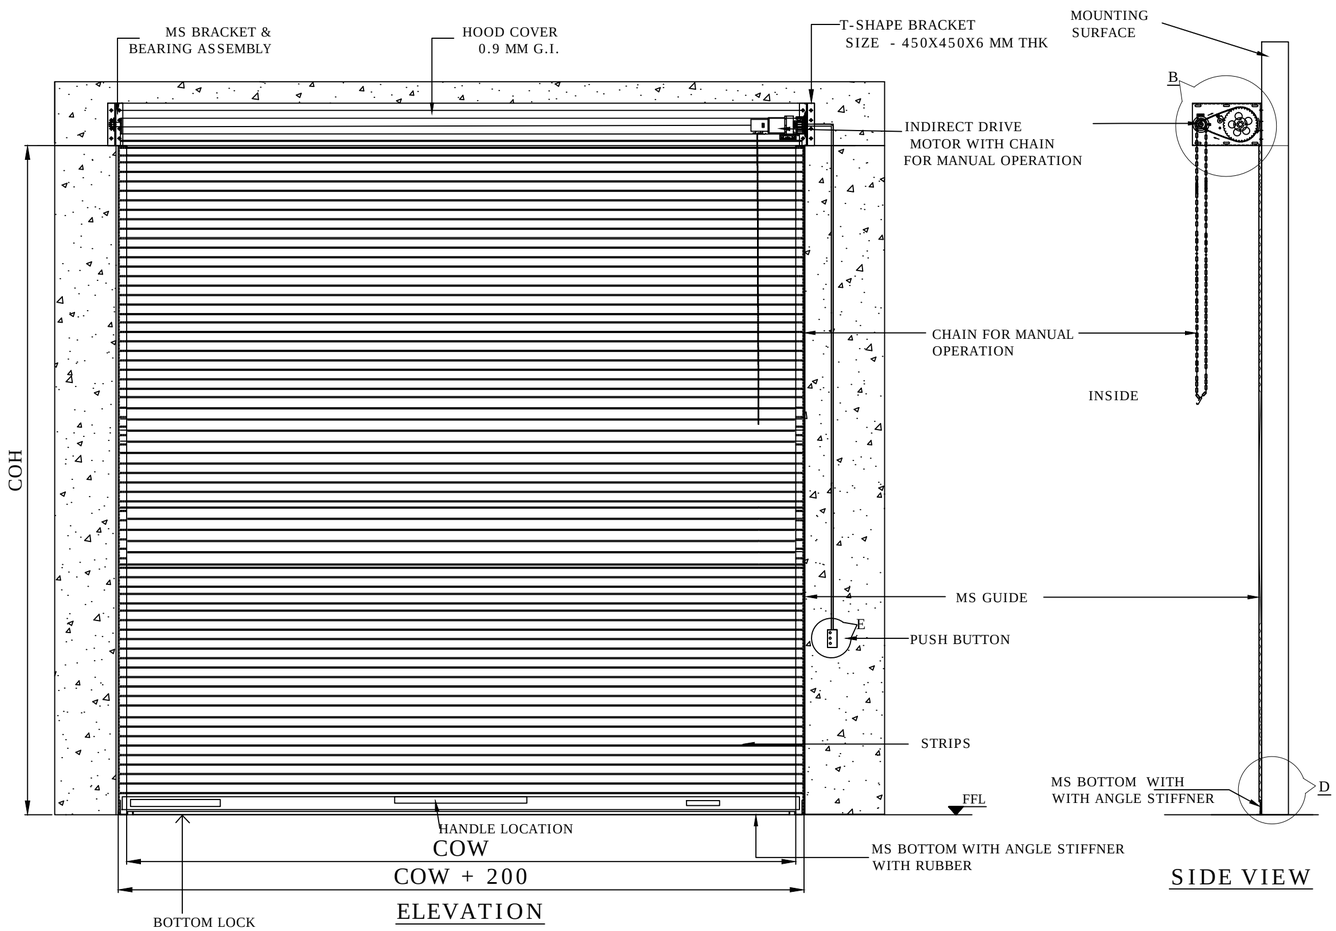


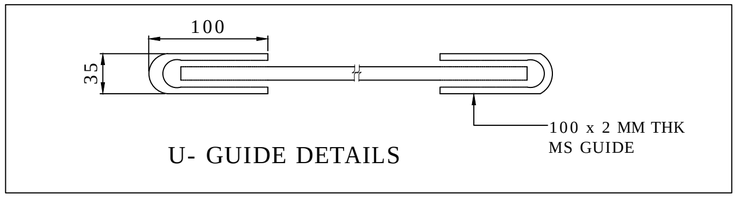


U- GUIDE DETAILS

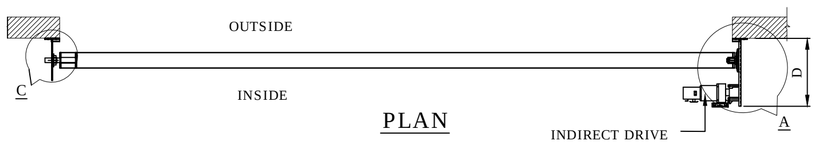


PLAN

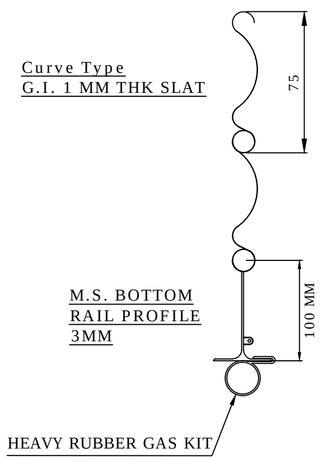

DETAILS : D

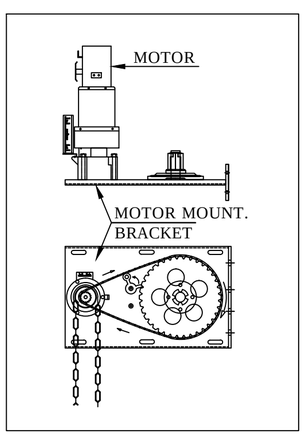

DETAILS : A & B

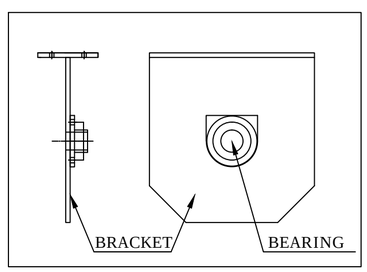

DETAILS : C

RAL SHADE FOR POWDER COATING WILL BE CONFIRMED .

1	4050	4600	1 NO	
SR NO	CLEAR OPENING WIDTH (COW)	CLEAR OPENING HEIGHT (COH)	QUANTITY	RAL COLOR POWDER COATED

This drawing & design is the property of NIHVA TECHNOLOGIES. Not to be sold or copied to any other concern.

TITLE GI MOTORIZED ROLLING SHUTTER 4050X4600

	NAME	SIGN	DATE
DRAWN	S.M.S.		14.7.2021
CHECK	A.K.		14.7.2021
APPRD.			

NIHVA TECHNOLOGIES PVT. LTD.
NIHVA TECHNOLOGIES PVT. PUNE
Tel : 020 66304033
Email:- info@nihva.com
Website:- www.nihva.com

CLIENT -

PROJECT -

SITE LOCATION -

If any queries contact :design@nihva.com

DWG. NO. : NIHVA/21-22/040/MRS/VDR

REV- R00

ALL DIMENSION ARE IN mm

SCALE: NTS

WT:

SHEET: