

OUTSIDE FTO PLOT
(MADC LAND)

SLIDING DIRECTION

LAND SIDE (OUTSIDE)

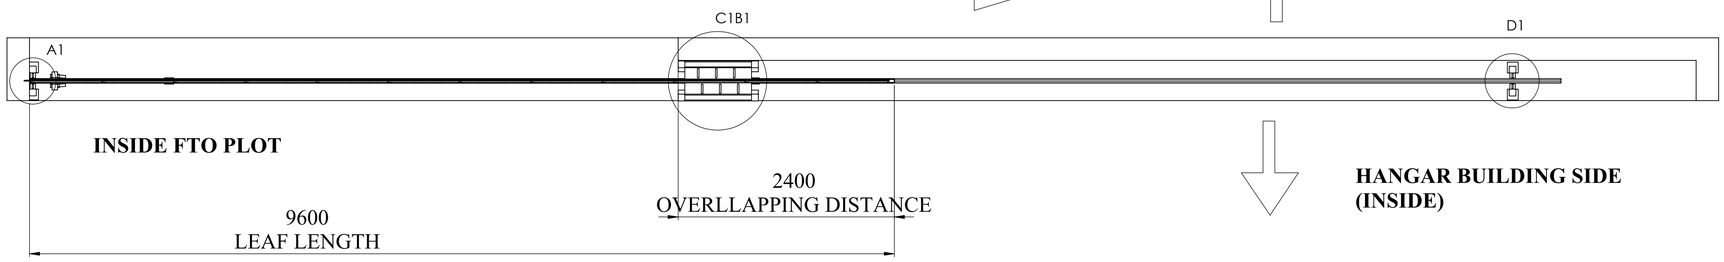


HANGAR BUILDING SIDE
(INSIDE)

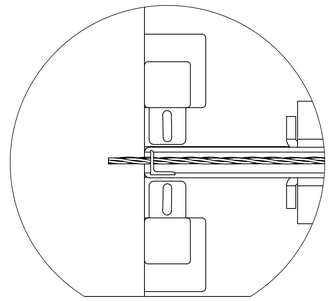


POST 1 & NYLON
ROLLER ASM

DETAIL A1
SCALE 1 : 5

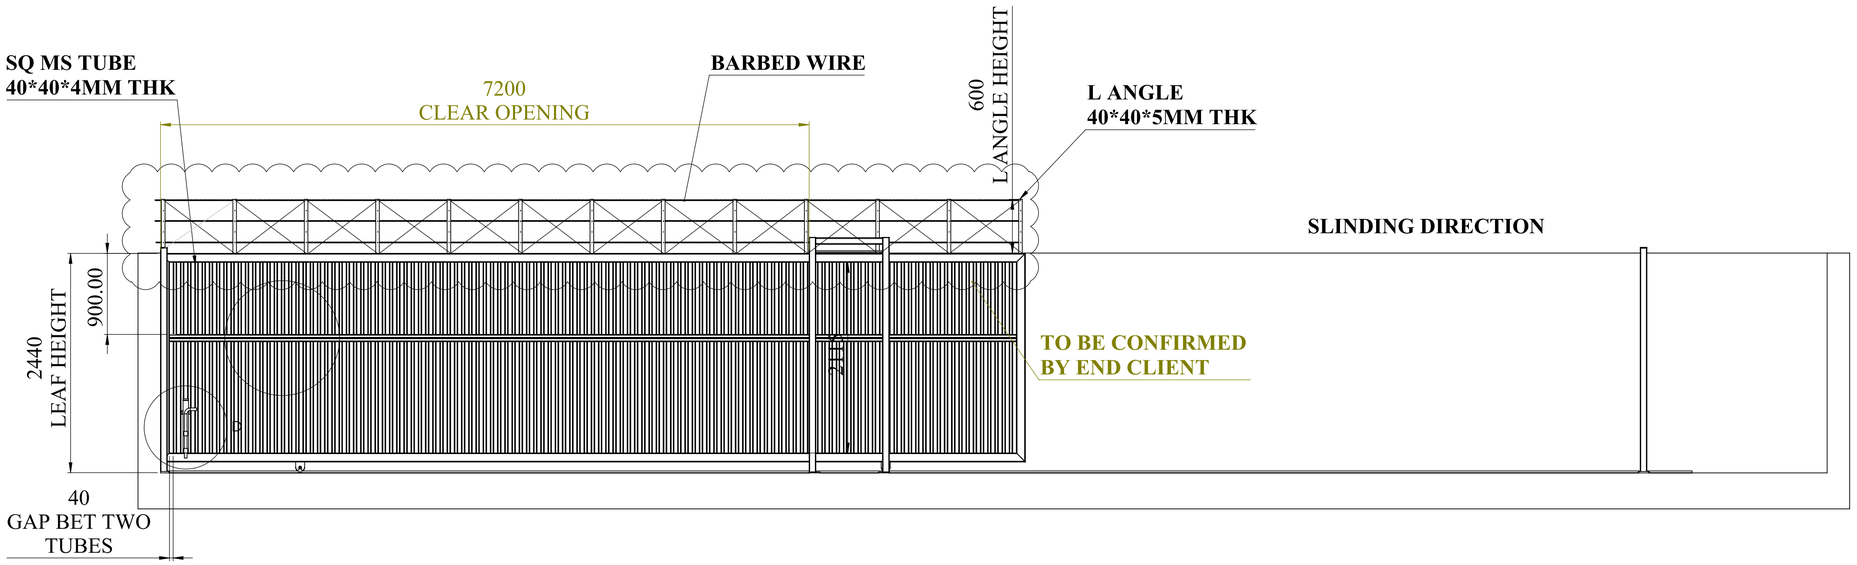


RECT MS
100MM*50*5MM THK

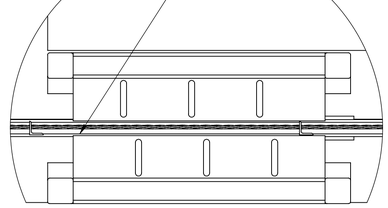


POST 2 & NYLON
ROLLER ASM

DETAIL C1B1
SCALE 1 : 9

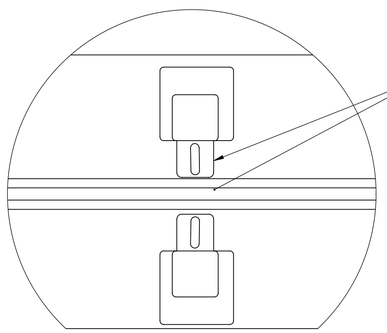


POST 3 & NYLON
ROLLER ASM

DETAIL D1
SCALE 1 : 5

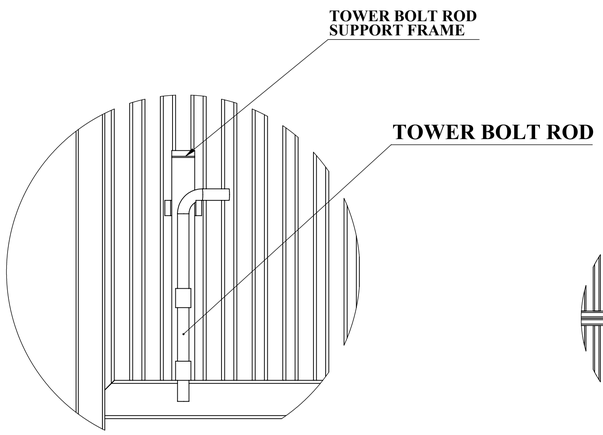

TOWER BOLT LOCKING
ARRANGEMENT

DETAIL D
SCALE 1 : 8

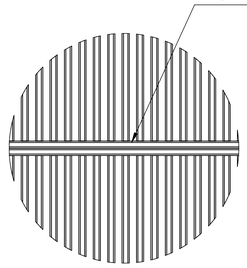

DETAIL I
SCALE 1 : 17

NOTE :

1)GA DRAWING SINGLE SLIDING GATE TYPE NO 05.
2)Total column -04 (A1,B1,C1,D1)
3) 03 column posts when the gates is in the closed position.(A1,B1,C1)
4) 03 column posts when the gates is in the fully open position.(B1,C1,D1)
5) barbed wire design is zigzag pattern.

UNLESS OTHERWISE SPECIFIED: DIMENSIONS ARE IN MILLIMETERS SURFACE FINISH: TOLERANCES: LINEAR: ANGULAR:	FINISH:		DEBURR AND BREAK SHARP EDGES	DO NOT SCALE DRAWING	REVISION
	NAME	SIGNATURE	DATE	TITLE:	
DRAWN				GA DRAWING TYPE 05	
CHK'D					
APPV'D					
MFG					
Q.A				DWG NO.	01
MATERIAL:					
WEIGHT:				SCALE:1:100	SHEET 1 OF 1