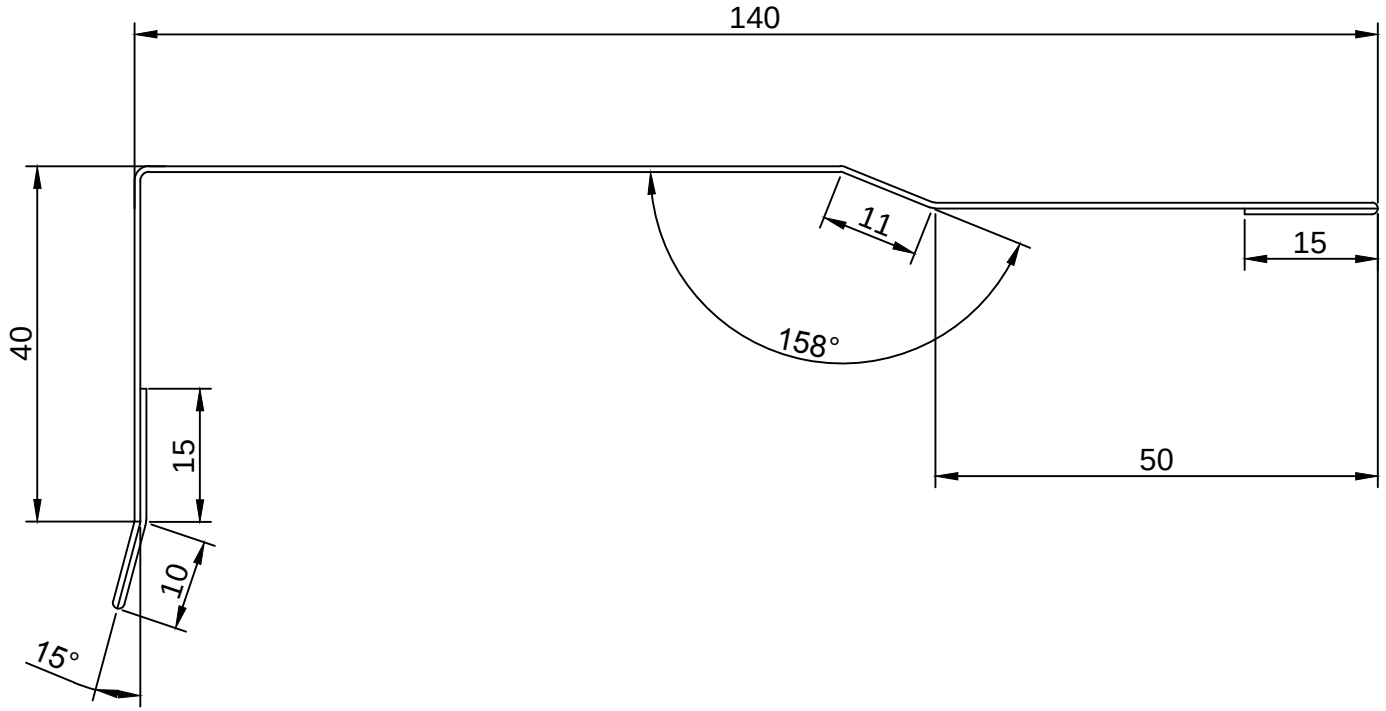


DEVELOPMENT SIZE:
1. 3560 X 230 X 0.65- 44 NOS
2. 2410 X 230 X 0.65- 22 NOS

MATERIAL : GI/ MS
THK : 0.65 MM
POWDER COATING : RAL 9001

This drawing & designing is the property of NIHVA TECHNOLOGIES. Not be sold or copy to any other concern.

TITLE: DOOR SUPPORT CHANNEL			NIHVA TECHNOLOGIES PVT. LTD.
	SIGN	DATE	
DRAWN	G.P.	31.8.2021	CLIENT -
CHECK	A.K.	31.8.2021	PROJECT - DOOR SUPPORT CHANNEL
APPROVAL	V.T.	31.8.2021	SITE -
REV.	00		DWG. NO. : NIHVA/21-22/0224
If any queries contact : design@nihva.com			SCALE: NTS | WT: | SHEET: 01 OF 01
ALL DIMENSION ARE IN mm			

NIHVA TECHNOLOGY PVT. LTD. PUNE
Tel : 020 66304033
Email:- info@nihva.com
Website:- www.nihva.com