
REV.	DESCRIPTION.	REVISED BY	SIGN	DATE
000	RELEASED GA DWG FOR APPROVAL	MAHESH S.		30.11.22
001	MODIFIED GA DWG PER SITE CHANGES	MAHESH S.		30.12.22

PROPOSED PLAN LAYOUT

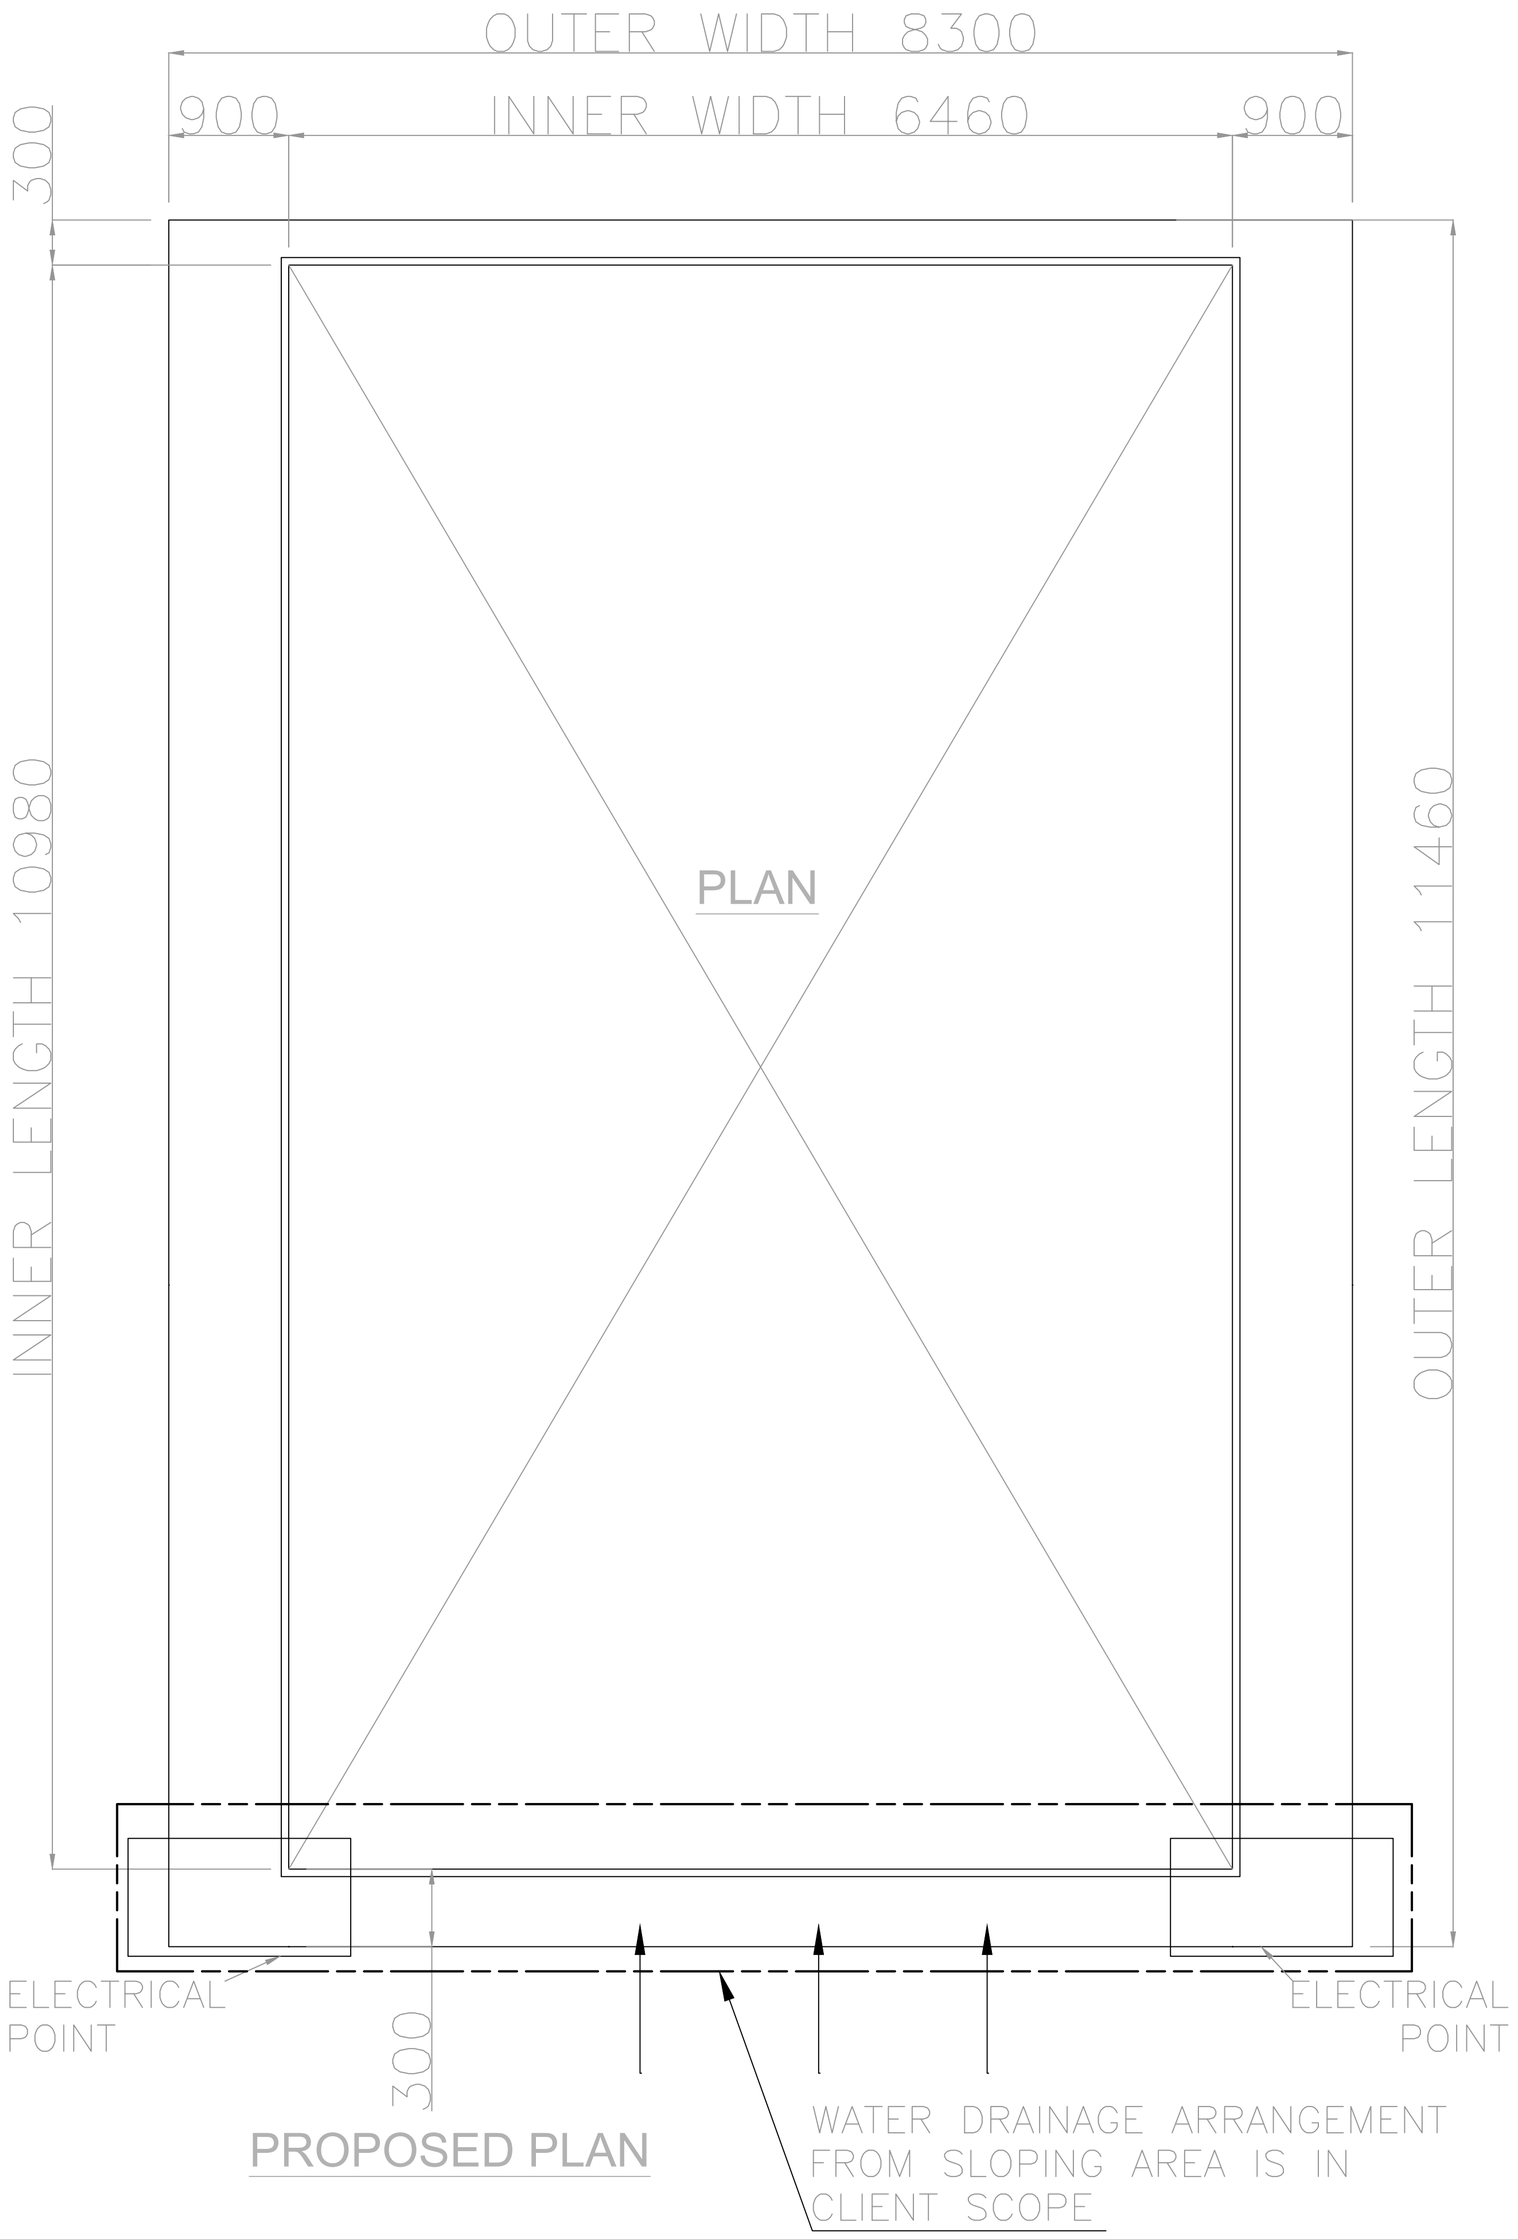

PROPOSED PLAN



SECTION VIEW

1. THE STRUCTURE AROUND THE CUT OUT SHOULD BE OF CONCRETE FOR FOR PROPER FASTENING OF ROOF.
2. TOP SURFACE SHOULD BE OF GRANITE 20MM FOR SMOOTH FUNCTIONING OF ROOF.
3. ROOF EXTENSION IS SHOWN FOR ONLY REFERENCE. IT CAN BE MODIFIED AS PER THE WORK UNDERTAKEN.
4. GRADIENT OF 80MM NEED TO BE PROVIDED ALONG THE OUTER LENGTH TO AVOID WATER STAGNANCY IN GUIDE RAIL.
5. AL PROFILE - POWDER COATED
6. GASKET - EPDM
7. MOTOR - ITALIAN/GERMAN MAKE
8. ELECTRICAL REQUIREMENT - .
9. ALL DIMENSION IN MM.
10. ALL CIVIL WORK IS IN CLIENT SCOPE

This drawing & design is the property of NIHVA TECHNOLOGIES. Not to be sold or copied to any other concern.

TITLE
PROPOSED PLAN LAYOUT
(IN CLIENT SCOPE)

	NAME	SIGN	DATE
DRAWN	MAHESH S.		30.11.22
CHECK	MAHESH S.		30.11.22
APPRD.	VIJAY T.		30.11.22

NIHVA
NIHVA TECHNOLOGIES PVT. LTD.

CLIENT - MR. MANISH SHAHA
LOCATION - AHMEDABAD_IN
PRODUCT - RETRACTABLE ROOF

If any queries contact : projectsautomation@nihva.com
NIHVA\22-23\02XX
REV- 0
ALL DIMENSION ARE IN mm
SCALE: NTS
SHEET: 01 OF 01