

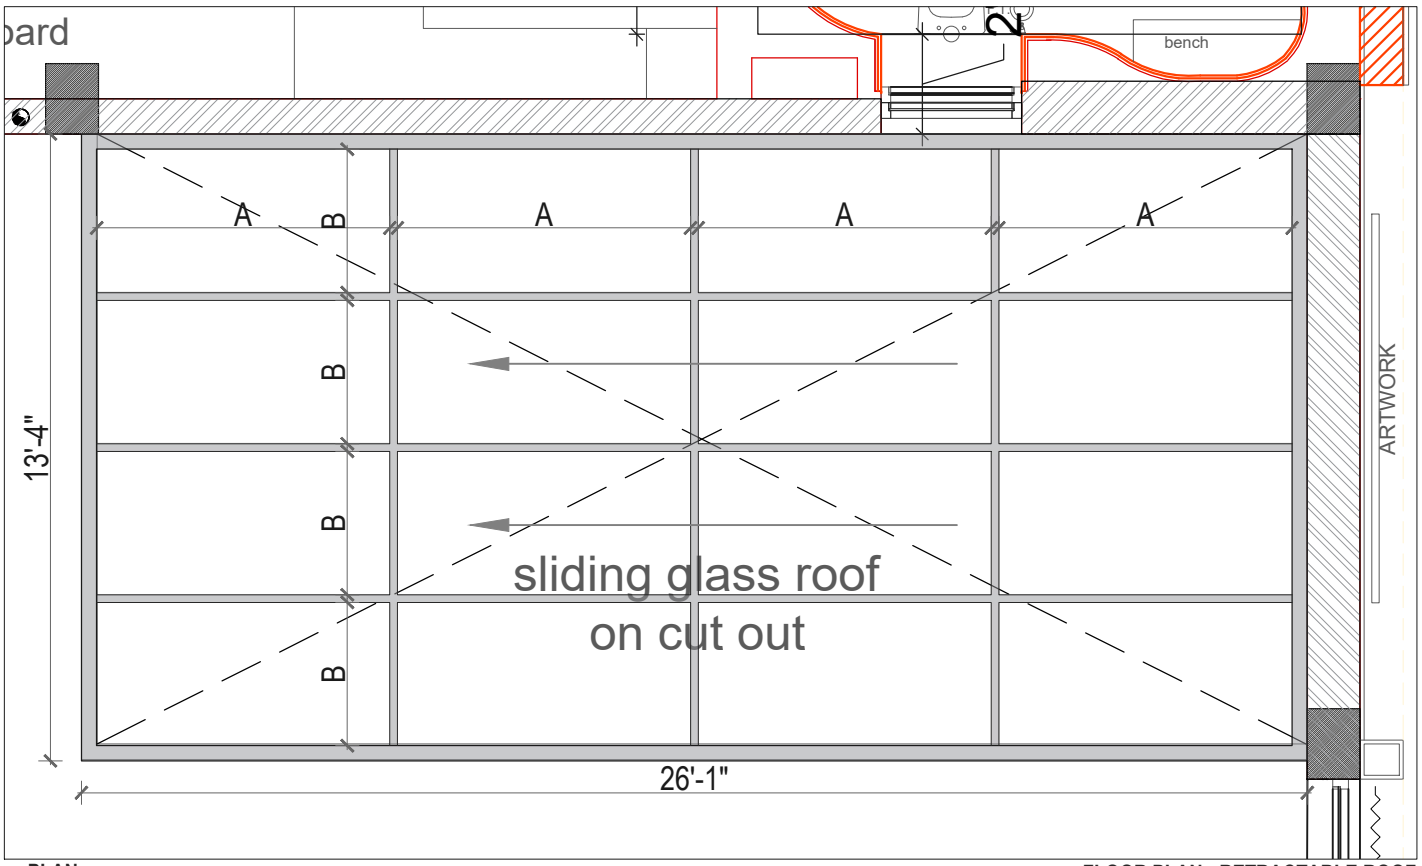


PLAN

FLOOR PLAN : RETRACTABLE ROOF

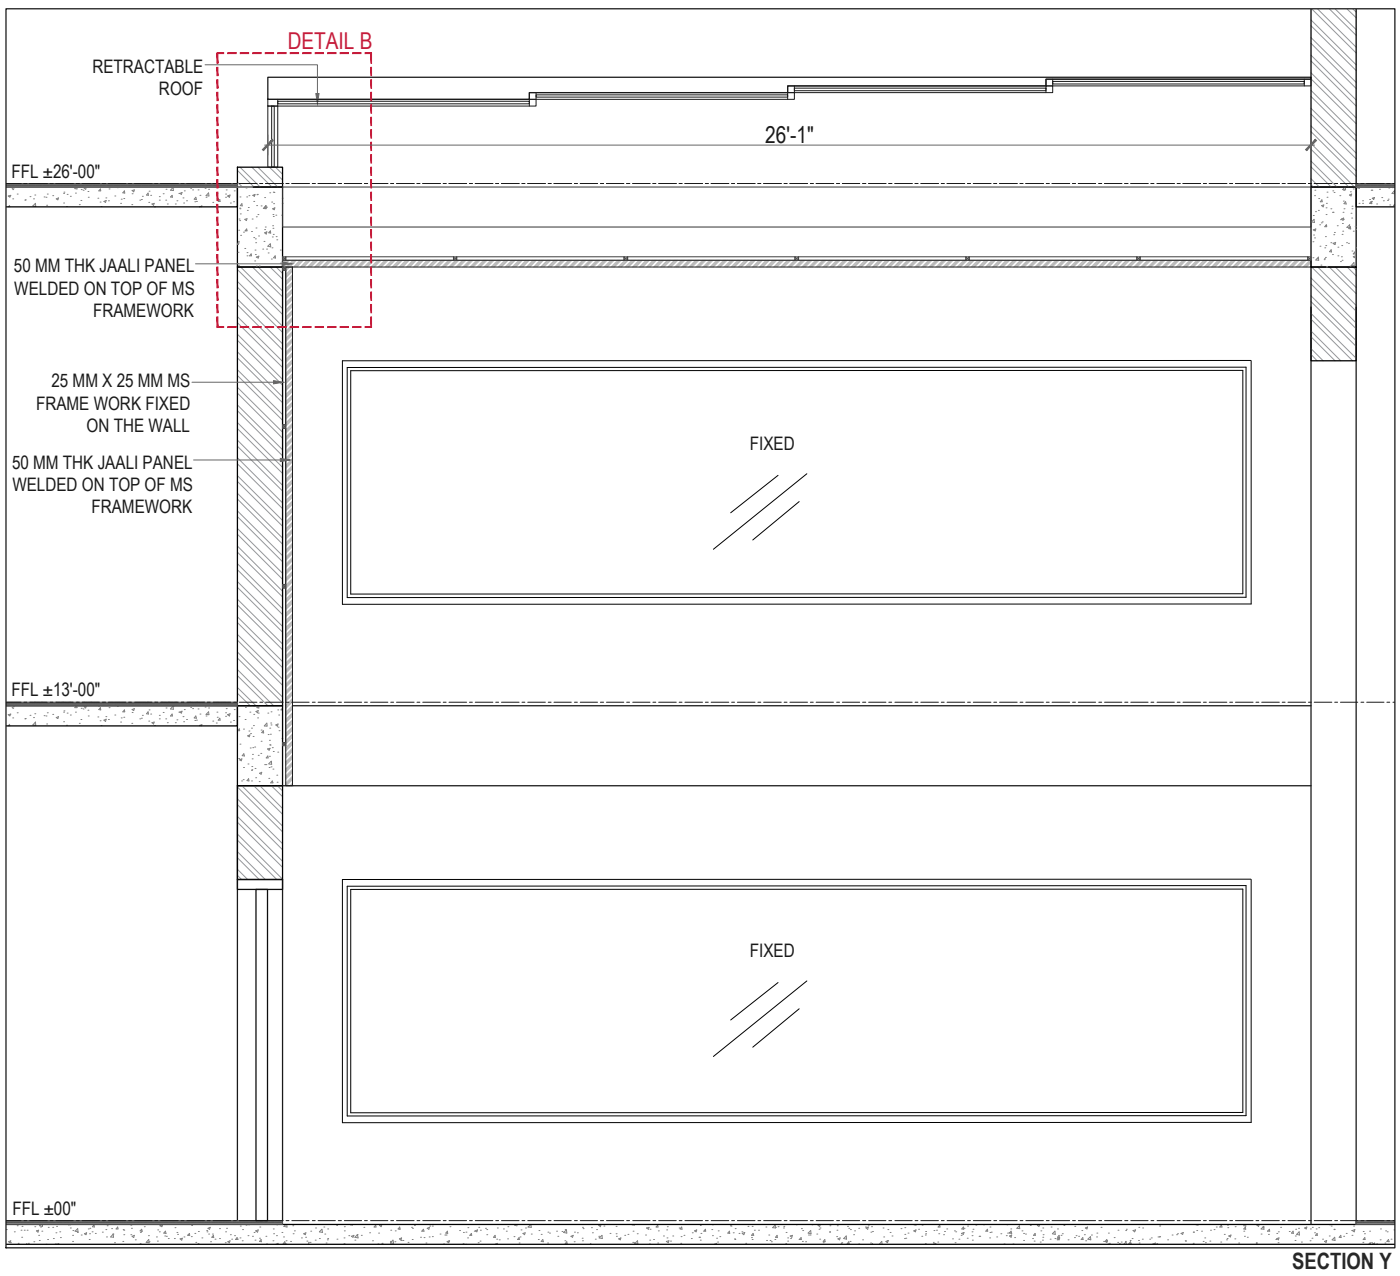

SECTION Y

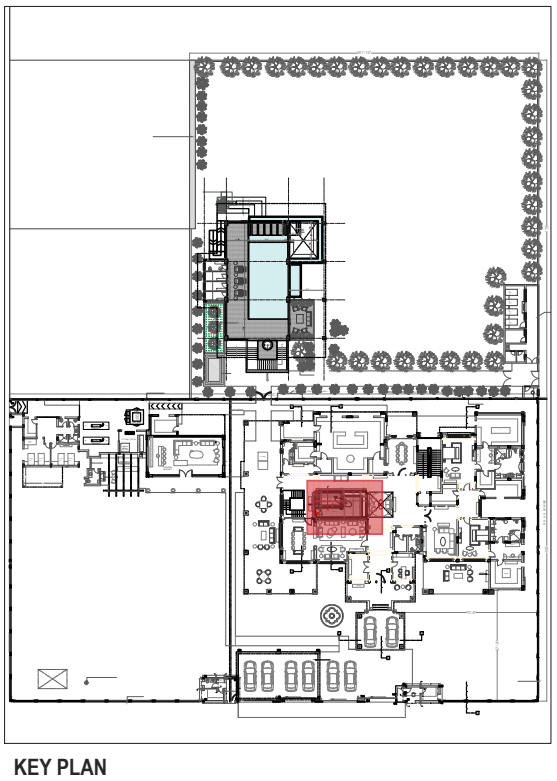

KEY PLAN

PROJECT	CLIENT	ARCHITECTS	TECHNICAL CONSULTANTS
VIKAS LUDHIANA		STUDIO BIPOLAR	STRUCTURE CONSULTANT

REVISIONS

REV.	DATE	DESCRIPTION
R0	XX.YY.ZZ	DRAWING FIRST ISSUED

DRAWING TITLE
COURTYARD DETAILS

DRAWN	APPROVED	SCALE	DRAWING NO.	DATE
SJ	JS	NTS	GAD / WD / A / 100 / R0	14.02.22

THIS DRAWING IS THE PROPERTY OF THE ARCHITECT AND IS NOT TO BE COPIED / REPRODUCED WITHOUT PRIOR PERMISSION.