

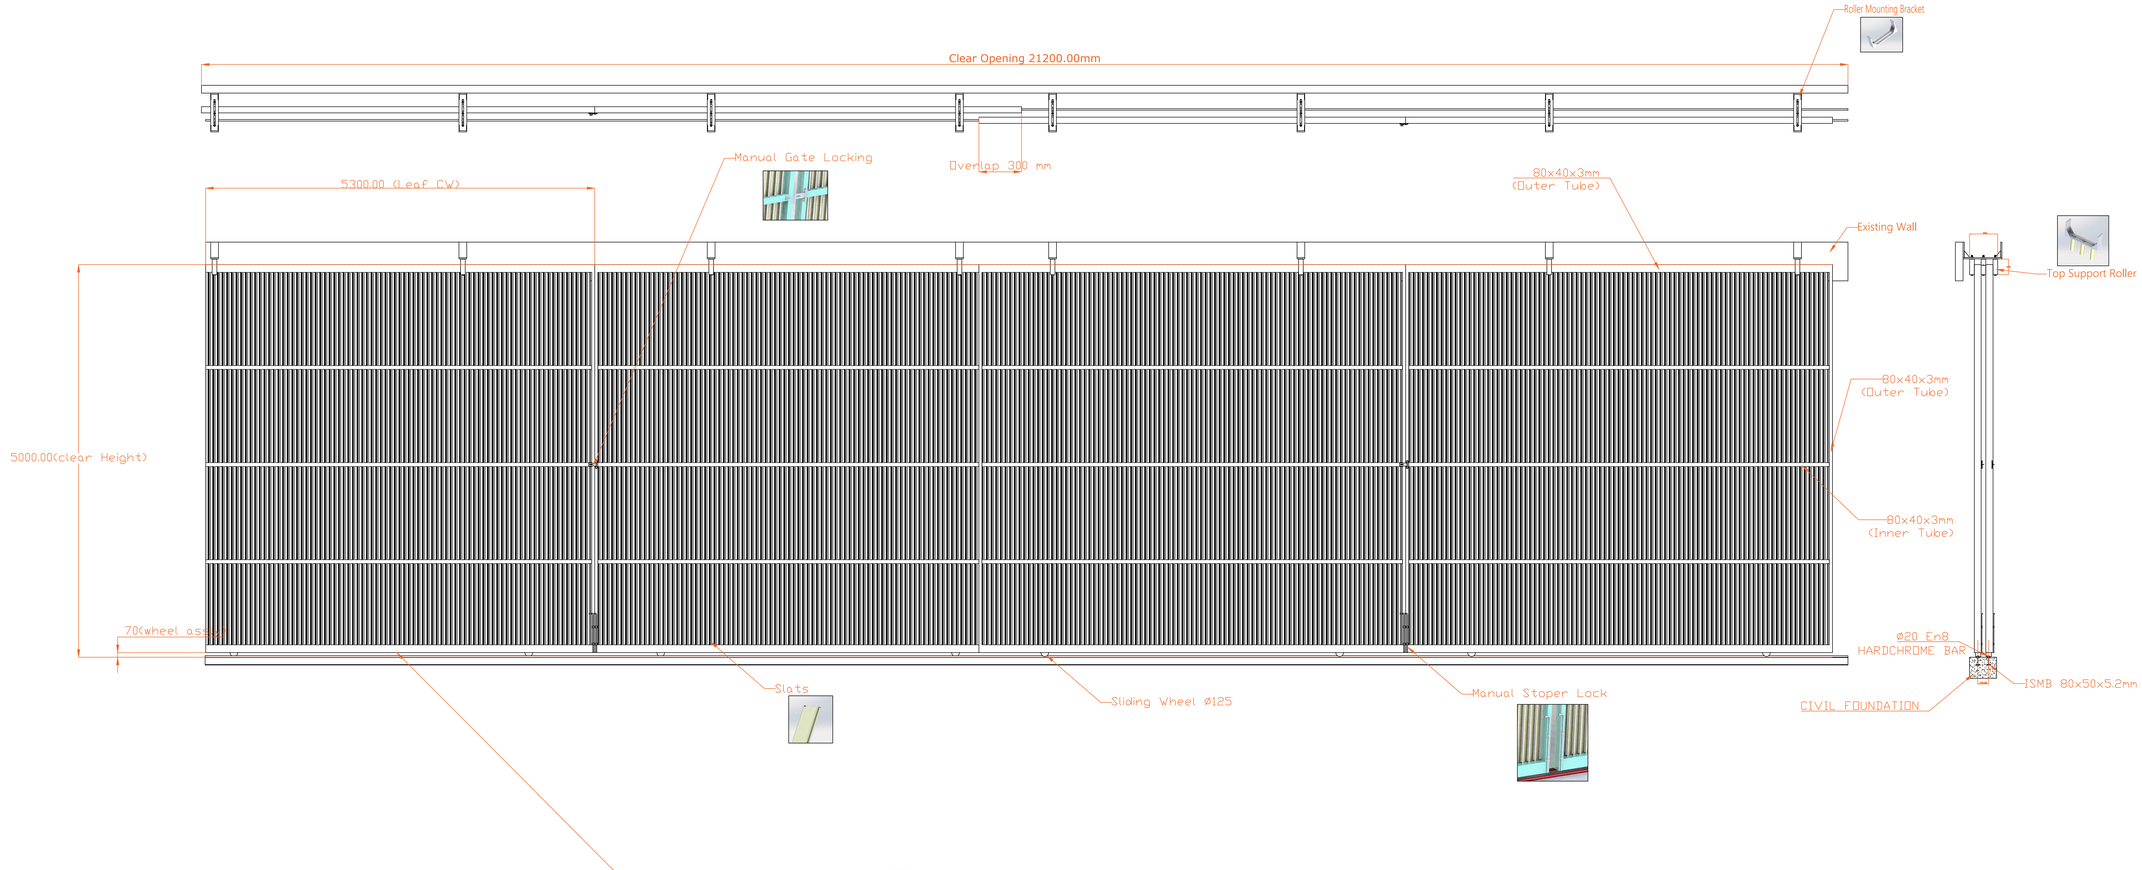


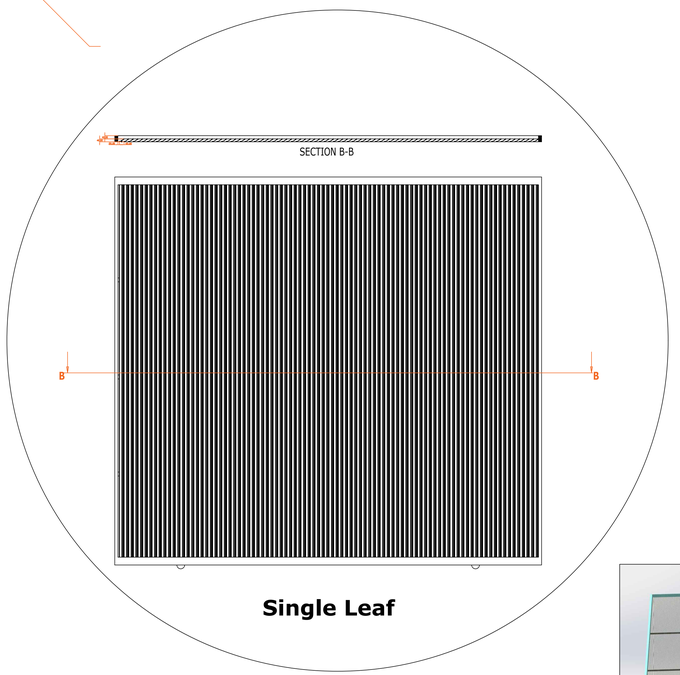

Single Leaf

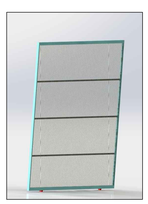

Shown GA IS ONLY FOR 2 LEAFS

TECHNICAL SPECIFICATION:-

SR.	SPECIFICATION	DETAILS
1.	Description & Drive	Manual Operated Sliding Gate
2.	Slat	Curved 80 mm GI Sheet - 1.0 mm Thk.
3.	Leaf Size	5300 mm x 4950 mm= 14 qty
4.	Overlap	Overlap considered 300 mm between 2 gates

This drawing & designing is the property of NIHVA TECHNOLOGIES. Not to be sold or copied to any other concern.

TITLE :-
Manual Sliding Gate

NIHVA TECHNOLOGIES PVT. LTD. PUNE
Tel : 020 66304033
Email:- info@nihva.com
Website:- www.nihva.com

	NAME	DATE
DRAWN	S.J	23/02/2024
CHECK	A.K.	23/02/2024
APPROVAL	V.T.	23/02/2024

CLIENT - Panchashil
PROJECT - Manual Sliding Gate
FORMAT NO - NIHVA-DD-F-03
DWG. NO. : NIHVA/23-24/XX | REV-00
SCALE: NTS | WT: | SHEET: 01 OF 01
ALL DIMENSION ARE IN mm
If any queries contact : design@nihva.com