


WEST ELEVATION OF MATERIAL ENTRY GATE ENTRANCE.

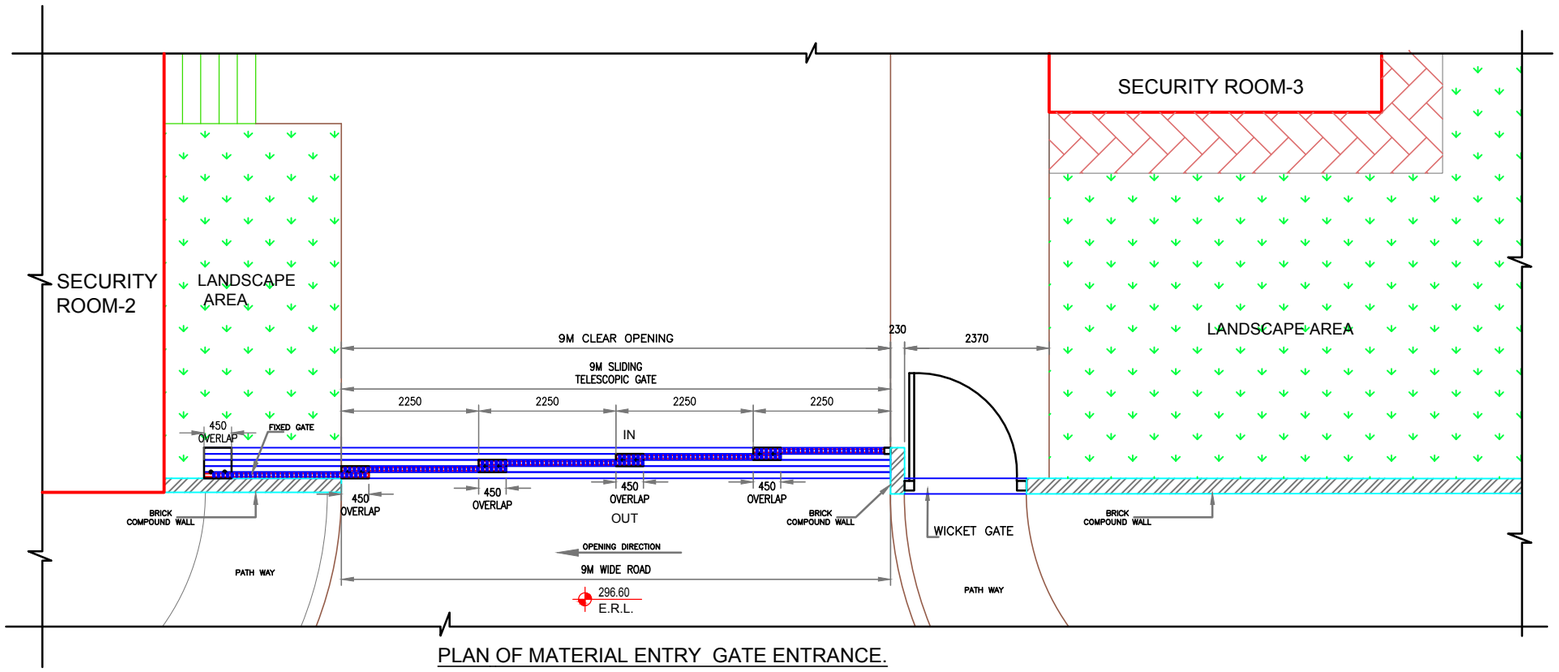

PLAN OF MATERIAL ENTRY GATE ENTRANCE.

ips INTERNATIONAL

Integrated Project Services

Engineering
Design
Site Supervision
Consulting

C-1,C-Block, Community Centre, Naraina Vihar
New Delhi - 110 028


+91-11-25777806 phone
+91-11-25779089 phone
+91-11-25779152 phone
www.ipsintl.net

REVISION	DATE	DESCRIPTION	BY
R0	14AUG17	NEW DRAWING	SJ

NOTE :
FGL. FINISHED GROUND LEVEL
FFL. FINISHED FLOOR LEVEL
TOC. TOP OF CONCRETE
BRICK WALL

FOR COMMENTS AND APPROVAL

KEY PLAN

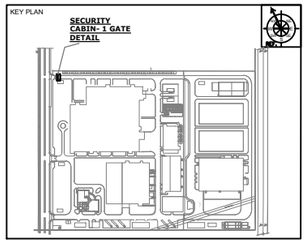

CONFIDENTIAL

THE INFORMATION CONTAINED HEREIN MAY NOT BE USED OR REPRODUCED IN ANY MANNER WITHOUT WRITTEN PERMISSION OF INTEGRATED PROJECT SERVICES.

CLIENT

LUPIN LIMITED
MIHAN NAGPUR

Lupin Ltd.

DRAWING TITLE

OSD BLOCK
SECURITY CABIN 3
MATERIAL ENTRY GATE DETAIL

ENGINEER	ARCHITECT	DESIGNER
	SK	
DRAWN BY	REVIEWED BY	SCALE
SJ	PNP	1:50

RECORDS CONTROL

IPS #	DRAWING NUMBER	
14-1095/96	IPS-14-1095/96-AR-A11	
XREF FILE(S)		
CADD FILE #	PAPER SIZE: A1	REV.