

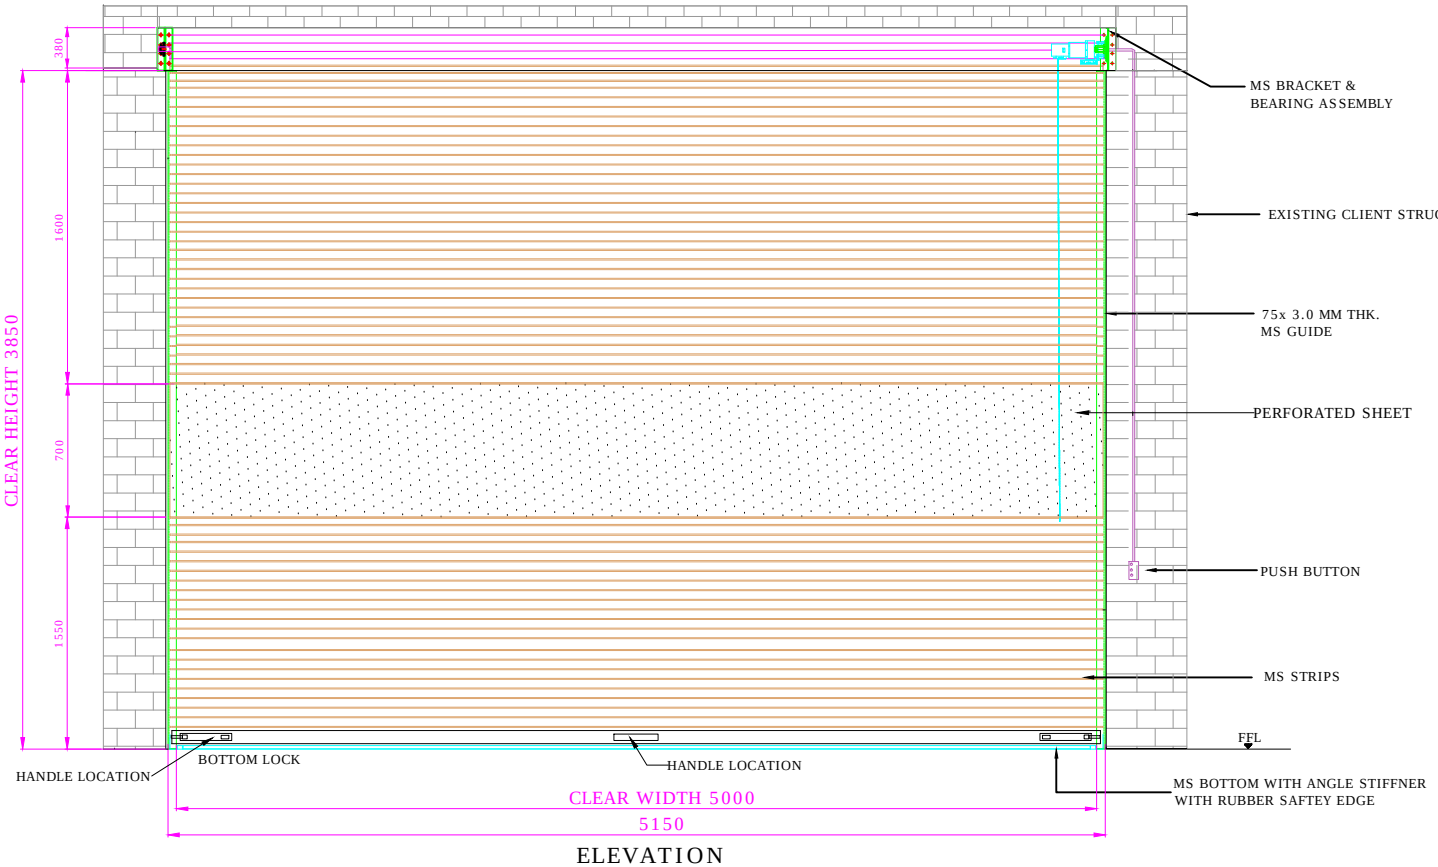



ELEVATION

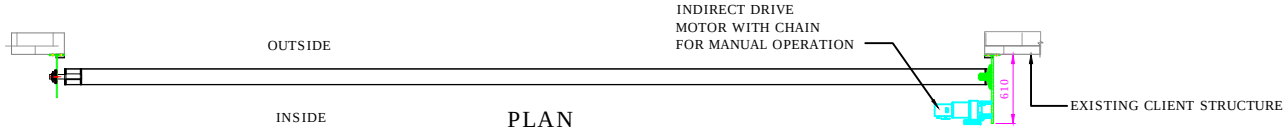

PLAN

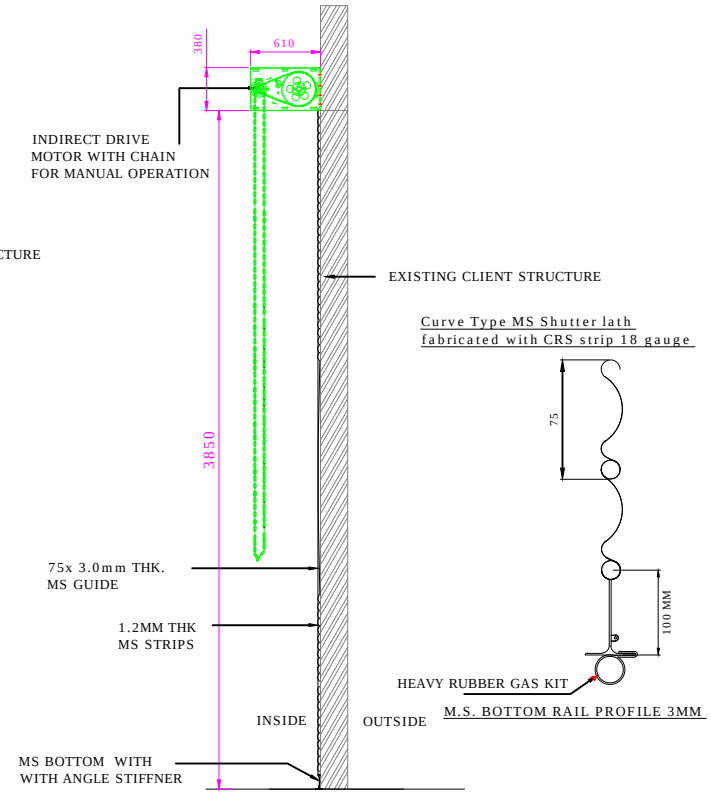

SIDE VIEW

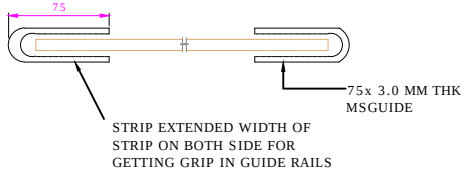

CLEAR OPENING : 5000X3850
QTY.: 1NOS.

Clear opening Dimensions	
Width (w) :-	5000 mm
Height (h) :-	3850 mm
Motor Position	
Left :-	Right :- ✓

TITLE

MOTORIZED ROLLING SHUTTER

CLIENT APPROVAL

This drawing & designing is the property of NIHVA TECHNOLOGIES. Not be sold or copy to any other concern.

ALL DIMENSION ARE IN mm

	SIGN	DATE
DRAWN	ABHIJIT	04/03/15
CHECK	ANIL	04/03/15
REV.	03	
APPRD.		
MFG		
Ref. No.		

NIHVA TECHNOLOGIES PVT. LTD.
NIHVA TECHNOLOGY PVT. LTD. PUNE
Tel : 020 66304033
Email:- info@nihva.com
Website:- www.nihva.com

CLIENT - NYATI ENGINEERS & CONSULTANT
PROJECT -ELRING KLINGER
SITE -PLOT NO.G2, MIDC, RANJANGAON
DWG. NO. - NVA/NYATI/D1/01
SCALE: 01 | WT: | SHEET: 01 OF 02
If any queries contact : projects@nihva.com