




5mm THK.
CHEQUERED PLATE

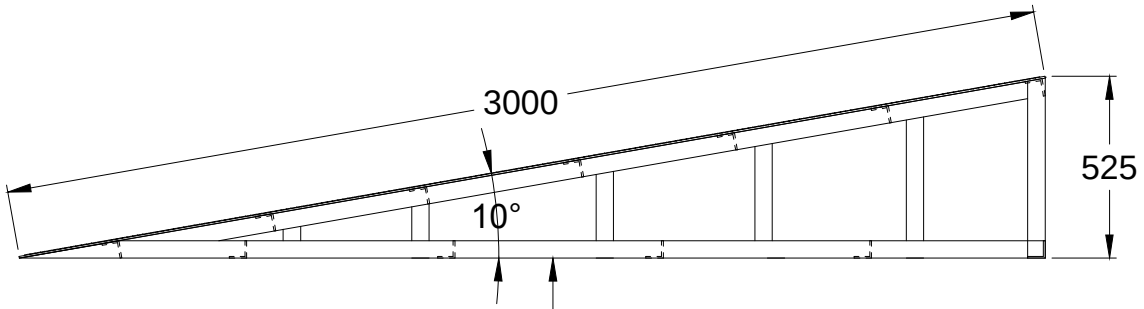

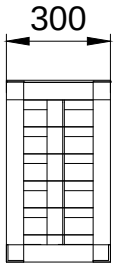

50X50X5mm MS ANGLE
STRUCTURE

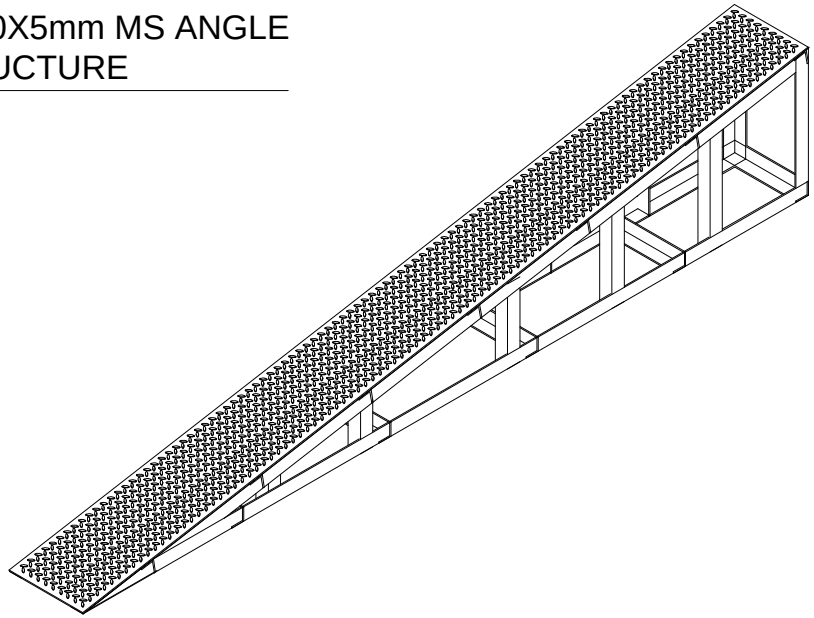

DIMENSION :		
CLEAR WIDTH	CLEAR HEIGHT	QUANTITY
MATERIAL :		
THICKNESS :		
TOLERANCES- ±10mm		

NIHVA TECHNOLOGIES PVT. LTD.

NIHVA TECHNOLOGY
PVT. LTD. PUNE
Email:- info@nihva.com
Website:- www.nihva.com

TITLE:

FIXED LOADING RAMP

CLIENT'S APPROVAL :		
CLIENT - HYOSUNG T&D INDIA PVT. LTD.		
PROJECT -		
SITE LOCATION - KHED CITY		
DWG. NO. : NIHVA/16-17/116		
SCALE: NTS	WT:	SHEET:1 OF 1
DRAWN BY: OMKAR		DATE: 26-12-2016
CHECK : SAGAR P.		DATE: 26-12-2016
APPROVED BY : R.K.		DATE: 26-12-2016
If any queries contact : projects@nihva.com		
NOTE: ALL DIMENSION ARE IN mm		

THIS DRAWING & DESIGNING IS THE PROPERTY OF NIHVA TECHNOLOGIES. NOT BE SOLD OR COPY TO ANY OTHER CONCERN.