
# LOCATION AREA :- SEZ 1 C - FIRST FLOOR- ENTRY

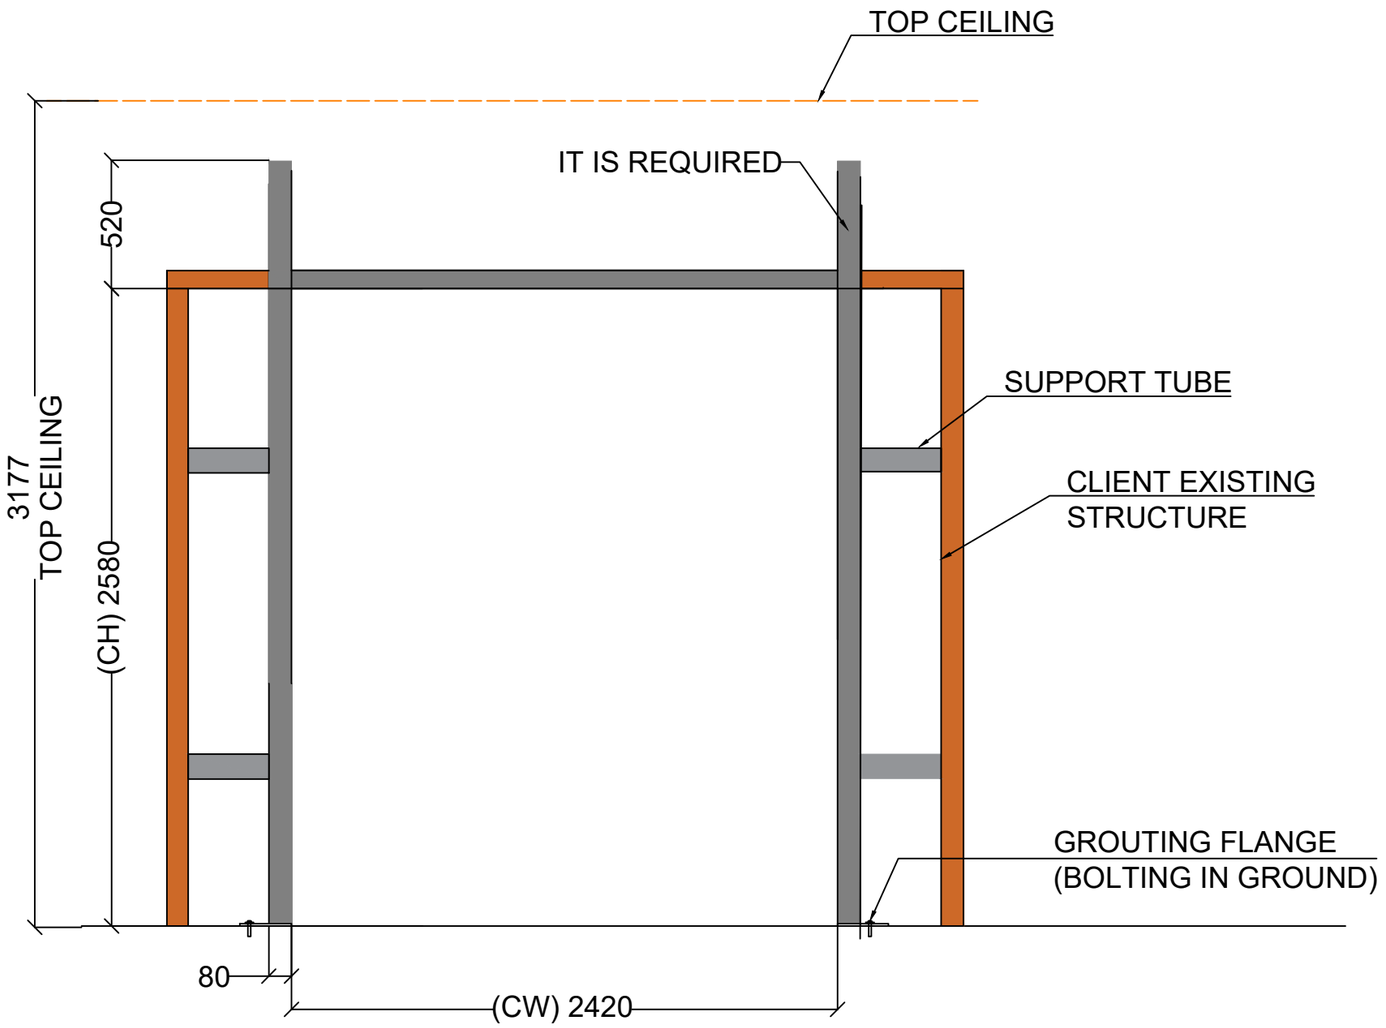


NOTE :-

1. ALL DIMENSIONS ARE IN MM
2. THIS DRAWING IS SOLELY MEANT TO BE UNDERSTOOD.
3. REQUIRED HEIGHT & ACTUAL HEIGHT PLEASE CONFIRM BY CLIENT

## M.S. STRUCTURE DETAILS

| Clear Width (CW) | Clear Height (CH) | QTY |
|---|---|---|
| **2420** | **2580** | 01 |

This drawing & design is the property of NIHVA TECHNOLOGIES. Not to be sold or copied to any other concern.

| TITLE:- HIGH SPEED DOOR STRUCTURE DRAWING | | | | NIHVA TECHNOLOGIES PVT. LTD. PUNE<br>Tel : 020 66304033<br>Email:- info@nihva.com<br>Website:- www.nihva.com |
|---|---|---|---|---|
| | NAME | SIGN | DATE | |
| DRAWN | S.J | | 14.11.2024 | CLIENT - SERUM INSTITUTE OF INDIA PVT.LTD |
| CHECK | S.W. | | 14.11.2024 | PROJECT - HIGH SPEED DOOR ST. |
| APPRD. | V.T | | 14.11.2024 | FORMAT NO - NIHVA-DD-F-03 |
| If any queries contact : projectsupport@nihva.com | | | | DWG. NO. : NIHVA/24-25/SM/24100301 / REV- R00 |
| ALL DIMENSION ARE IN mm | | | | SCALE: NTS / WT: / SHEET: |