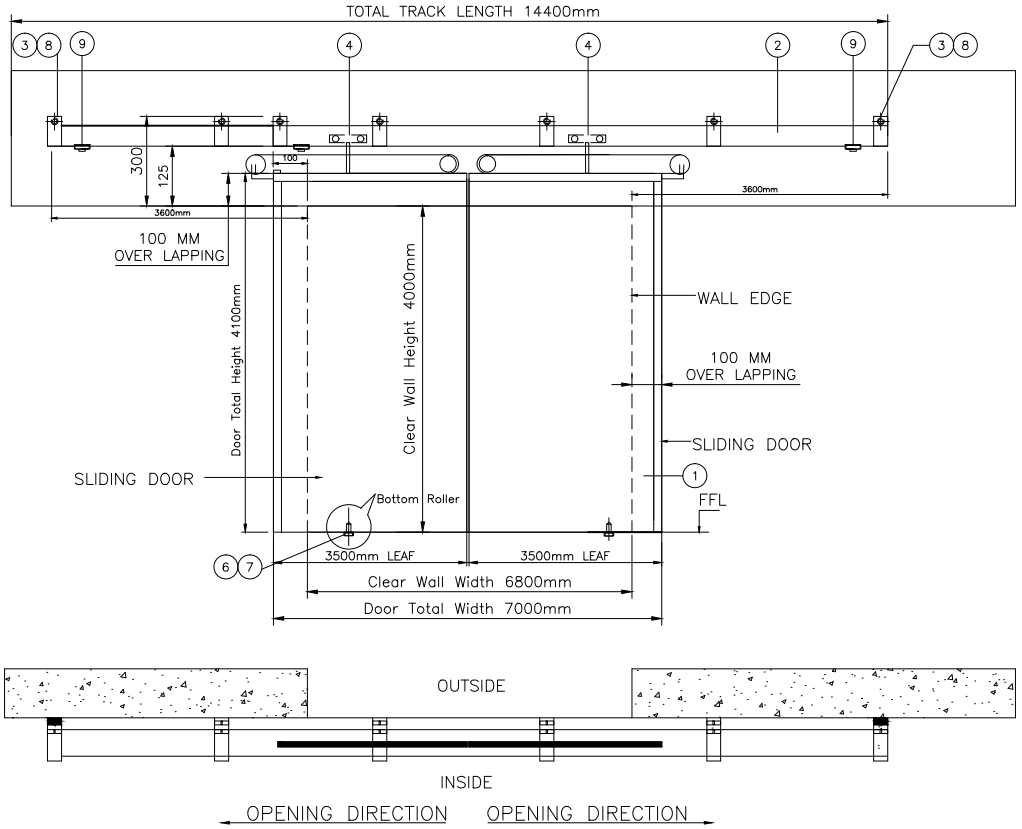

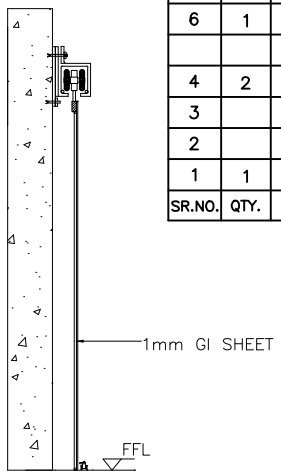

9	1	STOPPER (FOR HANGER ASSLY.)
8	1	COVER (FOR TRACK BKT.)
7	1	BOTTOM ROLLER MTG. FLAT (BOTTOM ROLLER BKT.)
6	1	BOTTOM ROLLER ASSLY.
4	2	HANGER ROLLER ASSLY.
3		TRACK BRACKET
2		SLIDING TRACK
1	1	SLIDING DOOR & FRAME / BACK SUPPORT SQ. TUBE
SR.NO.	QTY.	DESCRIPTION

DOOR DIMENSION		
CLEAR WIDTH	CLEAR HEIGHT	
6800mm	4000mm	01NOS

R01	30-07-2018	SURAJ	1.DOOR SIZE CHANGED 2.DOOR BI PARTING.	
REV. NO	DATE	DRAWN	DESCRIPTION	SIGN.

TOLERANCE:- ± 10mm

NOTE : DOOR OVERLAPING 100mm AT RH & LH AND TOP SIDE
ALL DIMENSIONS ARE IN MM.

This drawing & designing is the property of NIHVA TECHNOLOGIES. Not to be sold or copied to any other concern.

TITLE: MANUAL SLIDING DOOR			NIHVA TECHNOLOGIES PVT. LTD. PUNE Tel : 020 66304033 Email:- info@nihva.com Website:- www.nihva.com
	NAME	SIGN	DATE
DRAWN	SURAJ		25/06/18
CHECK	PRADEEP		25/06/18
APPROVAL	R.D		25/06/18
If any queries contact : design@nihva.com			DWG. NO. : NIHVA/18-19/VDR/041 REV- 01
ALL DIMENSION ARE IN mm			SCALE: NTS WT: SHEET: 01 OF 01

CLIENT -

PROJECT -

SITE LOCATION-