
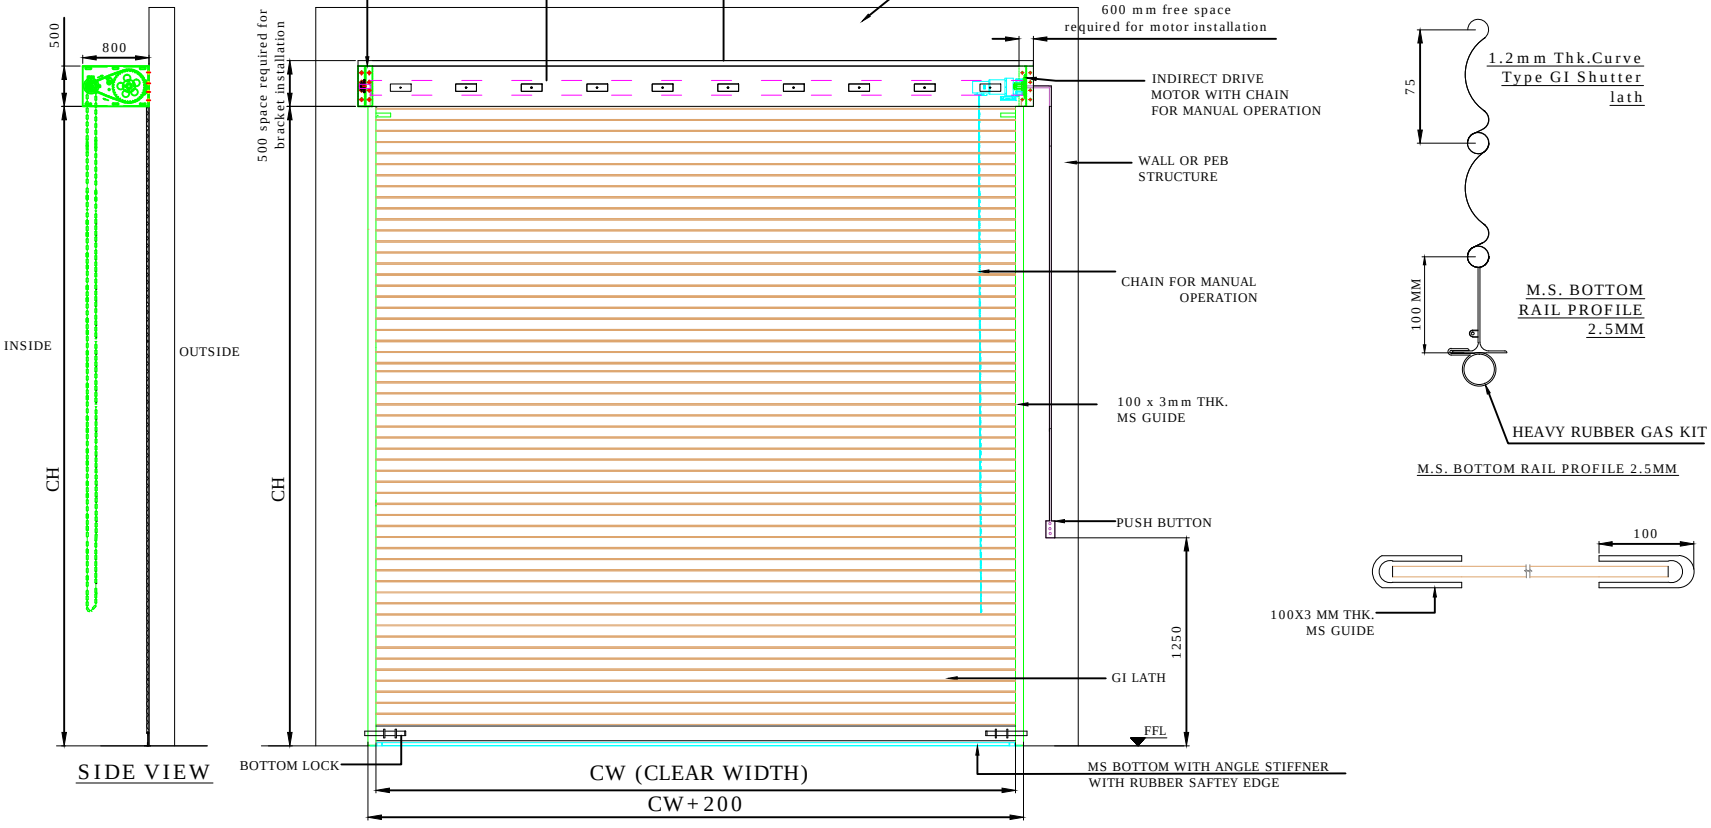


M.S. BOTTOM RAIL PROFILE 2.5MM

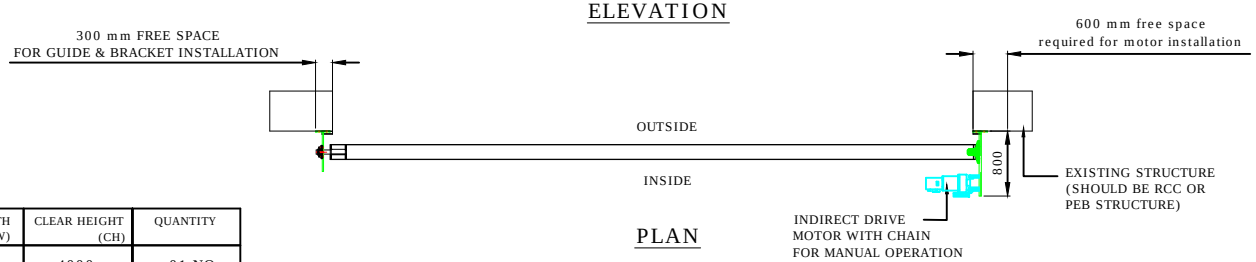

PLAN

CLEAR WIDTH (CW)	CLEAR HEIGHT (CH)	QUANTITY
4000	4000	01 NO

TOLERANCE: ±10mm

REV:-19-6-2018
1.SLAT THK. CHANGED 1mm TO 1.2mm

This drawing & designing is the property of NIHVA TECHNOLOGIES. Not to be sold or copied to any other concern.

TITLE			NIHVA TECHNOLOGIES PVT. LTD. PUNE
MOTORISED ROLLING SHUTTER			NIHVA TECHNOLOGIES PVT. LTD.
	SIGN	DATE	Tel : 020 66304033
DRAWN	SURAJ	02.06.18	Email:- info@nihva.com
CHECK	PRADEEP	02.06.18	Website:- www.nihva.com
APPROVAL	PRADEEP	02.06.18	CLIENT - Shapoorji Pallonji and Co.Pvt Ltd
MFG.			PROJECT -
If any queries contact : design@nihva.com			SITE -
ALL DIMENSION ARE IN mm			DWG. NO. : NIHVA/18-19/0050/R01 REV-01
			SCALE: NTS WT: SHEET: 01 OF 01