

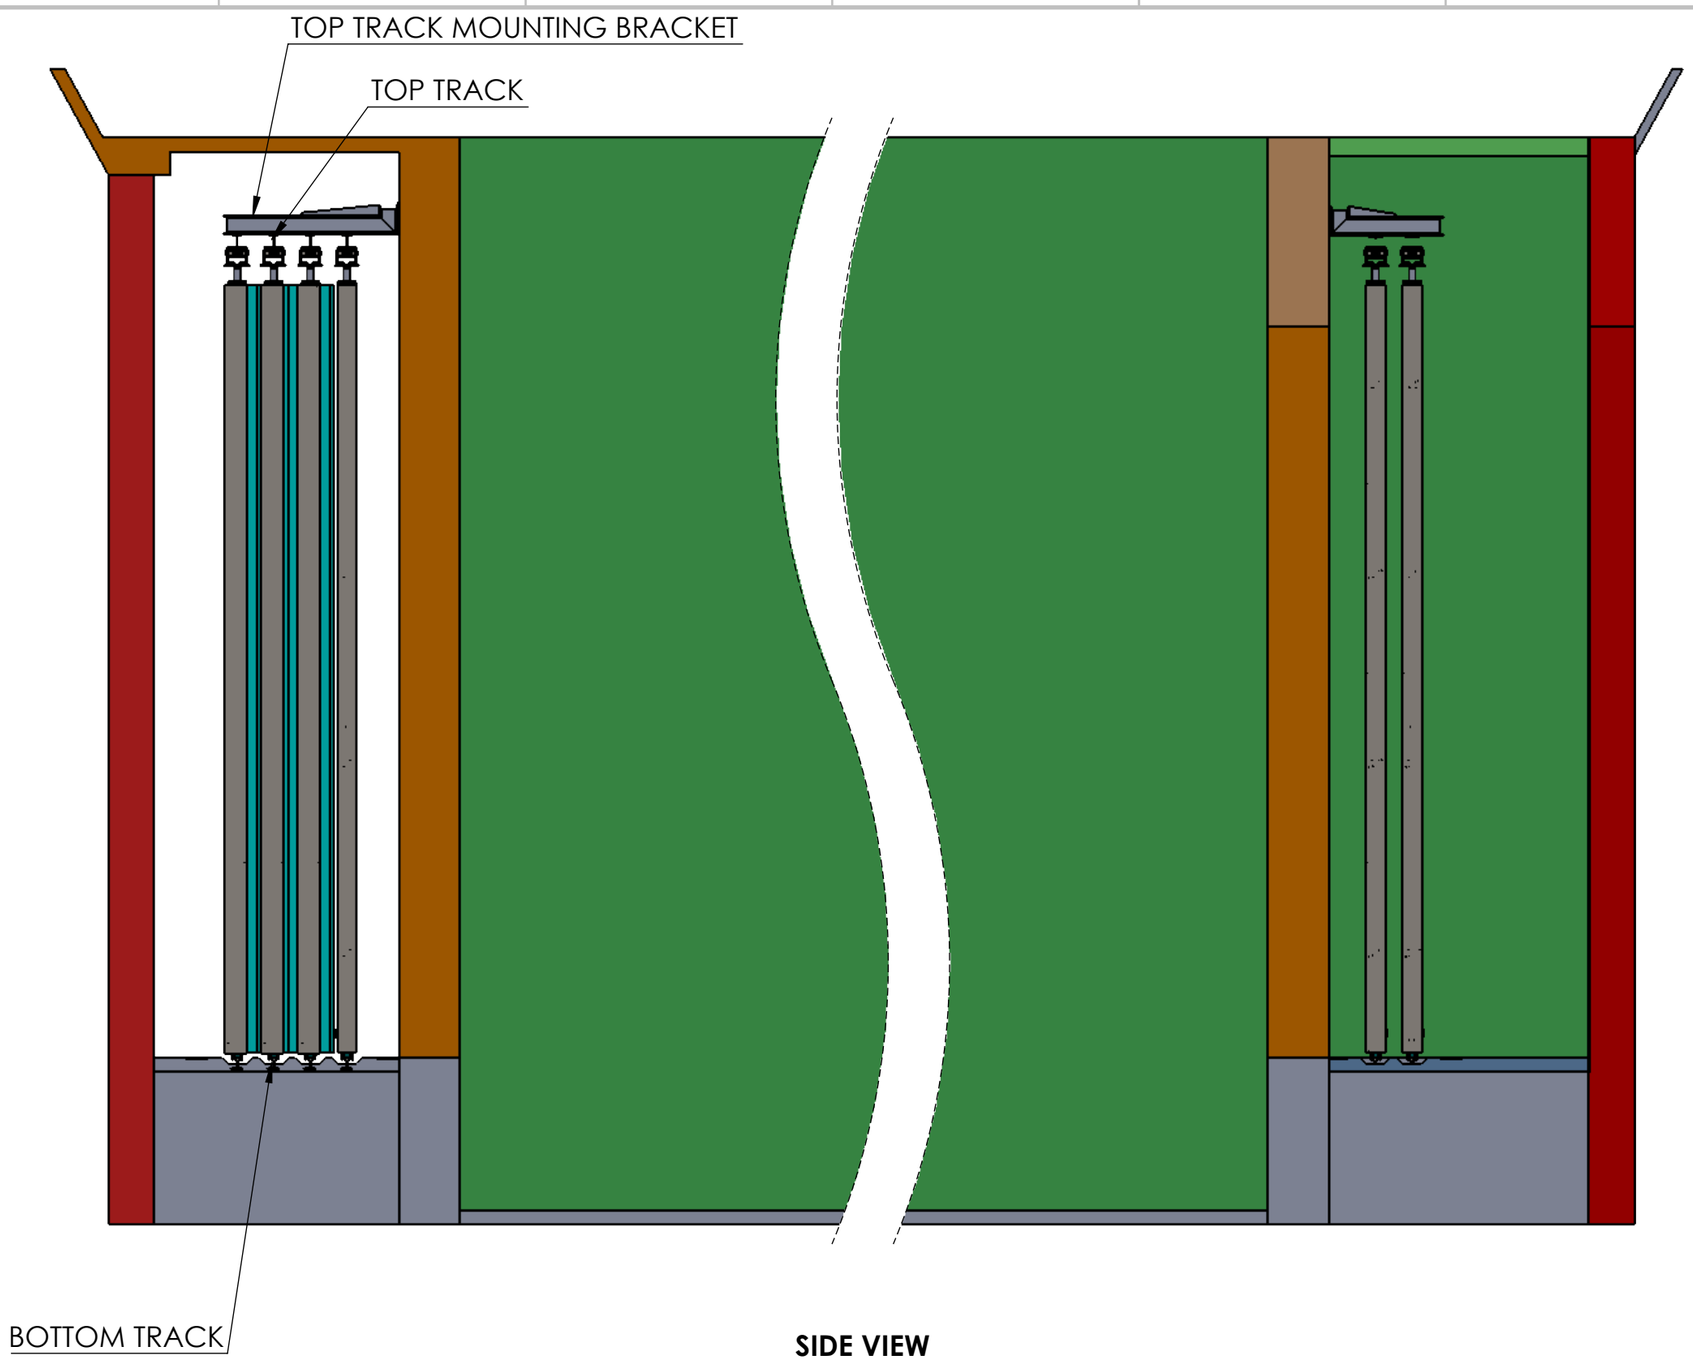



**SIDE VIEW**

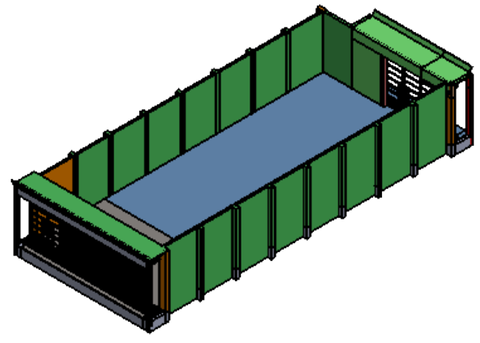


**NOTE:-**
1) TOP TRACK MOUNTING BRACKET WELD TO OUR MS PLATE AS WELL AS CHEMICAL ANCHOR ON BOTH SIDE
2) APPLY ON BOTH DOOR


| | | | | |
|---|---|---|---|---|
| TITLE - TELESCOPIC HANGER SLIDING DOOR | | | | NIHVA TECHNOLOGIES PVT.LTD.PUNE |
| DWG NO - NTPL-261-PM-001-00-000 | | | | Website - www.nihva.com |
| | NAME | SIGNATURE | DATE | PROJECT NO - NTPL261-PM |
| DRAWN | S.W | | 03-03-2025 | PRODUCT - TELESCOPIC HANGER SLIDING DOOR |
| CHK'D | P.M. | | 03-03-2025 | SITE LOCATION - KERAL |
| APPV'D | V.T. | | 03-03-2025 | |
| if any queries contact - supportautomation@nihva.com | | | | REVISION - |
| ALL DIMENSION ARE IN mm | | | A3 | SCALE - SHEET 1 OF 2 |

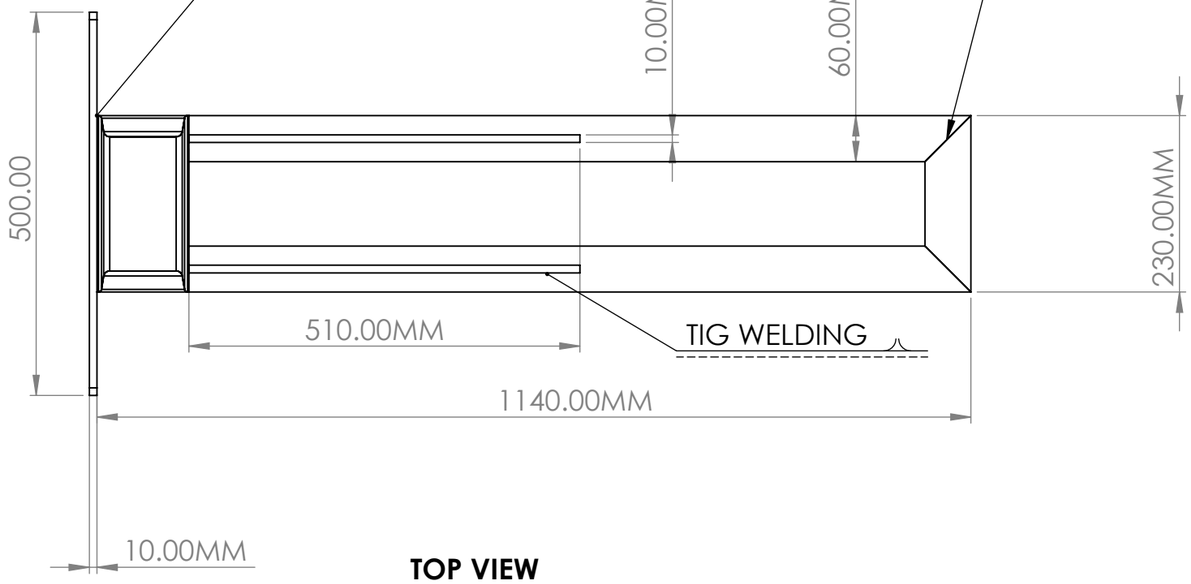



**TOP VIEW**

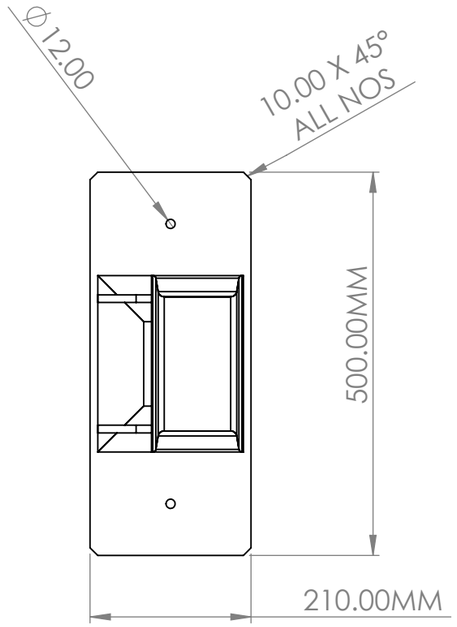


**SIDE VIEW**

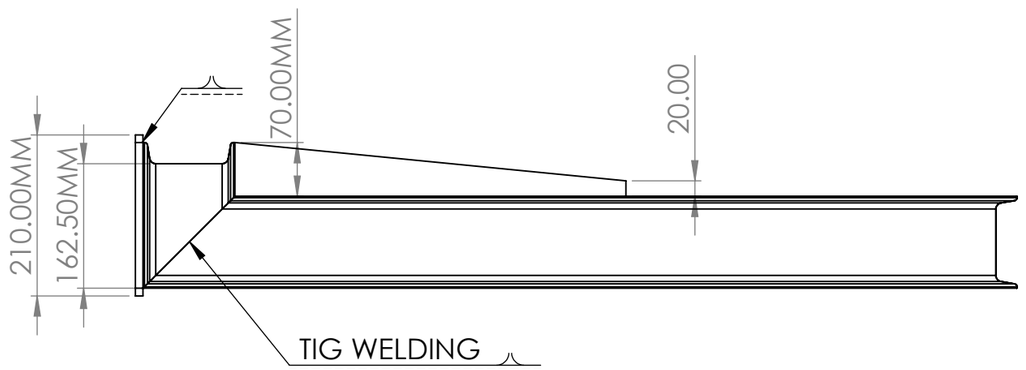


**FRONT VIEW**

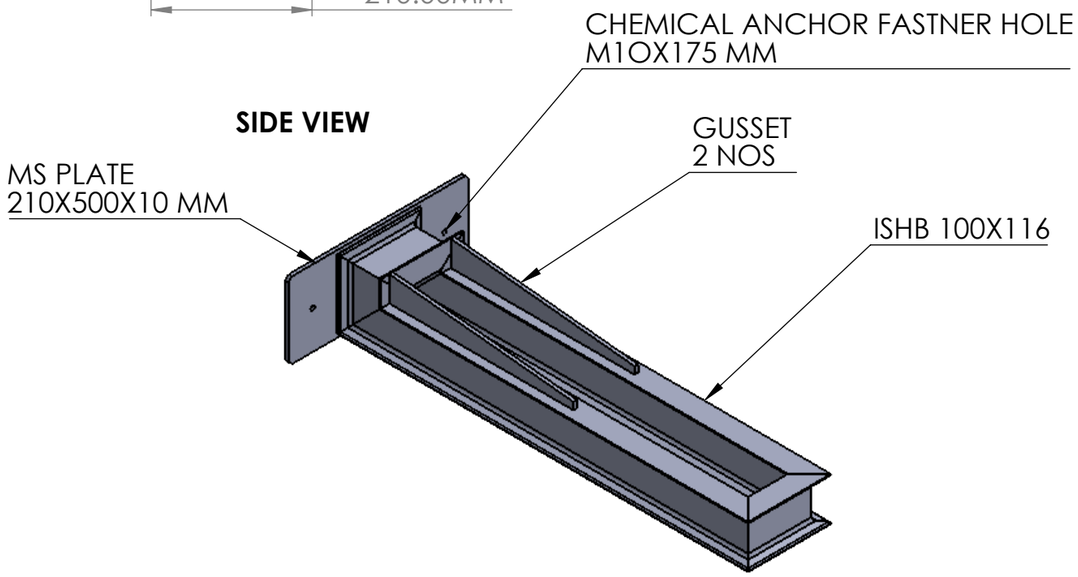


QTY:-30 NOS FOR BOTH DOOR

| | | | | |
|---|---|---|---|---|
| TITLE - TELESCOPIC HANGER SLIDING DOOR | | | | NIHVA TECHNOLOGIES PVT.LTD.PUNE<br>Website - www.nihva.com |
| DWG NO - NTPL261-PM | | | | |
| | NAME | SIGNATURE | DATE | PROJECT NO - NTPL261-PM |
| DRAWN | S.W | | 03-03-2025 | PRODUCT - TELESCOPIC HANGER SLIDING DOOR |
| CHK'D | P.M. | | 03-03-2025 | SITE LOCATION - KERAL |
| APPV'D | V.T. | | 03-03-2025 | |
| if any queries contact - supportautomation@nihva.com | | | | REVISION - |
| ALL DIMENSION ARE IN mm | | A3 | | SCALE - SHEET 2 OF 2 |