
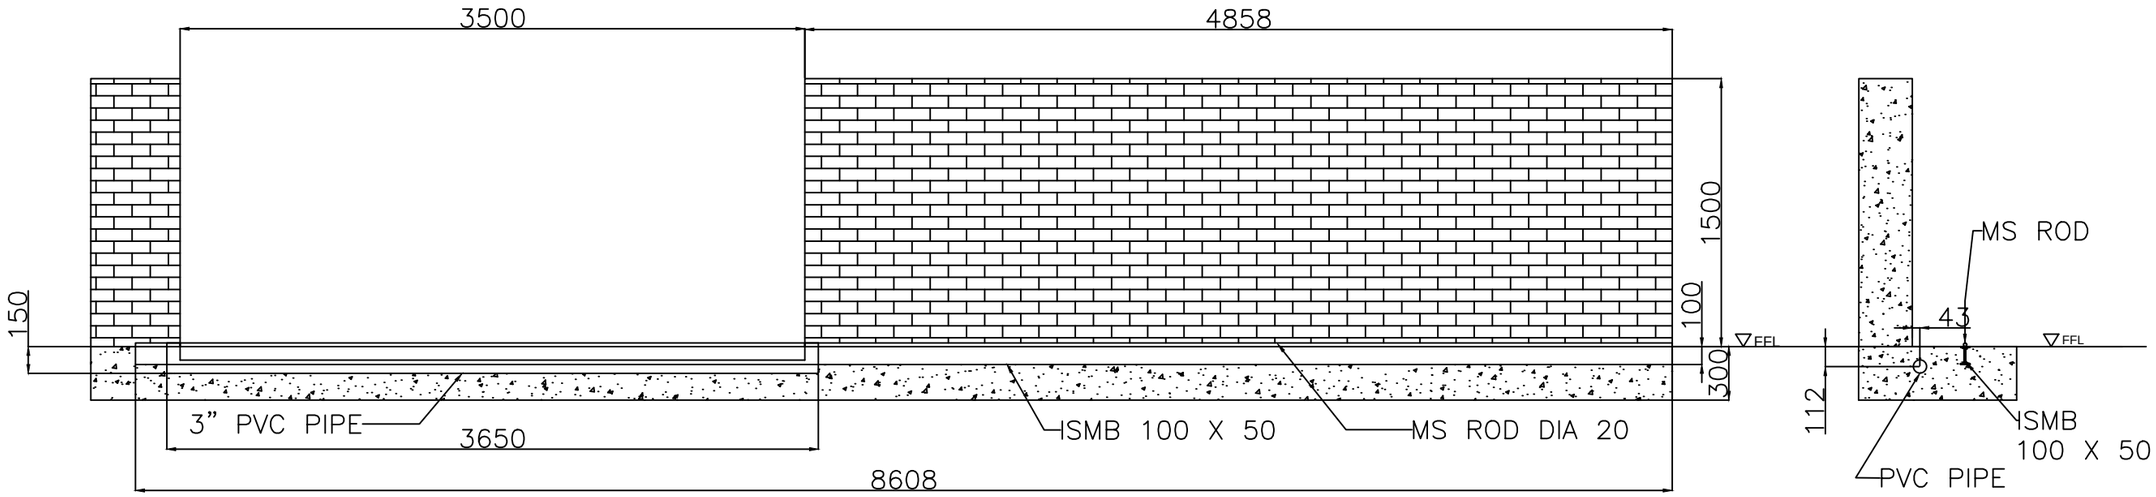


ELEVATION VIEW

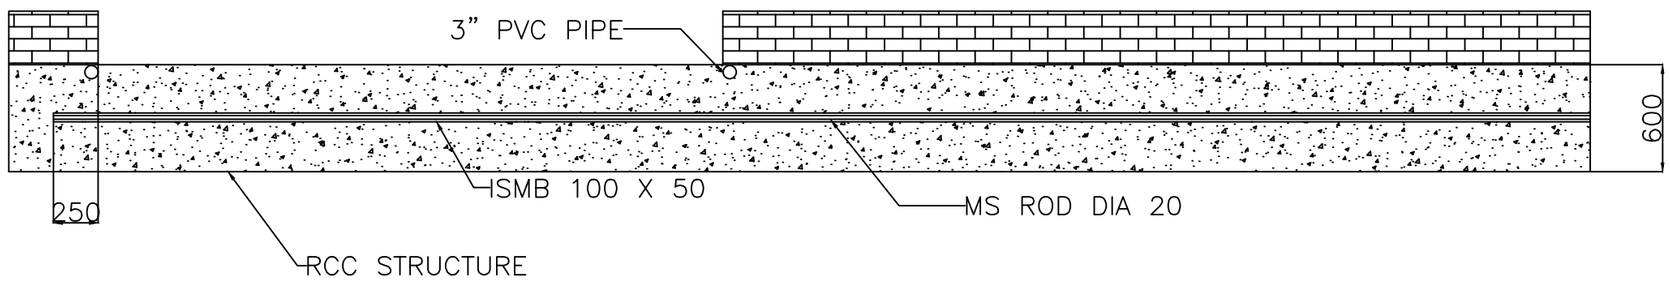

PLAN

Technical Specs of Motorized Sliding Gate

1. Parking length required - 5250mm
2. Bottom Rail - Bright bar Ø20mm
3. Total leaf weight ≈ 741 kg
4. ISMB 100 X 50 positioned in the foundation.

Note-

1. All dimension are in mm.
2. All civil work is under client scope.
3. 3" PVC pipe in the foundation to be provided by NIHVA.
4. Power supply 3 phase 440v, 50hz.
5. Cable for power supply 2.5 sqmm 4 core
6. Cable for photocell - 1.5 sqmm 4 core

This drawing & design is the property of NIHVA TECHNOLOGIES. Not to be sold or copied to any other concern.

TITLE				
SLIDING GATE FOUNDATION DRAWING				NIHVA TECHNOLOGIES PVT. LTD.
	NAME	SIGN	DATE	
DRAWN	G.P.		08.09.21	CLIENT -HAIMAVATHY PROPERTIES PVT. LTD.
CHECK	A.K.		08.09.21	LOCATION - MUMBAI
APPRD.	V.T.		08.09.21	PRODUCT - SLIDING GATE 3500 X 2000
If any queries contact : design@nihva.com				NIHVA\21-22\0229 / REV- 00
ALL DIMENSION ARE IN mm				SCALE: NTS / SHEET: 01 OF 01

NIHVA TECHNOLOGIES PVT. LTD. PUNE
Tel : 020 66304033
Email:- info@nihva.com
Website:- www.nihva.com