




PLAN

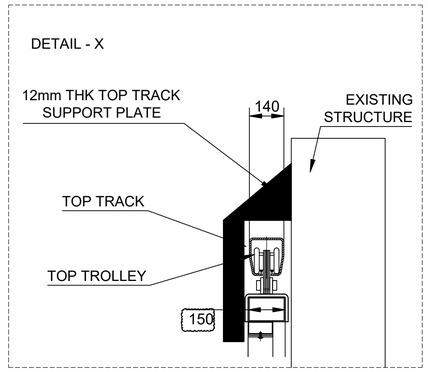

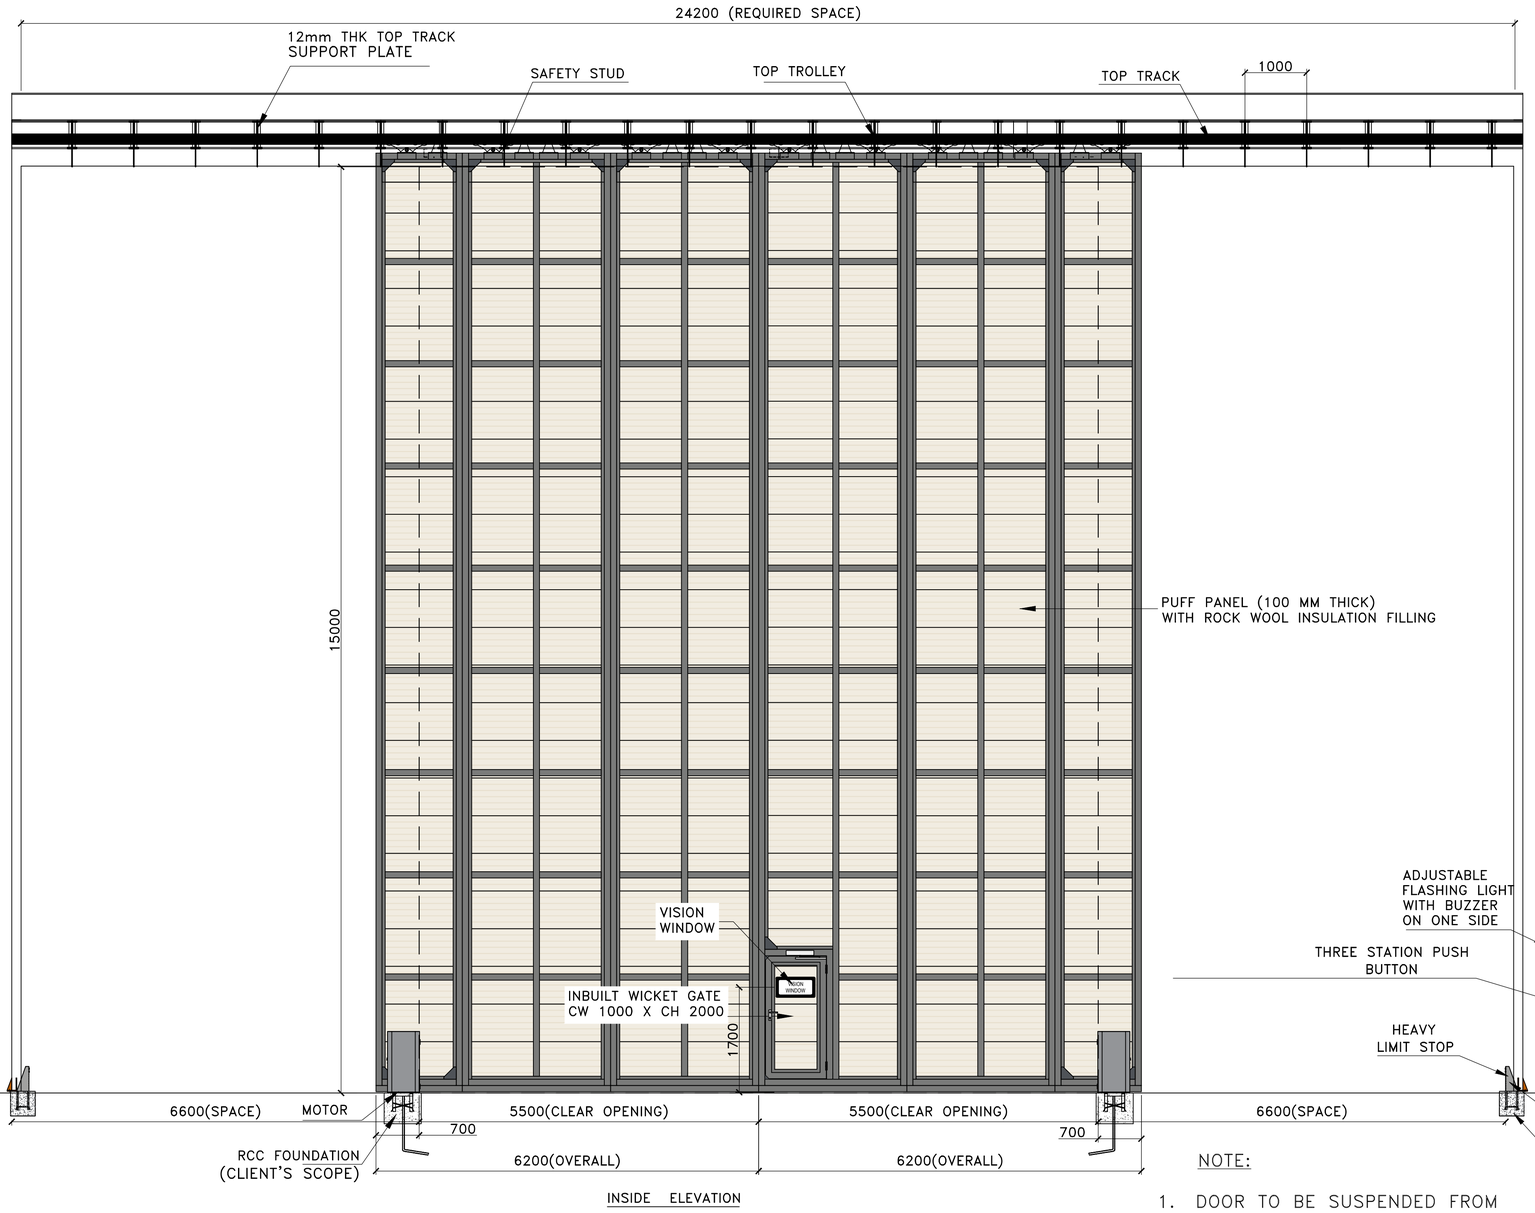

INSIDE ELEVATION

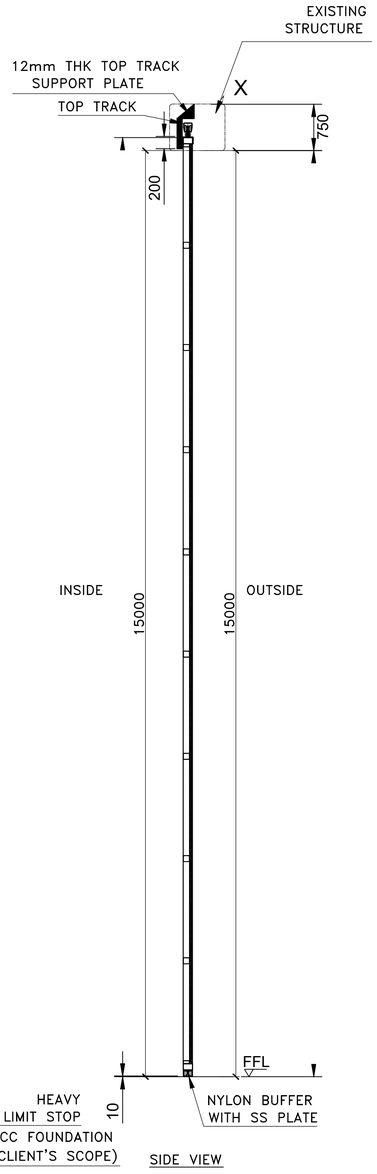

SIDE VIEW

NOTE:

1. DOOR TO BE SUSPENDED FROM TOP AND NO ROLLERS FROM FLOOR
2. MOTOR OF SUITABLE CAPACITY (EUROPEAN BRAND ONLY)
3. DOOR SHOULD BE DESIGN FOR 20KMH WIND SPEED

REFERENCE DRAWINGS

SR.NO.	DRAWING TITLE	DRAWING NO.

NOTE :-

1. DO NOT SCALE THE DRAWING. REFER TO WRITTEN DIMENSIONS ONLY. ALL MEASUREMENTS MUST BE CHECKED AND VERIFIED AT SITE. ANY DISCREPANCY FOUND,TO BE NOTIFIED TO THE CONSULTING ENGINEER BEFORE EXECUTION.
2. ALL DIMENSIONS ARE IN MM.& ALL LEVELS ARE IN METERS UNLESS OTHERWISE SPECIFIED.
3. F.G.L & F.R.L AS PER SITE ROAD LAYOUT PLAN.

ABBREVATION :-

N.G.L	= NATURAL GROUND LEVEL
F.G.L.	= FINISHED GROUND LEVEL
F.R.L.	= FINISHED ROAD LEVEL
F.F.L.	= FINISHED FLOOR LEVEL
T.O.C.	= TOP OF CONCRETE
T.O.W.	= TOP OF WALL
B.O.C.	= BOTTOM OF CONCRETE
B.O.W.C	= BOTTOM OF WALL CLADDING
B.O.P	= BOTTOM OF PORTAL
T.O.T	= TOP OF CABLE TRAY
T.O.G	= TOP OF GANTRY
T.O.B	= TOP OF BEAM
T.O.F	= TOP OF FASCIA

LEGEND :-

230MM THK. BRICK MASONRY WALL (4M WALL HEIGHT)

230MM THK. BRICK MASONRY WALL (1M WALL HEIGHT)

OPENING SCHEDULE GROUND FLOOR

TYPE	CLEAR SIZE	WITH STONE FRAME SIZE	FINISHED SILL	FINISHED LINTEL	NOS.	DESCRIPTION
ROLLING SHUTTER						
RS1	6000X6000	–	–	6000	04	MOTORIZED MS ROLLING SHUTTER
RS3	5000X5000	–	–	5000	07	MOTORIZED MS ROLLING SHUTTER
RS4	4000X5000	–	–	5000	02	MOTORIZED MS ROLLING SHUTTER
HSD1	6000X4500	–	–	4500	02	HIGH SPEED DOOR
HSD2	5000X5000	–	–	5000	02	HIGH SPEED DOOR
HSD3	4800X6000	–	–	6000	04	HIGH SPEED DOOR
HSD4	5200X6200	–	–	6200	03	HIGH SPEED DOOR
HSD5	6200X6800	–	–	6800	01	HIGH SPEED DOOR
SD1	11000X15000	–	–	15000	02	SLIDING DOOR WITH MAN ENTRY
SD2	5000X5000	–	–	5000	02	SLIDING DOOR WITH MAN ENTRY
SD3	8000X6500	–	–	6500	04	SLIDING DOOR WITH MAN ENTRY
RPD1	3000X4000	–	–	4000	02	RAPID DOOR
RPD2	4000X5000	–	–	5000	02	RAPID DOOR
DOOR						
FD	1200X2400	1400X2450	–	2450	22	EMERGENCY FIRE EXIT DOOR
D1	1200X2400	1300X2450	–	2450	11	STEEL DOOR WITH VISION PANEL
D2	1200X2400	–	–	–	16	STEEL DOOR WITH VISION PANEL (IN PEB)
D3	900 X 2400	1000X2450	–	2450	08	STEEL DOOR WITHOUT VISION PANEL
D4	750 X 2100	850X2150	–	2150	09	STEEL DOOR WITHOUT VISION PANEL
WINDOW						
W	3000X1500	3100X1600	900	2450	49	ALUMINUM FIX GLASS WINDOW STONE FRAME ON FOUR SIDE
VENTILATION						
V	3000 X 600	3100 X 700	8700	9400	23	ALUMINUM FIX GLASS WITH EXHAUST FAN
V1	1200 X 600	1300 X 700	2400	3100	11	ALUMINUM FIX GLASS WITH EXHAUST FAN
V2	3000 X 600	–	–	–	42	ALUMINUM FIX GLASS WITH EXHAUST FAN(IN PEB)

REV.	DATE	DESCRIPTION	DRN.	CHK.	APP.	PRN.
R0	13-05-26	ISSUED FOR CONSTRUCTION(TEST LAB DOOR)	JP	GJT	GJT	EMAIL

ISSUED FOR

☐ INFORMATION ☐ APPROVAL ☑ CONSTRUCTION

☐ ENQUIRY ☐ ORDER ☐ REVIEW

CLIENT : **C G POWER & INDUSTRIAL SOLUTION LTD. BHOPAL**

PROJECT : PROPOSED 45000 MVA PROJECT AT JAHANGIRPURA

CONSULTANT : SHAH & TALATI Design & Engineering

9th FLOOR, KIRTI TOWER, TILAK ROAD, VADODARA-390001, GUJARAT, INDIA.
PHONE : +91-265-2440701 / 2440726
E-MAIL : design@shahntalati.com
WEBSITE : www.shahntalati.com

PROJECT NO. :- **2537**

TITLE :- **TEST LAB DOOR DETAILS**

DRAWN BY	JANKI		R0 13 05 26
CHECKED BY	GJT		
APPROVED BY	GJT		
DRAWING NO.	**2537-FAC-A05-SH7-A1-R0**		SHEET 1 OF 1
SCALE : AS SHOWN			

THIS DOCUMENT OR DRAWING IS THE PROPERTY OF SHAH & TALATI CONSULTING ENGINEERS AND SHALL NOT, UNDER ANY CIRCUMSTANCES, BE TOTALLY OR PARTIALLY, DIRECTLY OR INDIRECTLY, TRANSFERRED, REPRODUCED, COPIED, DISCLOSED OR USED WITHOUT SHAH & TALATI'S PRIOR WRITTEN CONSENT.

A1