



ELEVATION VIEW

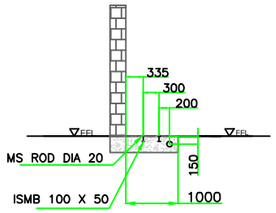

SIDE VIEW

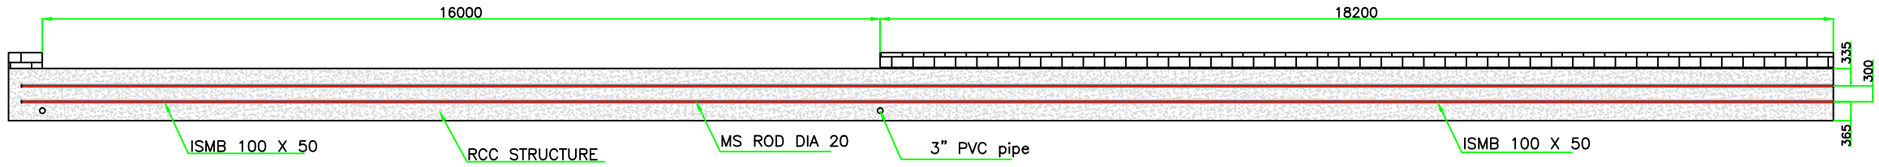

NOTE:

1. All dimensions are in mm.
2. All civil work is in client scope.
3. 3" PVC pipe should be provided for photocell wire conduit. (Client scope)
4. Power supply near motor- 3Ph, 400 V, 50 Hz (Client scope)
5. Safety: Photocell and flashlight.

This drawing & design is the property of NIHVA TECHNOLOGIES. Not to be sold or copied to any other concern.

MANUAL SLIDING GATE				NIHVA TECHNOLOGIES PVT. LTD. PUNE Tel : 020 66304033 Email:- info@nihva.com Website:- www.nihva.com
		SIGN	DATE	
DRAWN	G.P.		22.02.2022	CLIENT -SRF
CHECK	A.K.		22.02.2022	LOCATION - INDORE
APPRD.	V.T.		22.02.2022	PRODUCT - FOUNDATION DWG
If any queries contact : design@nihva.com				NIHVA\21-22\CLT\359 / REV- 00
ALL DIMENSION ARE IN mm				SCALE: NTS / SHEET: 01 OF 01