

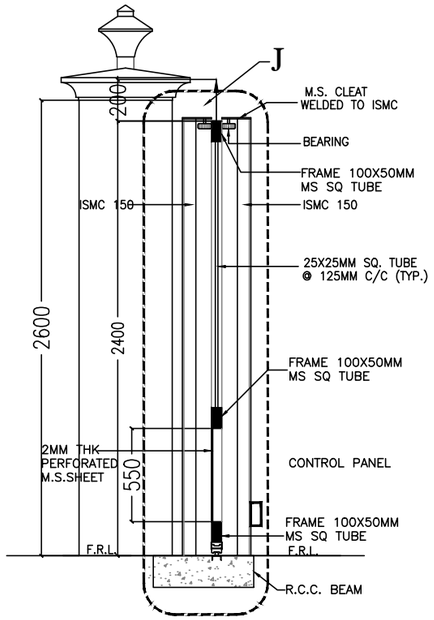



28 SECTION SCALE 1:35

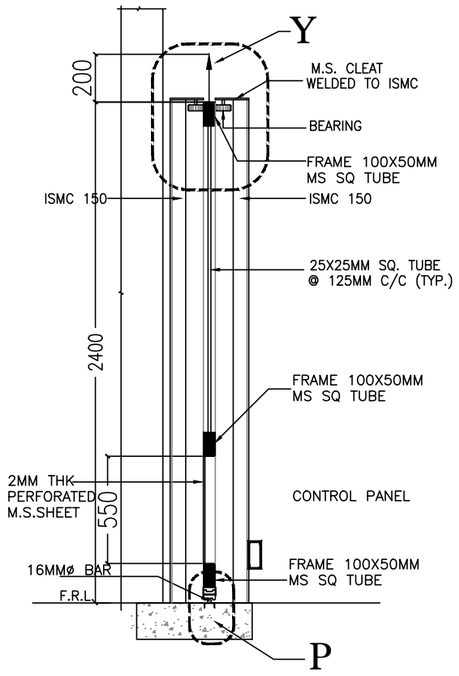


23 DETAIL OF 'J' SCALE 1:25

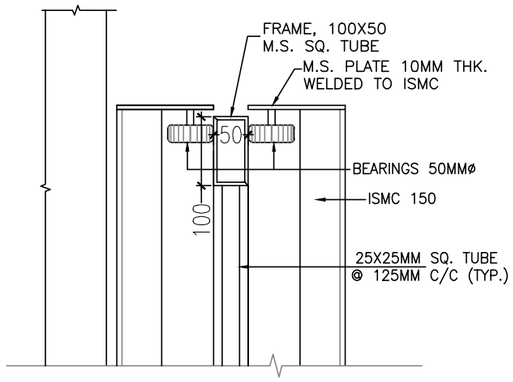


DETAIL OF 'Y' SCALE 1:8

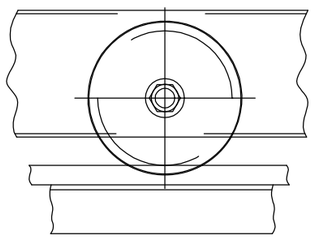


26 TYP. DETAIL SCALE 1:25

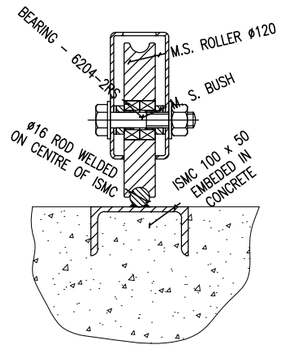

16 DETAIL OF 'P' SCALE 1:25

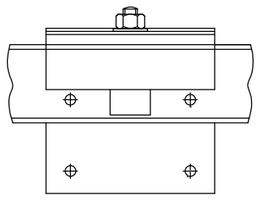

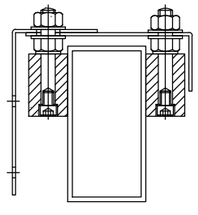

06 TYP. DETAILS SCALE 1:25

ASTUTE™
ENGINEERING SERVICES PVT. LTD.

No.	Date	Revision/Issue
RO	25-09-2024	ORIGINAL ISSUE

GENERAL NOTES :

1. ANY DRAWING TO BE REFERRED AS A PART OF THE SET ONLY AND NOT IN ISOLATION.
2. ALL DIMENSIONS ARE IN MM,UNLESS MENTIONED OTHERWISE.
3. DO NOT SCALE FROM THIS DRAWING.
4. ALL DIMENSIONS TO BE VERIFIED ON SITE.
5. THIS DRAWING IS TO BE READ IN CONJUNCTION WITH RELEVANT ARCHITECTURAL, STRUCTURAL, M, E & P DRAWINGS AND SPECIFICATIONS. CONTRACTOR SHALL CO-ORDINATE THESE DRAWINGS AND REPORT ANY DISCREPANCY FOR CLARIFICATION BEFORE PROCEEDING WITH WORKS.
6. CONTRACTOR SHALL SUBMIT SHOP DRAWING FOR APPROVAL WHEREVER ESSENTIAL.
7. CONTRACTOR WILL BE RESPONSIBLE FOR THE CHECKING AND VERIFICATION OF ALL DIMENSIONS, SIZES AND TOLERANCES NEEDED FOR THE INSTALLATIONS OF ALL EQUIPMENT AND FITTINGS THOSE THAT ARE WITHIN THE SCOPE OF THE WORK OF THE CONTRACT AS WELL AS THOSE TO BE SUPPLIED BY OTHERS. THEREFORE ALL DIMENSIONS SHOWN ON DRAWINGS RELEVANT TO THESE INSTALLATION ARE FOR GUIDANCE ONLY.
8. LEVELS MENTIONED FOR LINTELS AT DOOR AND OPENINGS ARE FROM FINISHED FLOOR LEVEL.
9. ANY DISCREPANCY IN THE DRAWINGS/DIMENSIONS/SPECIFICATIONS TO BE BROUGHT TO THE NOTICE OF CONSULTANT PRIOR TO SUBMISSION OF TENDER PRICE. ANY CLAIMS DUE TO SUCH DISCREPANCIES WILL NOT BE ACCEPTED/APPROVED LATER.
10. ALL CUTOUTS AND SLEEVES OF M.E.P. SERVICES MUST BE CLOSED AS PER METHOD SPECIFIED.
11. ALL OPENINGS DIMENSIONS SHOWN ARE STRUCTURAL OPENINGS UNLESS NOTED OTHERWISE.
12. ALL WET AREAS AND SHAFT FLOORING SHOULD HAVE WATER PROOFING LAYER AS PER SPECIFICATIONS.

Project Name

HODEK VIBRATION TECHNOLOGIES PVT LTD
BELUR INDUSTRIAL AREA,
TALUKA- DHARWAD, KARNATKA.

Sheet Title

TYP. ENTRANCE GATE DETAILS

Sheet Number

ARCH-WD-116A-R0

Date	Scale	Drawn	Checked
25.09.24	AS SHOWN	VILAS	SM

THIS DRAWING IS THE COPY RIGHT PROPERTY OF ASTUTE ENGG. SERVICES PVT. LTD. ANY MISUSE, DUPLICATION, ALTERATION OR REUSE FOR ANOTHER PURPOSE IS STRICTLY PROHIBITED & SHALL BE DEALT LEGALLY.