

Weitergabe sowie Vervielfältigung dieses Dokuments, Verwertung und Mitteilung seines Inhalts sind nur nach vorheriger ausdrücklicher schriftlicher Zustimmung von SMS Meer GmbH gestattet. Das Dokument ist vor unberechtigtem Zugriff Dritter zu schützen. Zuwiderhandlungen verpflichten zu Schadensersatz. Alle Rechte aus Patent-/Gebrauchsmuster-/Markenschutz vorbehalten.

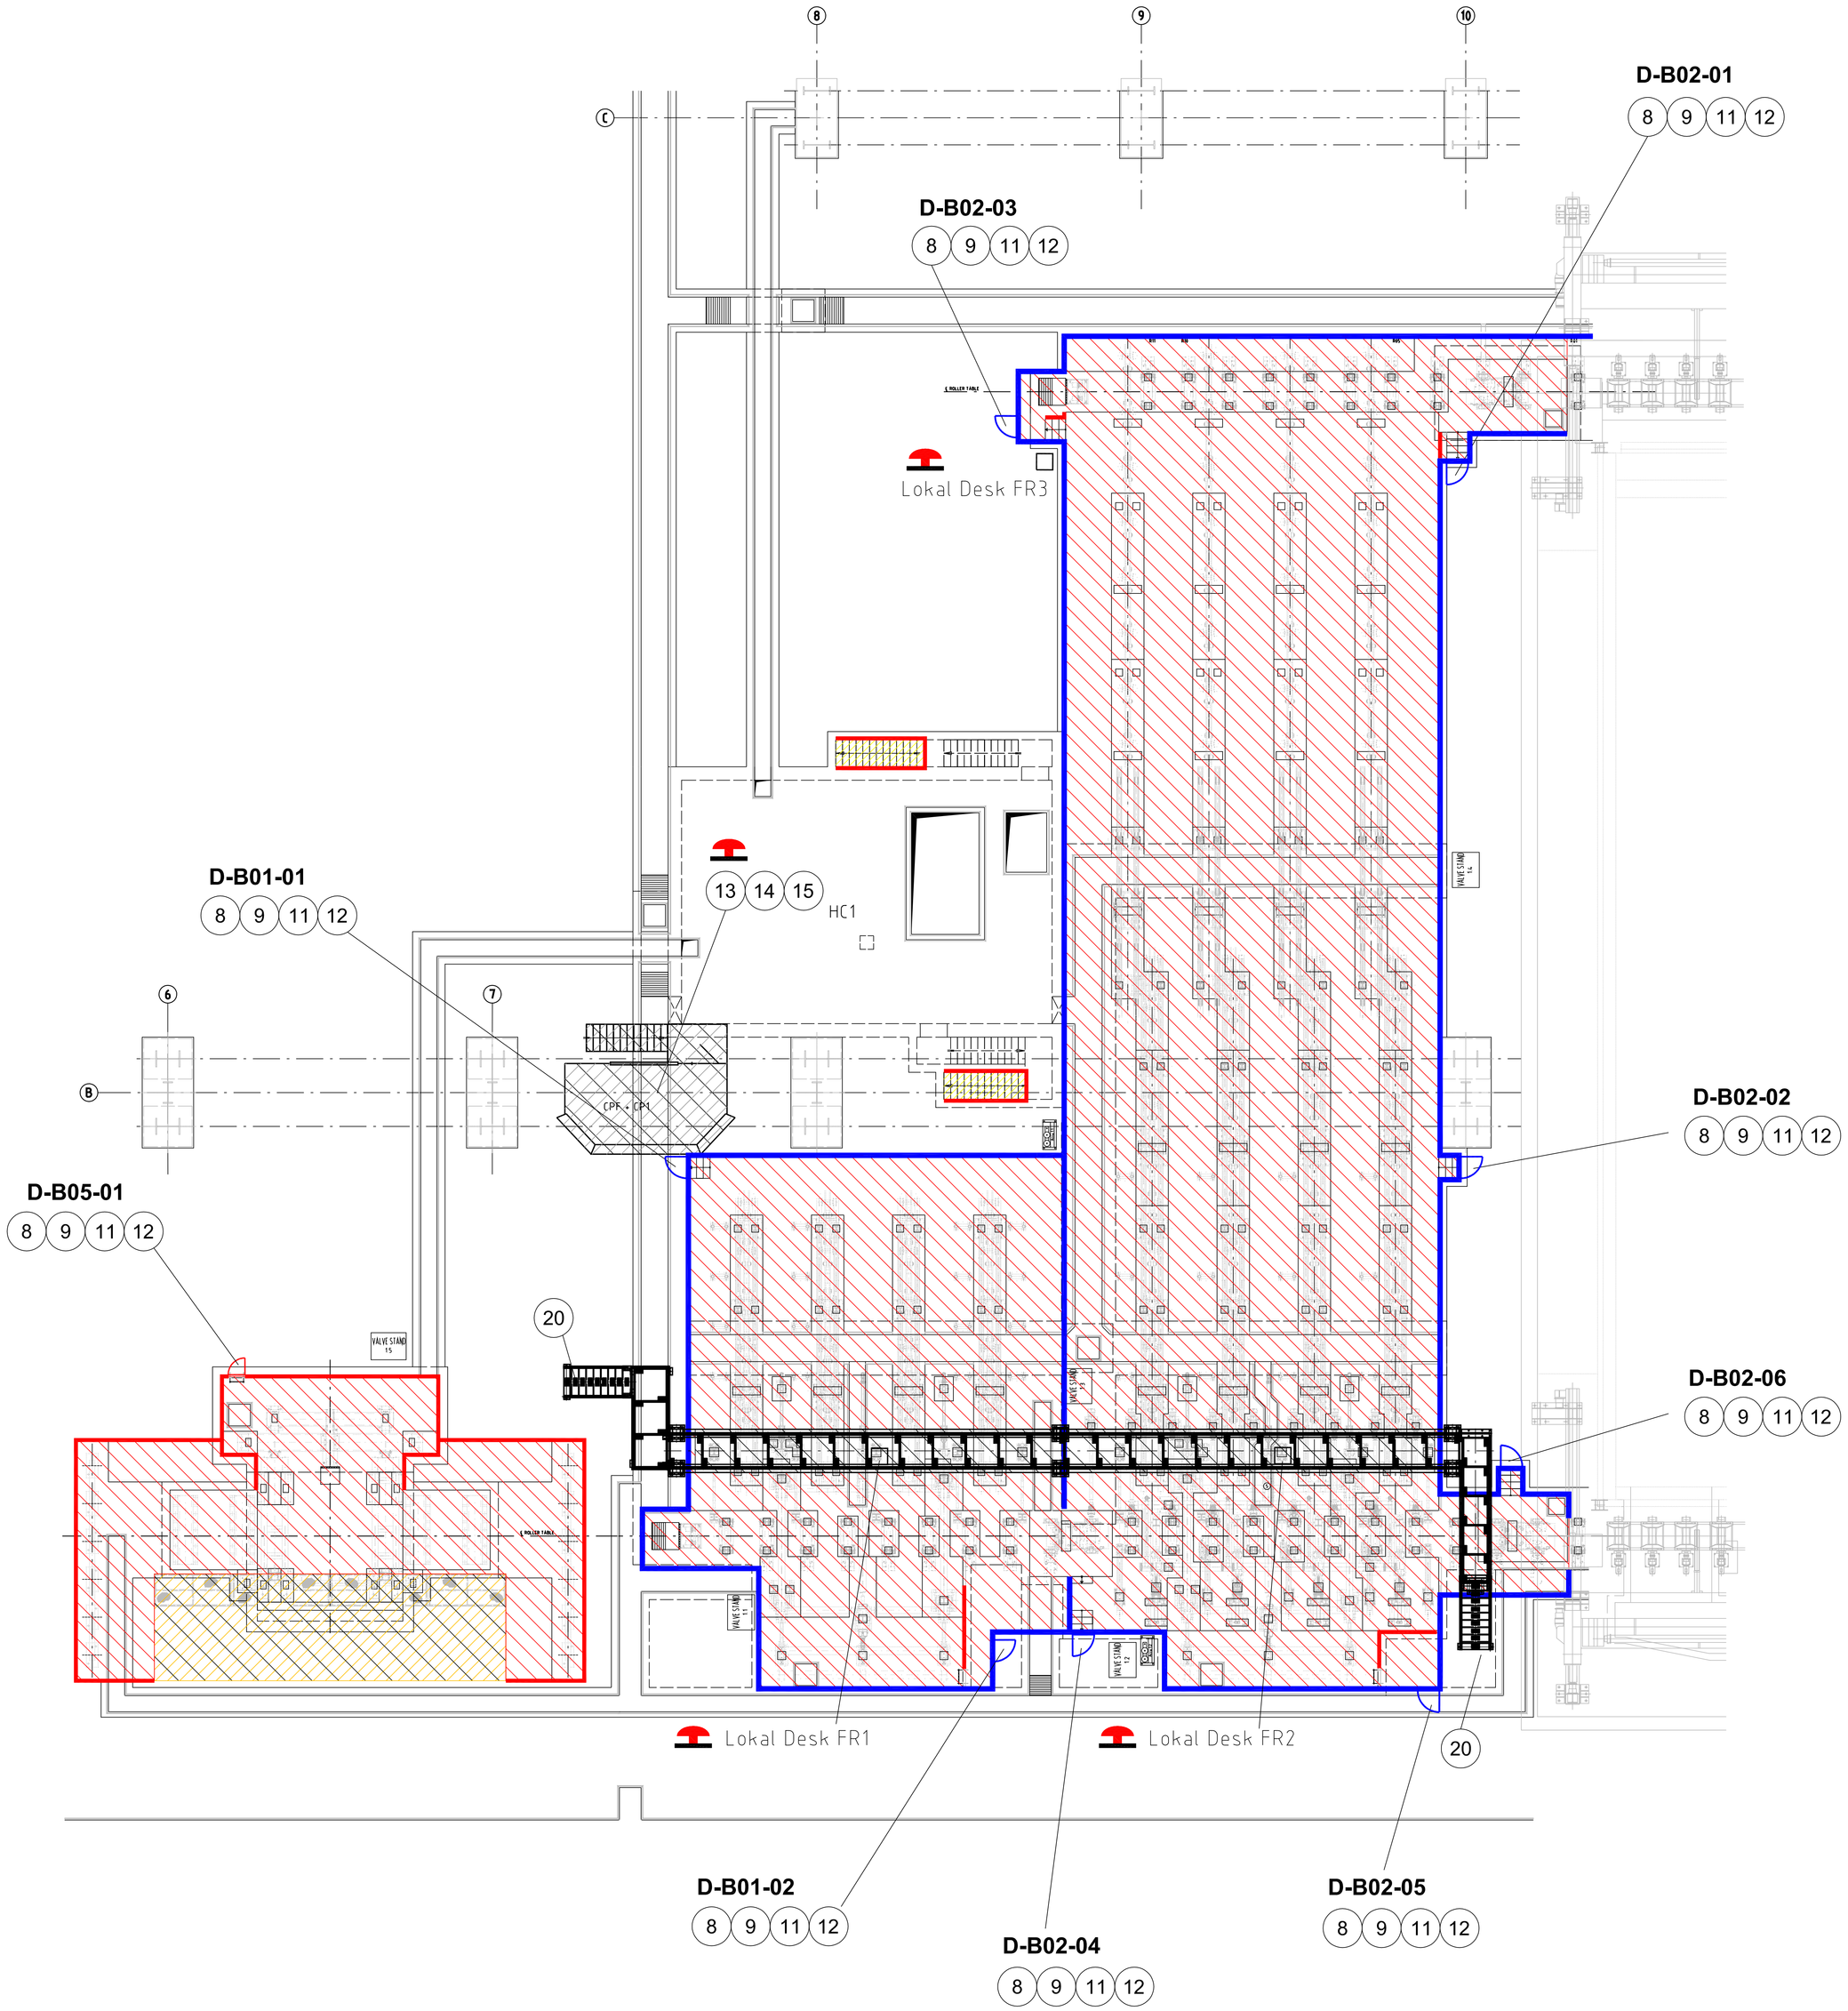

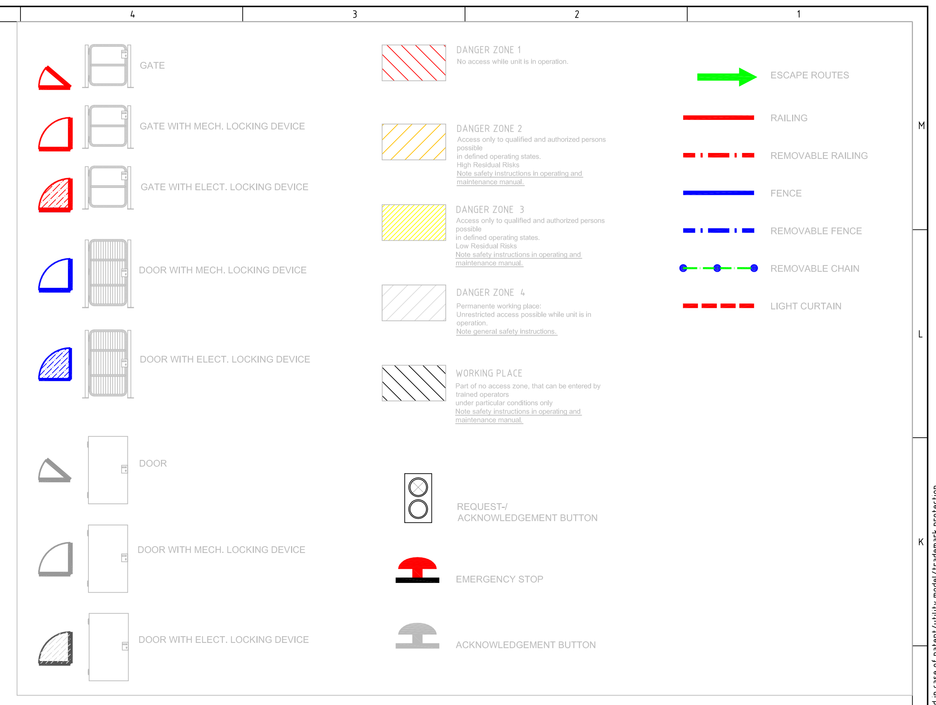

9463.0000 / RAILBHL

CATEGORY OF DRWG.	APPROVAL	INFORMATION	REFERENCE	RECORD	CONSTRUCTION

BHILAI STEEL PLANT, BHILAI, CHATTISGARH
7,0 MTPA EXPANSION

मेकॉन लिमिटेड
MECON LIMITED

VENSDOR'S NAME: SMS Meer/SMS Meer India/ABB
PACKAGE DESCRIPTION: UNIVERSAL RAIL MILL (Pkg No-047)
TITLE OF DRAWING. PARTITION1, SAFETY LAYOUT
SCALE-
VENDOR'S DRG NO.-
PROJECT DRG. NO. BSP-SMS Meer-08-047-21-130-35-BE-06650 REV. -

Fertigungsvorschriften / Manufacturing Instructions: SN 200
Ursprung / Origin | Fertiggewicht / Finished weight | Modell-Nr / Pattern-No
Werkstoff / Material: kG
Projektionsmethode 1 / First angle projection method ISO 128

	Datum / Date	Name
Bearb. / Drawn	27.09.11	Fryen
Gepr. / Checked	27.09.11	Pratzel
Norm. / Std.		

Typ / type: Safety Layout
Benennung / Title: Teilbereich 1
Title: PARTITION 1
Sach-Nr: 0100133-00.650
Drawing-No
Maßstab / Scale: 1:100
Blatt / Sheet: 01 Blattzahl / Sheets: 01

SMS MEER SMS group

Ausgabe / Issue	Änderung / Revision	Datum / Date	Name

Ersatz für / Supersedes
Ersatz durch / Superseded by

The reproduction, distribution and utilization of this document as well as the disclosure of its content to others without prior explicit written consent of SMS Meer GmbH is prohibited. Holder has to protect this document against unauthorized withdrawal of third parties. Offenders will be held liable for the payment of damages. All rights reserved in case of patent/utility model/trademark protection.

Diese Zeichnung und alle darauf enthaltenen Informationen sind vertraulich. This drawing and all information on it is confidential.

A0