

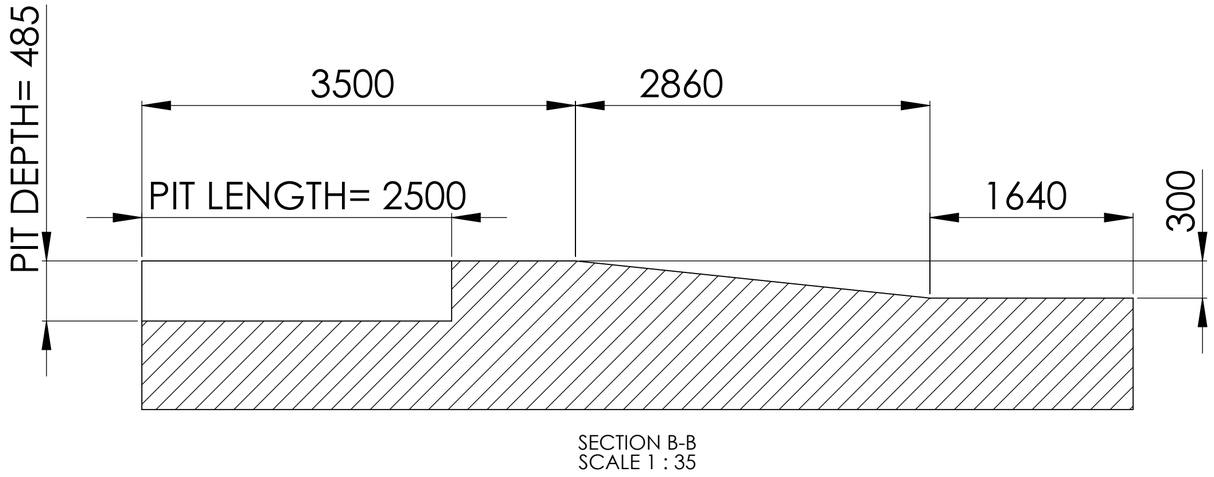



SECTION B-B
SCALE 1 : 35

SECTIONAL VIEW OF PIT WITH RAMP

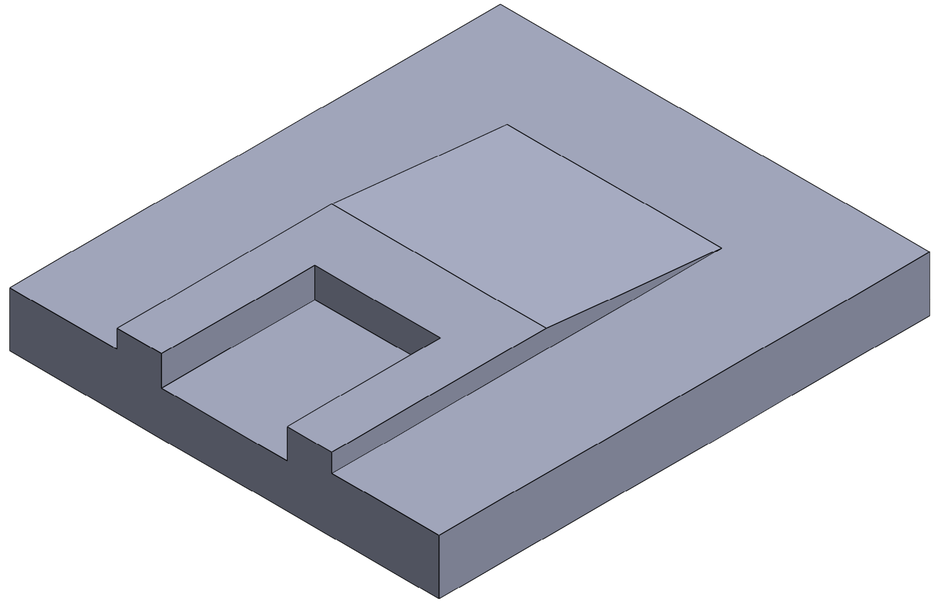

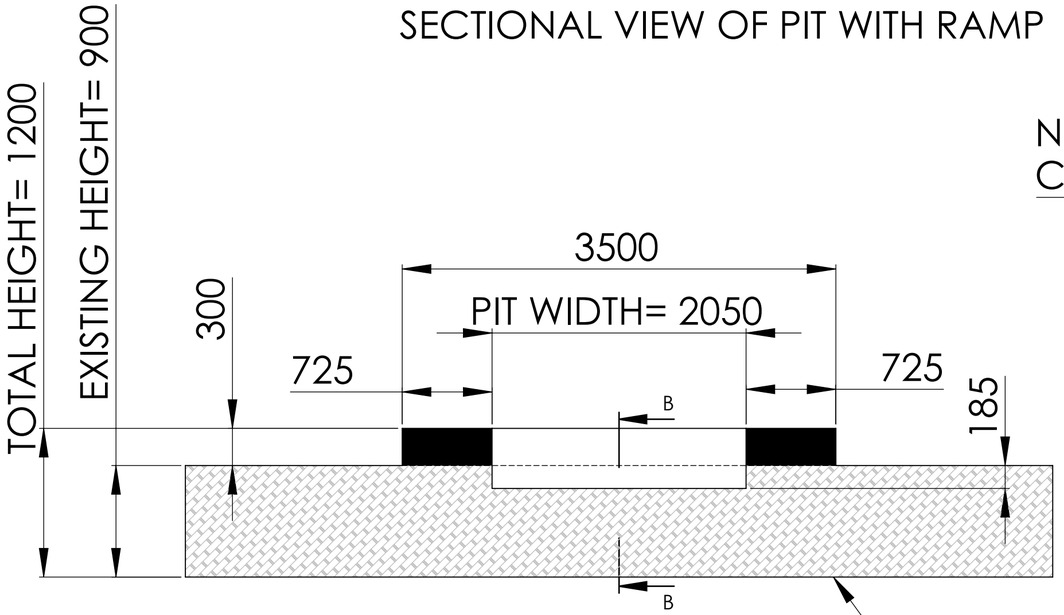

FRONT VIEW OF DOCK
LEVELER PIT

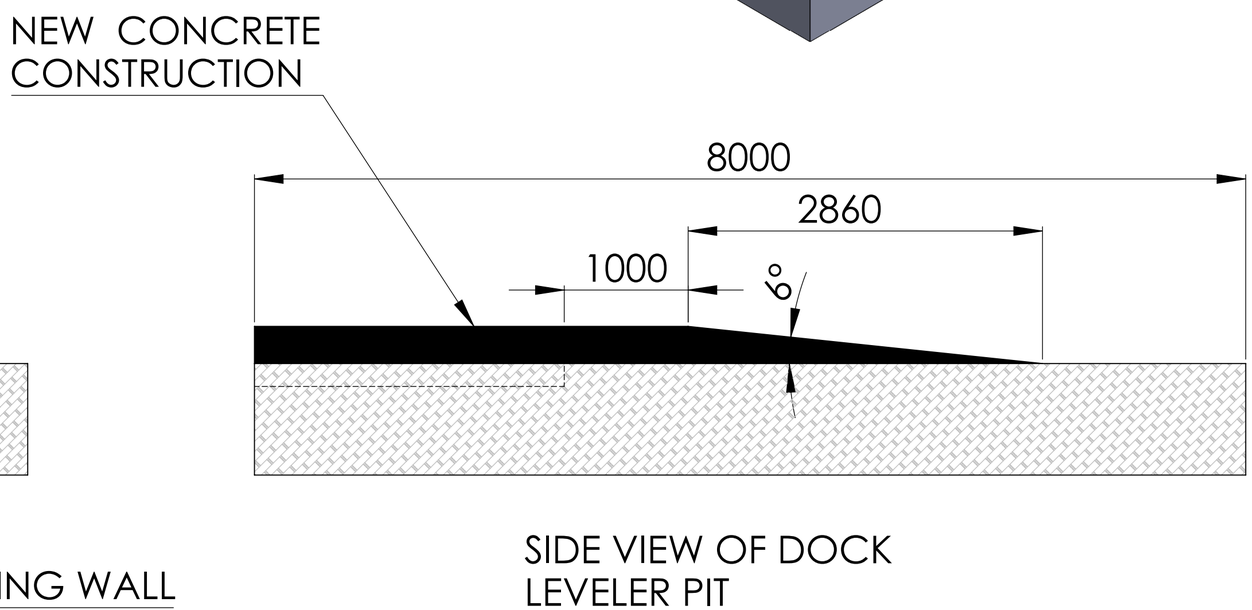

SIDE VIEW OF DOCK
LEVELER PIT

UNLESS OTHERWISE SPECIFIED: DIMENSIONS ARE IN MILLIMETERS SURFACE FINISH: TOLERANCES: LINEAR: ANGULAR:	FINISH:				DEBURR AND BREAK SHARP EDGES	DO NOT SCALE DRAWING / REVISION
	NAME	SIGNATURE	DATE			TITLE: NIHVA/20-21/0144
DRAWN	SIDDHESHWAR		25.1.2021			
CHK'D						
APPV'D						
MFG						
Q.A				MATERIAL:		DWG NO. RAMP FOR DL / A2
				WEIGHT:		SCALE:1:50 / SHEET 1 OF 1