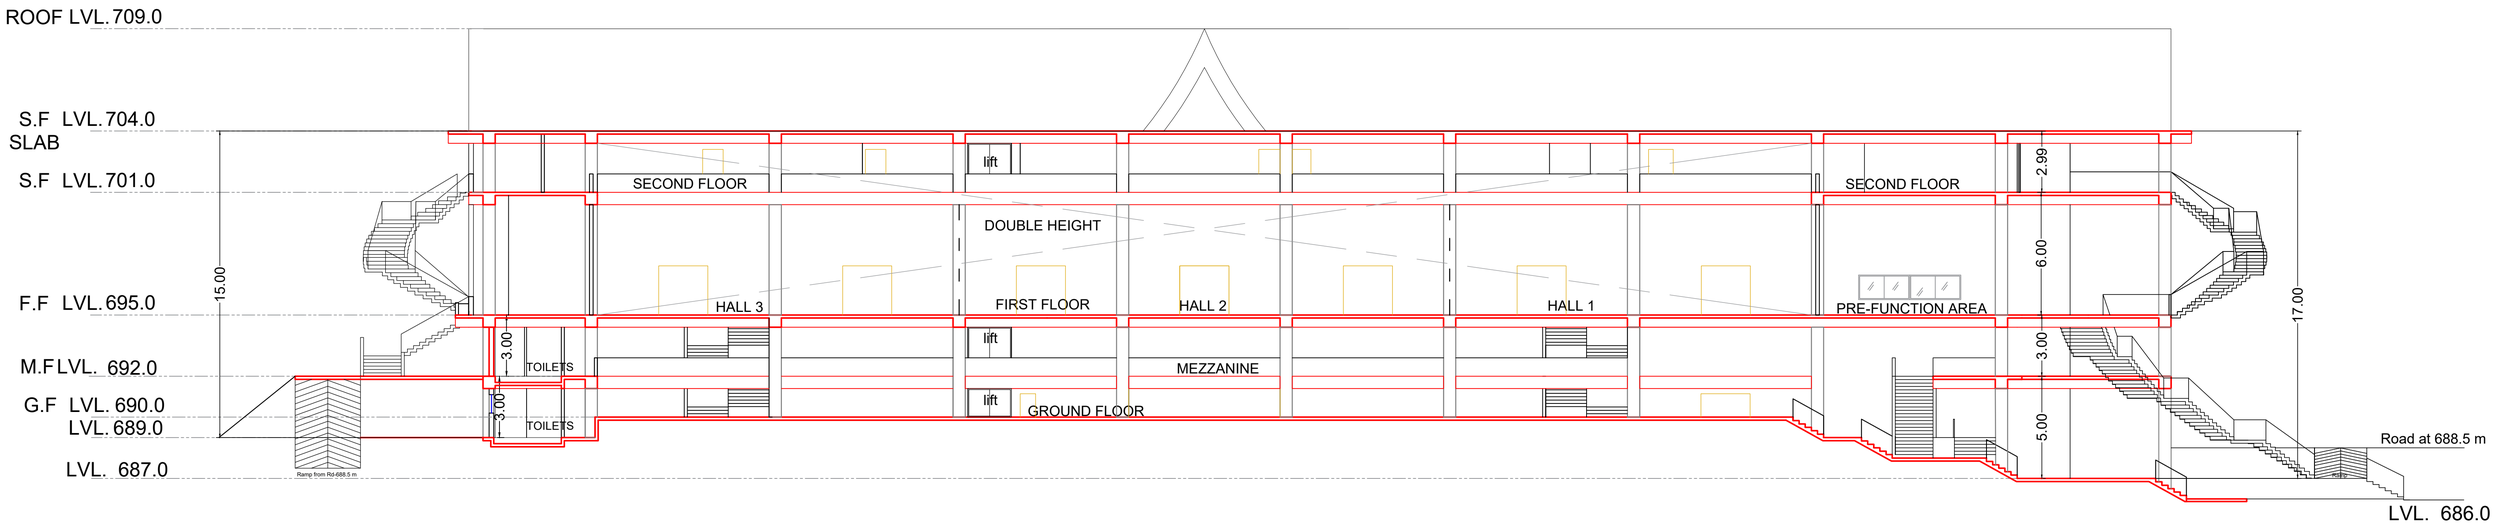

ROOF LVL. 709.0
S.F LVL. 704.0
SLAB
S.F LVL. 701.0
F.F LVL. 695.0
M.F LVL. 692.0
G.F LVL. 690.0
LVL. 689.0
LVL. 687.0
15.00
3.00
3.00
SECOND FLOOR
DOUBLE HEIGHT
FIRST FLOOR
GROUND FLOOR
MEZZANINE
HALL 3
HALL 2
HALL 1
TOILETS
TOILETS
lift
lift
lift
SECOND FLOOR
PRE-FUNCTION AREA
2.99
6.00
3.00
5.00
17.00
Road at 688.5 m
LVL. 686.0
Ramp from Rd-688.5 m

SECTION BB