


Abbrevation's:
WOW-Wall Opening Width
WOH-Wall Opening Height
UC-Under Cut
FFL-Finished Floor Level

## ASSESORIES DETALES


(a) HINGES: SS Ball bearing butt hinges 100x75x3mm.

(b) LOCK: Mortise dead lock,Cylinder( one side key& thumb turn other side) with escutcheon.


(c) DOOR CLOSER

(d) HANDLE : D Handle(254mm)


**Shutter thickness : 47 mm**
**Frame Sheet thick : 1.2mm**
**Shutter sheet thick : 0.8mm**
**Fixing : On Soliid Brick plasterd wall with Anchors**
**Electrostatic powder coated**

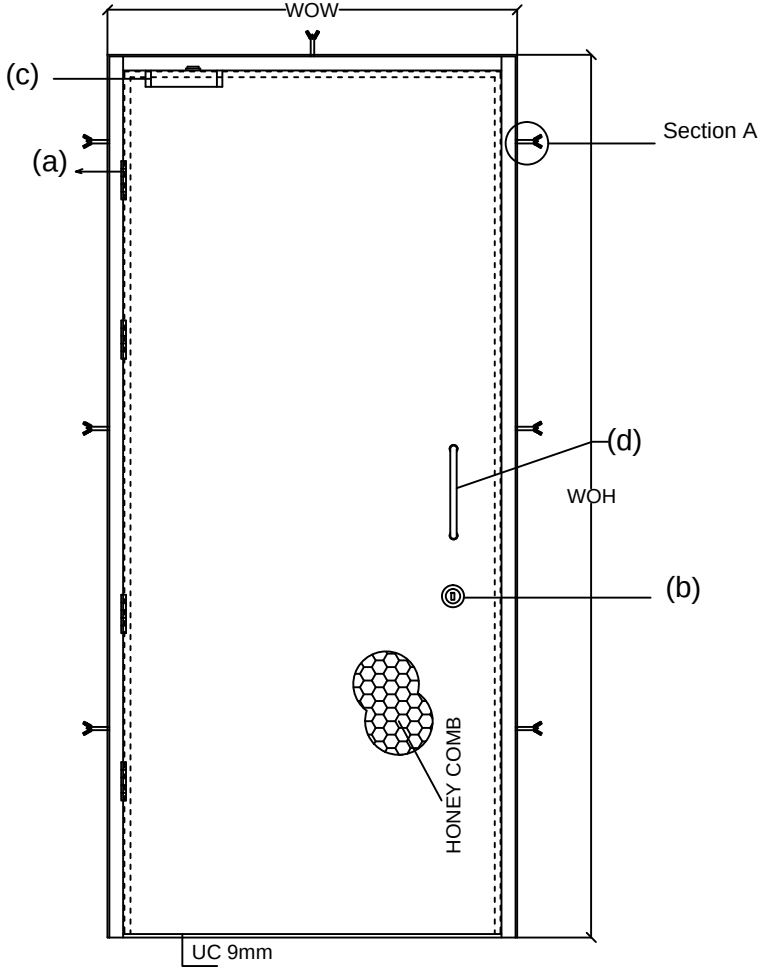


Elevation

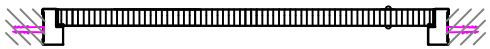

Top View

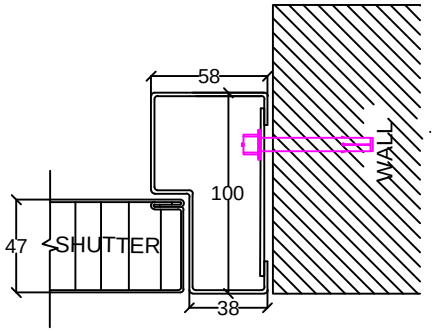


Detail view of Section A

NOTE:- *All Dimensions are in mm.
*Tolerance:-All Linear Dimensions ±3mm,Others ±0.5mm.
*The Drawing Is For Location of Hardware only. Drawing Does Not Represent The Hardware For More Clarity, Please Go Through Hardware Broucher.

| DOOR TYPE | WOW | WOH | TYPE 1 | TYPE 2 | TYPE 3 | TYPE 4 | TOTAL |
|---|---|---|---|---|---|---|---|
| STEEL DOOR | 1200 | 2200 | | | | | 6 |

Client should mention door handling type from door handling sheet.

COLOR - RAL 7035 LIGHT GREY

This drawing & designing is the property of NIHVA TECHNOLOGIES. Not be sold or copy to any other concern.

# SINGLE LEAF STEEL DOOR

CLIENT APPROVAL

ALL DIMENSION ARE IN mm

| | NAME | DATE | SIGN. |
|---|---|---|---|
| DRAWN | OMKAR | 31/08/16 | |
| CHECK | ANIL | 31/08/16 | |
| REV. | 0 | | |
| APPRD. | | | |
| MFG | | | |

NIHVA TECHNOLOGIES PVT. LTD.
NIHVA TECHNOLOGY PVT. LTD. PUNE
Tel : 020 66304033
Email:- info@nihva.com
Website:-www.nihva.com

CLIENT - INDOSPACE
PROJECT - RVK INDUSTRIAL PARK PVT. LTD.
SITE - RANJANGAON
DWG. NO. - NIHVA/16-17/0066
SCALE: NTS | WT: | SHEET: 01 OF 01
If any queries contact : projects@nihva.com